



งานจ้างเหมาก่อสร้างอาคารสถานีโครงข่ายเคเบิลใต้น้ำปากบารา อำเภอละงู จังหวัดสตูล และ
งานปรับปรุงอาคารชุมสายโทรศัพท์สงขลา จังหวัดสงขลา พร้อมงานระบบไฟฟ้าสำรอง
งานติดตั้งระบบปรับอากาศ และงานรื้อถอน

ประกอบด้วย

1. งานจ้างเหมาก่อสร้างอาคารสถานีโครงข่ายเคเบิลใต้น้ำปากบารา อำเภอละงู จังหวัดสตูล พร้อมงานระบบไฟฟ้าสำรอง งานติดตั้งระบบปรับอากาศ และงานรื้อถอน
2. งานจ้างเหมาปรับปรุงอาคารชุมสายโทรศัพท์สงขลา จังหวัดสงขลา พร้อมงานระบบไฟฟ้าสำรอง งานติดตั้งระบบปรับอากาศ และงานรื้อถอน
3. งานจ้างเหมาปรับปรุงสถานี ILA Site ที่ชุมสายโทรศัพท์สตูล จังหวัดสตูล พร้อมงานติดตั้งระบบปรับอากาศ และงานรื้อถอน
4. งานจ้างเหมาปรับปรุงสถานี ILA Site ที่ชุมสายโทรศัพท์ควนลัง จังหวัดสงขลา พร้อมงานติดตั้งระบบปรับอากาศ และงานรื้อถอน
5. งานจ้างเหมาปรับปรุงสถานี ILA Site ที่ชุมสายโทรศัพท์รัตภูมิ จังหวัดสงขลา พร้อมงานติดตั้งระบบปรับอากาศ และงานรื้อถอน
6. งานจ้างเหมาต่อเติมอาคารสถานีเคเบิลใต้น้ำภายในประเทศเดิม ชุมสายโทรศัพท์สงขลา จังหวัดสงขลา พร้อมงานติดตั้งระบบปรับอากาศ และงานรื้อถอน
7. งานจ้างเหมาย้ายเสา TOWER 3G ที่ชุมสายโทรศัพท์ปากบารา อำเภอละงู จังหวัดสตูล
8. งานจ้างเหมาย้ายตู้ MOBILE EXCHANGE ที่ชุมสายโทรศัพท์ปากบารา อำเภอละงู จังหวัดสตูล และย้ายอุปกรณ์ MICROWAVE ที่ชุมสายโทรศัพท์รัตภูมิ พร้อมจัดหาระบบสื่อสารสัญญาณ ที่ชุมสายโทรศัพท์สงขลา จังหวัดสงขลา

บริษัท ทีโอที จำกัด (มหาชน)
TOT PUBLIC COMPANY LIMITED

ส่วนออกแบบวิศวกรรมอาคาร ฝ่ายบริหารทรัพย์สิน

89/2 Moo 3 Cheangwattana Road, Thungsohong Laksi Bangkok 10210

89/2 หมู่ที่ 3 ถนนแจ้งวัฒนะ แขวงทุ่งสองห้อง เขตหลักสี่ กรุงเทพมหานคร 10210



งานจ้างเหมาก่อสร้างอาคารสถานีโครงข่ายเคเบิลใต้น้ำปากบารา อำเภอละงู จังหวัดสตูล และ
งานปรับปรุงอาคารชุมสายโทรศัพท์สงขลา จังหวัดสงขลา พร้อมงานระบบไฟฟ้าสำรอง
งานติดตั้งระบบปรับอากาศ และงานรื้อถอน

บริษัท ทีโอที จำกัด (มหาชน)
TOT PUBLIC COMPANY LIMITED

ส่วนออกแบบวิศวกรรมอาคาร ฝ่ายบริหารทรัพย์สิน

89/2 Moo 3 Cheangwattana Road. Thungsonghong Laksi Bangkok 10210

89/2 หมู่ที่ 3 ถนนแจ้งวัฒนะ แขวงทุ่งสองห้อง เขตหลักสี่ กรุงเทพมหานคร 10210

เจ้าของโครงการ ฝ่ายพัฒนาผลิตภัณฑ์ระหว่างประเทศ

2/358



งานจ้างเหมาก่อสร้างอาคารสถานีโครงข่ายเคเบิลใต้น้ำปากบารา อำเภอละงู จังหวัดสตูล และ
งานปรับปรุงอาคารชุมสายโทรศัพท์สงขลา จังหวัดสงขลา พร้อมงานระบบไฟฟ้าสำรอง
งานติดตั้งระบบปรับอากาศ และงานรื้อถอน

ประกอบด้วย

1. งานจ้างเหมาก่อสร้างอาคารสถานีโครงข่ายเคเบิลใต้น้ำปากบารา อำเภอละงู จังหวัดสตูล พร้อมงานระบบไฟฟ้าสำรอง งานติดตั้งระบบปรับอากาศ และงานรื้อถอน
2. งานจ้างเหมาปรับปรุงอาคารชุมสายโทรศัพท์สงขลา จังหวัดสงขลา พร้อมงานระบบไฟฟ้าสำรอง งานติดตั้งระบบปรับอากาศ และงานรื้อถอน
3. งานจ้างเหมาปรับปรุงสถานี ILA Site ที่ชุมสายโทรศัพท์สตูล จังหวัดสตูล พร้อมงานติดตั้งระบบปรับอากาศ และงานรื้อถอน
4. งานจ้างเหมาปรับปรุงสถานี ILA Site ที่ชุมสายโทรศัพท์ควนลัง จังหวัดสงขลา พร้อมงานติดตั้งระบบปรับอากาศ และงานรื้อถอน
5. งานจ้างเหมาปรับปรุงสถานี ILA Site ที่ชุมสายโทรศัพท์รัตภูมิ จังหวัดสงขลา พร้อมงานติดตั้งระบบปรับอากาศ และงานรื้อถอน
6. งานจ้างเหมาต่อเติมอาคารสถานีเคเบิลใต้น้ำภายในประเทศเดิม ชุมสายโทรศัพท์สงขลา จังหวัดสงขลา พร้อมงานติดตั้งระบบปรับอากาศ และงานรื้อถอน
7. งานจ้างเหมาย้ายเสา TOWER 3G ที่ชุมสายโทรศัพท์ปากบารา อำเภอละงู จังหวัดสตูล
8. งานจ้างเหมาย้ายตู้ MOBILE EXCHANGE ที่ชุมสายโทรศัพท์ปากบารา อำเภอละงู จังหวัดสตูล และจัดหาระบบสื่อสารสัญญาณ ที่ชุมสายโทรศัพท์สงขลา พร้อมย้ายอุปกรณ์ MICROWAVE ที่ชุมสายโทรศัพท์รัตภูมิ จังหวัดสงขลา

บริษัท ทีโอที จำกัด (มหาชน)
TOT PUBLIC COMPANY LIMITED

ส่วนออกแบบวิศวกรรมอาคาร ฝ่ายบริหารทรัพย์สิน

89/2 Moo 3 Cheangwattana Road, Thungsonghong Laksi Bangkok 10210

89/2 หมู่ที่ 3 ถนนแจ้งวัฒนะ แขวงทุ่งสองห้อง เขตหลักสี่ กรุงเทพมหานคร 10210

เจ้าของโครงการ ฝ่ายพัฒนาผลิตภัณฑ์ระหว่างประเทศ



1. งานจ้างเหมาก่อสร้างอาคารสถานีโครงข่ายเคเบิลใต้น้ำปากบารา
อำเภอละงู จังหวัดสตูล พร้อมงานระบบไฟฟ้าสำรอง งานติดตั้งระบบปรับอากาศและงานรื้อถอน
● งานด้านอาคาร

บริษัท ทีโอที จำกัด (มหาชน)
TOT PUBLIC COMPANY LIMITED

ส่วนออกแบบวิศวกรรมอาคาร ฝ่ายบริหารทรัพย์สิน
89/2 Moo 3 Cheangwattana Road Thungsonghong Laksi Bangkok 10210
89/2 หมู่ 3 ถนนแจ้งวัฒนะ แขวงทุ่งสองห้อง เขตหลักสี่ กรุงเทพมหานคร 10210

5/358


รายการประกอบแบบวัสดุ		รายการประกอบแบบวัสดุ	
วัสดุตกแต่งผิวพื้น		วัสดุตกแต่งผิวผนัง	
สัญลักษณ์	ความหมาย	สัญลักษณ์	ความหมาย
พ1	พื้น ค.ส.ล. ผิวเรียบ ปูกระเบื้องแกรนิตโต้ ชนิดผิวมัน ขนาด 0.60x0.60ม (ราคาไม่น้อยกว่า 300 บาท/ตร.ม.)	ผ1	ผนังก่ออิฐมวลเบาหนา 0.10ม ฉาบปูนเรียบ ทาสี ผนังภายในฉาบผิวเรียบ ผนังภายนอกเซาะร่อง กว้าง 1" ลึก 6มม.ตามแบบ
พ2	พื้น ค.ส.ล. ปูหินขัดสำเร็จรูป TERRAZZO TILE ขนาด 0.40x0.40 ม.ผิวเคลือบ WAX	ผ2	ผนังก่ออิฐมวลเบาหนา 0.20 ม ฉาบปูนเรียบ ทาสี ผนังภายในฉาบผิวเรียบ ผนังภายนอกเซาะร่อง กว้าง 1" ลึก 6มม.ตามแบบ
พ3	พื้น ค.ส.ล. ผิวเรียบขัดมัน ทำพื้นผิวระบบ EPOXY POLY URETHANE CONCRETE กำหนดสีภายหลัง	ผ3	ผนังก่ออิฐมวลเบาฉาบปูนเรียบ หนา 0.10–0.20ม ทาสี ผึงกฤษฎีงสแตนเลส V-CUT HAIRLINE TYPE ขนาด 4ซม. ตามแบบ
พ4	พื้น ค.ส.ล. ผิวเรียบขัดมัน ติดตั้งพื้นยก RAISED FLOOR ขนาด 0.60x0.60ม. สูง 0.60ม. รายละเอียดตามข้อกำหนด	ผ4	ผนัง ค.ส.ล. หนา 0.10ม ฉาบผิวเรียบ ทาสี ผนังภายในฉาบผิวเรียบ ผนังภายนอกเซาะร่อง กว้าง 1" ลึก 6มม.ตามแบบ
พ5	พื้น ค.ส.ล. ผิวเรียบขัดมัน ติดตั้ง RAMP ทางลาดเอียง โครงคร่าวเหล็กฉาก 1 1/2" x 1 1/2" ทาสีกันสนิม ทาทับด้วยสีน้ำมัน	ผ5	ผนังก่ออิฐมวลเบาหนา 0.10ม ฉาบปูนเรียบ ปูกระเบื้องแกรนิตโต้ ขนาด 0.30x0.60 ม
	อย่างน้อย 2 เทียว ปิดทับด้วยแผ่นสเมาร์ทบอร์ด หรือ วิก้าบอร์ด หนา 20 มม ไปด้วยแผ่นพื้นกระเบื้องยางผิวกันลื่น ชนิดม้วน	ผ6	ผนังยิปซัมบอร์ดหนา 15 มม ชนิดทนไฟกร2 ด้าน ฉาบรอยต่อระหว่างแผ่นเรียบทาสี โครงคร่าวเหล็กชุบสังกะสี ขนาด 9.4x300
	หนาอย่างน้อย 2.5มม. พร้อมปิดขอบโดยรอบ		หนา 0.55มม @ 0.60ม
พ6	พื้น ค.ส.ล. ผิวเรียบขัดมัน ปูกระเบื้องยางชนิดม้วน หนา 2.5 มม กำหนดสีและลายภายหลัง	ผ7	ผนังอลูมิเนียมคอมโพสิต สีเคลือบ PVDF COATING ความหนาไม่น้อยกว่า 4มม. โครงคร่าวเหล็กทาสีกันสนิม
พ7	พื้น ค.ส.ล. ผิวเรียบ ปูกระเบื้องแกรนิตโต้ ชนิดผิวหยาบ ขนาด 0.30x0.60ม	ผ8	ผนังก่ออิฐมวลเบาฉาบปูนเรียบทำผิวกรวดล้างเซาะร่อง กว้าง 1" ความลึกร่อง 6มม. ตามแบบ
พ8	พื้น ค.ส.ล. ผสมน้ำยากันซึมผิวเรียบ ติดตั้งระบบกันซึม BUILT UP ROOFและกันความร้อน	ผ9	ผนังก่ออิฐมวลเบาฉาบปูน กรุแผ่นเซลโลกริตขนาด 0.60x1.20ม.หนา 20มม. ทำสีพื้น เว้นร่อง PVC. 15มม. โครงคร่าวเหล็กชุบสังกะสี
พ9	พื้น ค.ส.ล. ผิวเรียบทำผิวขัดมัน	ผ10	ผนัง CURTAIN WALL กรอบอลูมิเนียม กระจกตัดแสงสีเขียวหนา 9 มม.
พ10	พื้น ค.ส.ล. ผิวกรวดล้าง เซาะร่องลายก้างปลา ขนาดร่องกว้าง 1" ลึก 1ซม. ระยะห่างร่อง 0.15ม.	ผ11	ผนัง ค.ส.ล. ฉาบปูนเรียบทาสี
พ11	พื้น ค.ส.ล. ผสมน้ำยากันซึมทำผิวเรียบขัดมัน	ผ12	ผนังตกแต่ง ห้องทำงานและห้องประชุม ดูแบบขยาย A-39
พ12	พื้น ค.ส.ล. ผิวขัดหยาบเรียบ		
พ13	พื้น ทราฮายาบบดอัดแน่น ปรับพื้นผิวคอนกรีตหยาบ ปูทับด้วยพื้นทางเท้า CPAC BLOCK ติดตั้งตามกรรมวิธีบริษัทผู้ผลิต	หมายเหตุ	
		บัวเชิงผนังอลูมิเนียม สูง 4" x1/2" ยึดด้วยสกรูพร้อมยางปิดขอบ ผลิตภัณฑ์ ของ INFINITE ,APACE หรือเทียบเท่า	
			</

รายละเอียด ขอบเขตของงาน



รายละเอียดและคุณสมบัติพื้น RAISED FLOOR

ขอบเขตของงานจ้างเหมาก่อสร้างอาคารสถานีโครงข่ายเคเบิลใต้น้ำ ปากบารา อ.ละงู จ.สตูล พร้อมงานติดตั้งระบบปรับอากาศและงานรื้อถอน			แผ่นพื้น
1. ผู้รับจ้างดำเนินการก่อสร้างอาคาร งานบริเวณและงานระบบส่วนประกอบอาคารต่างๆ คือ			- แผ่นพื้นต้องมีขนาด 600x600x35 มม. ทำจากเหล็ก โดยโครงสร้างของแผ่นพื้นประกอบด้วยเหล็กแผ่นบนและแผ่นล่าง ซึ่งแผ่นล่างถูกขึ้นรูปโดมทั้งหมด 64 โดม เหล็กแผ่นบนและแผ่นล่างถูกเชื่อมติดกันที่ขอบของแผ่นและปลายโดม เพื่อต้านการยุบตัวทุกๆจุดบนแผ่น แผ่นพื้นต้องบรรจุด้วยคอนกรีตชนิดน้ำหนักเบาเพื่อเพิ่มคุณสมบัติการรับน้ำหนัก - แผ่นพื้นต้องมีการป้องกันสนิม โดยด้านในของแผ่นเคลือบด้วยฟอสเฟต (PHOSPHATE COATING) และด้านนอกพ่นเคลือบด้วยสีอีพ็อกซี (ELECTRO-STATICALLY EPOXY POWER COATED PAINTWORK)
1.1 งานถมดินปรับพื้นที่ที่ก่อสร้างให้ไ้ระดับตามที่ระบุในแบบ			
1.2 งานก่อสร้างรั้วโดยรอบ พร้อมก่อสร้างป้ายด้านหน้า ให้เป็นไปตามแบบรูปและรายการละเอียดตามข้อกำหนด			
1.3 ก่อสร้างอาคารสถานีโครงข่ายเคเบิลใต้น้ำ เป็นอาคารคอนกรีตเสริมเหล็ก 4 ชั้น ตามแบบรูปและรายการละเอียด ตามข้อกำหนด			
1.4 งานติดตั้งระบบส่วนประกอบอาคารระบบต่างๆ ให้เป็นไปตามแบบรูปและรายการละเอียดข้อกำหนด ได้แก่			
1.4.1 งานระบบโครงสร้างอาคาร ตามแบบรูปและรายการละเอียดข้อกำหนด			
1.4.2 งานระบบไฟฟ้า ไฟฟ้ากำลัง (GENERATOR) และเครื่องสำรองไฟฟ้า(UPS) ตามแบบรูปและรายการละเอียดข้อกำหนด			
1.4.3 งานระบบสัญญาณเตือนอัคคีภัย ตามแบบรูปและรายการละเอียดข้อกำหนด			
1.4.4 งานระบบดับเพลิงอัตโนมัติ ตามแบบรูปและรายการละเอียดข้อกำหนด			
1.4.5 งานระบบควบคุมการเข้า-ออกอาคาร (ACCESS CONTROL) ตามแบบรูปและรายการละเอียดข้อกำหนด			
1.4.6 งานระบบบริหารจัดการอาคาร (BMS) ตามแบบรูปและรายการละเอียดข้อกำหนด			วัสดุปิดผิว - ผิวหน้าด้านบนของแผ่นพื้น ต้องปิดด้วยแผ่นลามิเนต (HPL) โดยวัสดุปิดผิวต้องมีคุณสมบัติเป็นชนิด ANTI-STATIC โดยมีค่าความต้านทานที่ผิวอยู่ในช่วง $1 \times 10^5 - 1 \times 10^9$ โอห์ม - ขอบทุกด้านของแผ่นพื้นต้องปิดด้วย PVC EDGE TRIM
1.4.7 งานระบบโทรทัศน์วงจรปิด ตามแบบรูปและรายการละเอียดข้อกำหนด			
1.4.8 งานระบบปรับอากาศ และระบายอากาศ ตามแบบรูปและรายการละเอียดข้อกำหนด			
1.4.8 งานก่อสร้างพร้อมติดตั้งเสา รับ ส่ง สัญญาณระบบ 3G ตามแบบรูปและรายการละเอียดข้อกำหนด			
1.4.9 งานบริเวณอื่นๆได้แก่ ถนน ที่จอดรถ ทางเท้าโดยรอบอาคาร และป้ายรั้ว ตามแบบรูปและรายการละเอียดข้อกำหนด			
1.4.10 งานอื่นๆ ตามแบบรูปและรายการละเอียดข้อกำหนด			ระบบขาตั้ง - เสาต้องทำจากเหล็กกล่องสี่เหลี่ยม มีความสูง 60CM.(จากฐานถึงผิวหน้า)ตามที่กำหนดในรายการยกพื้นRAISED FLOOR ฐานมีขนาด 4"x4"ยึดติดกับพื้นคอนกรีตโดยใช้กาว (ADHESIVE) - หัวเสาต้องทำจากเหล็กกล่องสี่เหลี่ยม ประกอบด้วยส่วนที่เป็นเกลียวและน็อต สามารถปรับระดับที่น็อตขึ้นลงได้ในแกน ± 25 มม. - คานต้องทำจากเหล็กกล่องสี่เหลี่ยม คานยึดกับหัวเสาโดยใช้สกรู (BOLTED STRINGER) - ระบบขาตั้งต้องรับแรงในแนวตั้ง (AXIAL LOAD) ได้ไม่น้อยกว่า 22.5 KN.
2.1. พื้น			
- ติดตั้งยกพื้น RAISED FLOOR ในบริเวณที่กำหนดตามแบบรูป รายละเอียดและข้อกำหนด			
- จัดทำและติดตั้ง .AMP ตามแบบรูป รายละเอียดและข้อกำหนด			
- ห้อง AAE-1 ห้อง IIG และห้อง Collocation บริเวณพื้นที่ห้องและผนังใต้พื้นยก RAISED FLOOR ให้บุห้บและบุด้วยฉนวนกันความร้อนชนิด FLEXIBLE CLOSED CELL ELASTOMERIC THERMAL INSULATION หรือชนิด CLOSED CELL GRAY POLYETHYLEN FORM หนา 1"พร้อมหุ้มขาตั้งแผ่นพื้นยกยกระดับ			
- ติดตั้งบันไดโครงเหล็กจาก 1 1/2"x1 1/2"๑0.40 ม ทาสีกันสนิม ปิดทับด้วยแผ่น SMART BOARD หรือ VIVA BOARD ความหนาไม่น้อยกว่า 20 มม บุกระเบื้องยางหนา 2.5 มม จมูกบันไดอลูมิเนียมพร้อมยางกันลื่น			การรับน้ำหนัก ระบบพื้นยกจะต้องรับน้ำหนักได้ดังนี้ - CONCENTRATED LOAD : 570 KG./ตารางนิ้ว - UNFORM LOAD : 3370 KG./ตารางเมตร - ULTIMATE LOAD : 1710 KG./ตารางเมตร - ROLLING LOAD : 454 KG.
2.2. ผนัง			
- ให้ติดตั้งบัวเชิงผนังอลูมิเนียมชนิดความสูง 4" ยึดด้วยสกรูพร้อมยางปิดขอบ ผลิตภัณฑ์ ของ APACE, INFINITEหรือเทียบเท่า			
ภายในห้อง OFFICE ,CONFERENCES, BMS CONTROL, LOBBY, COLOCATION, IIG, TRANSMISSION, AAE-1CLS, CORRIDOR ชั้น 1 2 และ3			
2. งานครุภัณฑ์			
- จัดหาตู้เก็บอุปกรณ์เคเบิลใต้น้ำ จำนวน 6 ตู้ - จัดหาตู้เก็บเอกสาร จำนวน 6 ตู้			RAMP ทำจากโครงเหล็กจาก 1 1/2"x1 1/2"ทาสีกันสนิม ปิดทับด้วยแผ่นSMART BOARDหรือVIVA BOAEDหนา 20 มม. และปิดทับด้วยแผ่นยางปูมกันลื่น มาตรฐาน - การทดสอบการรับน้ำหนักของระบบพื้นยกต้องเป็นไปตามมาตรฐาน CISCA-USA STANDARDS - โรงงานผู้ผลิตต้องได้คุณภาพมาตรฐานสากล - ผลิตภัณฑ์ห่อ PEC,BSP,PP,JUL หรือ เทียบเท่า - จัดหาอุปกรณ์สำหรับยกพื้น (PANEL LIFTER) จำนวน 2 ชุด - สำหรับห้อง COLLOCATION(1)ห้อง IIG และ AAE-1 ให้จัดหาแผ่นระบายอากาศ (PERFORATED PANEL) ชนิดมี VOLUMETRIC DAMPER จำนวน 25% ของพื้นที่ห้อง
- จัดหาโต๊ะทำงานพร้อมเก้าอี้พนักงาน จำนวน 6 ชุด			
- จัดหาโต๊ะประชุม จำนวน 1 ตัว			
- จัดหาเก้าอี้พนักงานกลางและมีเท้าแขน จำนวน 6 ตัว			
3. จัดทำแผ่นป้ายชื่อห้องต่างๆ บริเวณหน้าห้อง แผ่นป้ายอลูมิเนียมหนา3มม. ตัวหนังสือ PVC สีขาวด้าน ความสูง 8 ซม. FRONTแบบ PSL KITTITHADAรูปแบบกำหนดภายหลัง			
4. งานรื้อถอน เสาสัญญาณโทรศัพท์ 3G และ ตู้ MOBILE ชุมสายโทรศัพท์ปากบารา วัสดุรื้อถอนส่งคืน บริษัท ทีโอที จำกัด(มหาชน)			
5. ผู้รับจ้างจะต้องทำงานทั้งหมดแล้วเสร็จภายใน 360 วัน นับถัดจากวันลงนาม ในสัญญาโดย บมจ.ทีโอที จ่ายเงินเป็นงวด จำนวน 9 งวด			

 Property Management Department ฝ่ายบริหารทรัพย์สิน ส่วนอำนวยการวิศวกรรมอาคาร	เจ้าของโครงการ	ฝ่ายพัฒนาผลิตภัณฑ์ระหว่างประเทศ	สถาปนิก	สนั่น นาคนิกร ภ-สธ9619	วิศวกรระบบไฟฟ้ากำลัง เอลิมชัย พฤตชากร ภพท 6625 จิระชาย เวชวิสุทธิคุณ ภพท 19309	วิศวกรระบบป้องกันอัคคีภัย ประทีป อินทรศักดิ์ ภพส 6707	ตรวจ	วิเชษฐพงศ์ พิตยามาต 18/04/57	เลขที่แบบ	A-03
	แบบ	งานจ้างเหมาก่อสร้างอาคารสถานีโครงข่ายเคเบิลใต้น้ำ ปากบารา อ.ละงู จ.สตูล พร้อมงานติดตั้งระบบปรับอากาศ และงานรื้อถอน	วิศวกรโครงสร้าง	เอกสิทธิ์ จิงขจรเกียรติ สย5778	วิศวกรระบบควบคุมอัตโนมัติ พงษ์ศักดิ์ บุญทวี ภพท5874	วิศวกรระบบดับเพลิงอัตโนมัติ ปรีชา เหมมัน สก3014	เห็นชอบ	พิระ มาประเสริฐ 26/05/57	แผ่นที่/รวม	
	แสดง	รายละเอียด ขอบเขตของงาน	มาตราส่วน				อนุมัติ	ชูชาติ ช่วยชู 27/05/57		
		รายละเอียดและคุณสมบัติพื้นRAISED FLOOR	เขียน	สิงห์ อาษา	วิศวกรระบบสุขาภิบาล เอลิมพล อุดลย์นร ภย 21035	วิศวกรระบบสื่อสารสัญญาณ ปานทิพย์ พูนผล	วิศวกรระบบปรับอากาศ สุมิตร ศรีวิพัฒน์ ภท10666	ผจก.ทพ. 27/05/57		

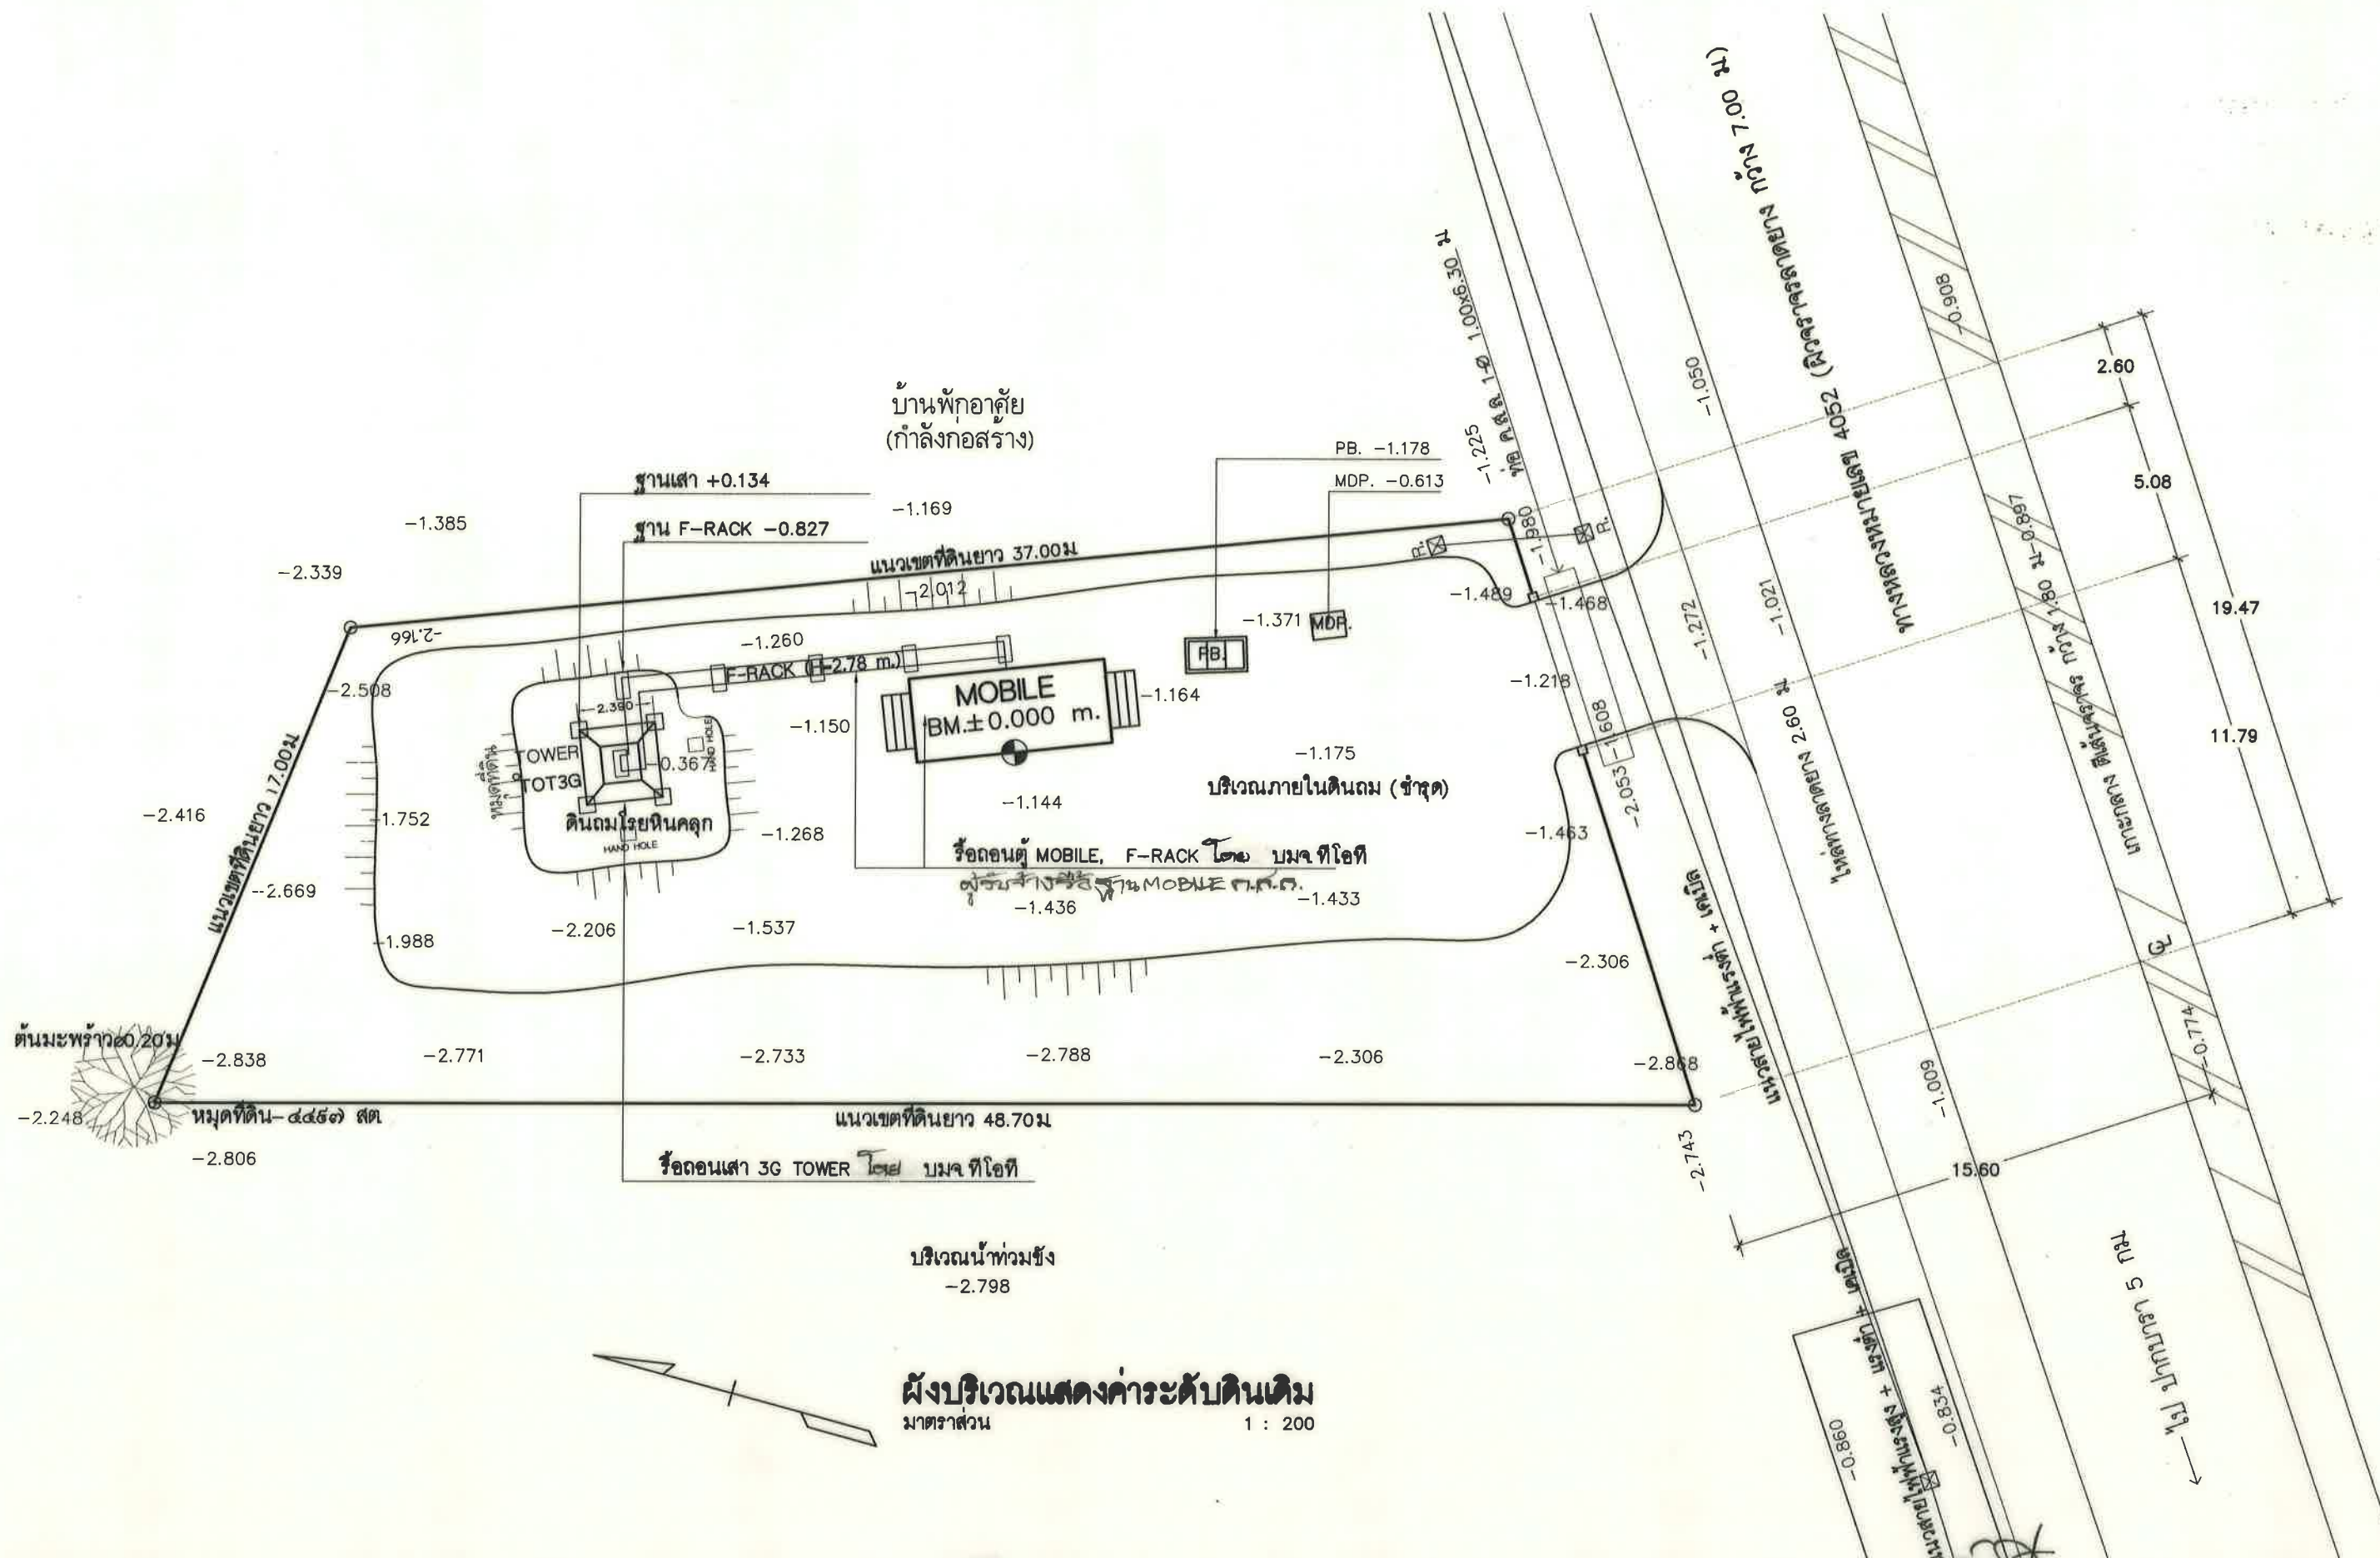

 Property Management Department ฝ่ายบริหารทรัพย์สิน ส่วนออกแบบวิศวกรรมอาคาร	เจ้าของโครงการ	ฝ่ายพัฒนาผลิตภัณฑ์ระหว่างประเทศ	สถาปนิก	สนั่น นาคนิกร ภา-สถ.9619	วิศวกรระบบไฟฟ้ากำลัง	เฉลิมชัย พงษ์พานิช ภาฟก 6625	วิศวกรระบบป้องกันอัคคีภัย	ประทีป อินทพรศักดิ์ ภาฟค 6707	ตรวจ	วิรัชพงศ์ ศิพยานนท์ ภาฟค 18/4/57	เลขที่แบบ
	แบบ	งานจ้างเหมาก่อสร้างอาคารสถานีโครงข่ายเคเบิลใยแก้ว ปากบารา อ.ละงู จ.สตูล พร้อมงานติดตั้งระบบปรับอากาศ และงานรื้อถอน	วิศวกรโครงสร้าง	เอกสิทธิ์ จิงจางเกียรติ สย.5778	วิศวกรระบบควบคุมอัตโนมัติ	พงษ์ศักดิ์ บุญทวี ภาฟก 5874	วิศวกรระบบดับเพลิงอัตโนมัติ	ปรีชา เหมสันต์ สก.3014	เห็นชอบ	ศิระ มาประเสริฐ 26/4/57	A-04
	แสดง	มาตราส่วน 1 : 200	วิศวกรระบบสุขาภิบาล	เฉลิมพล อุดมย์บุตร ภาข. 21035	วิศวกรระบบสื่อสารสัญญาณ	ปานทิพย์ ขุนผล	วิศวกรระบบปรับอากาศ	สุมิตร ศรีวิวัฒน์ ภาท.10666	อนุมัติ	รุชติ ราษฎร์ 27/4/57	แผ่นที่/รวม
	ผังบริเวณแสดงค่าระดับดินเดิม	เขียน	สนั่น นาคนิกร								4/49

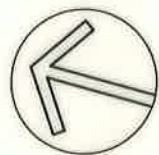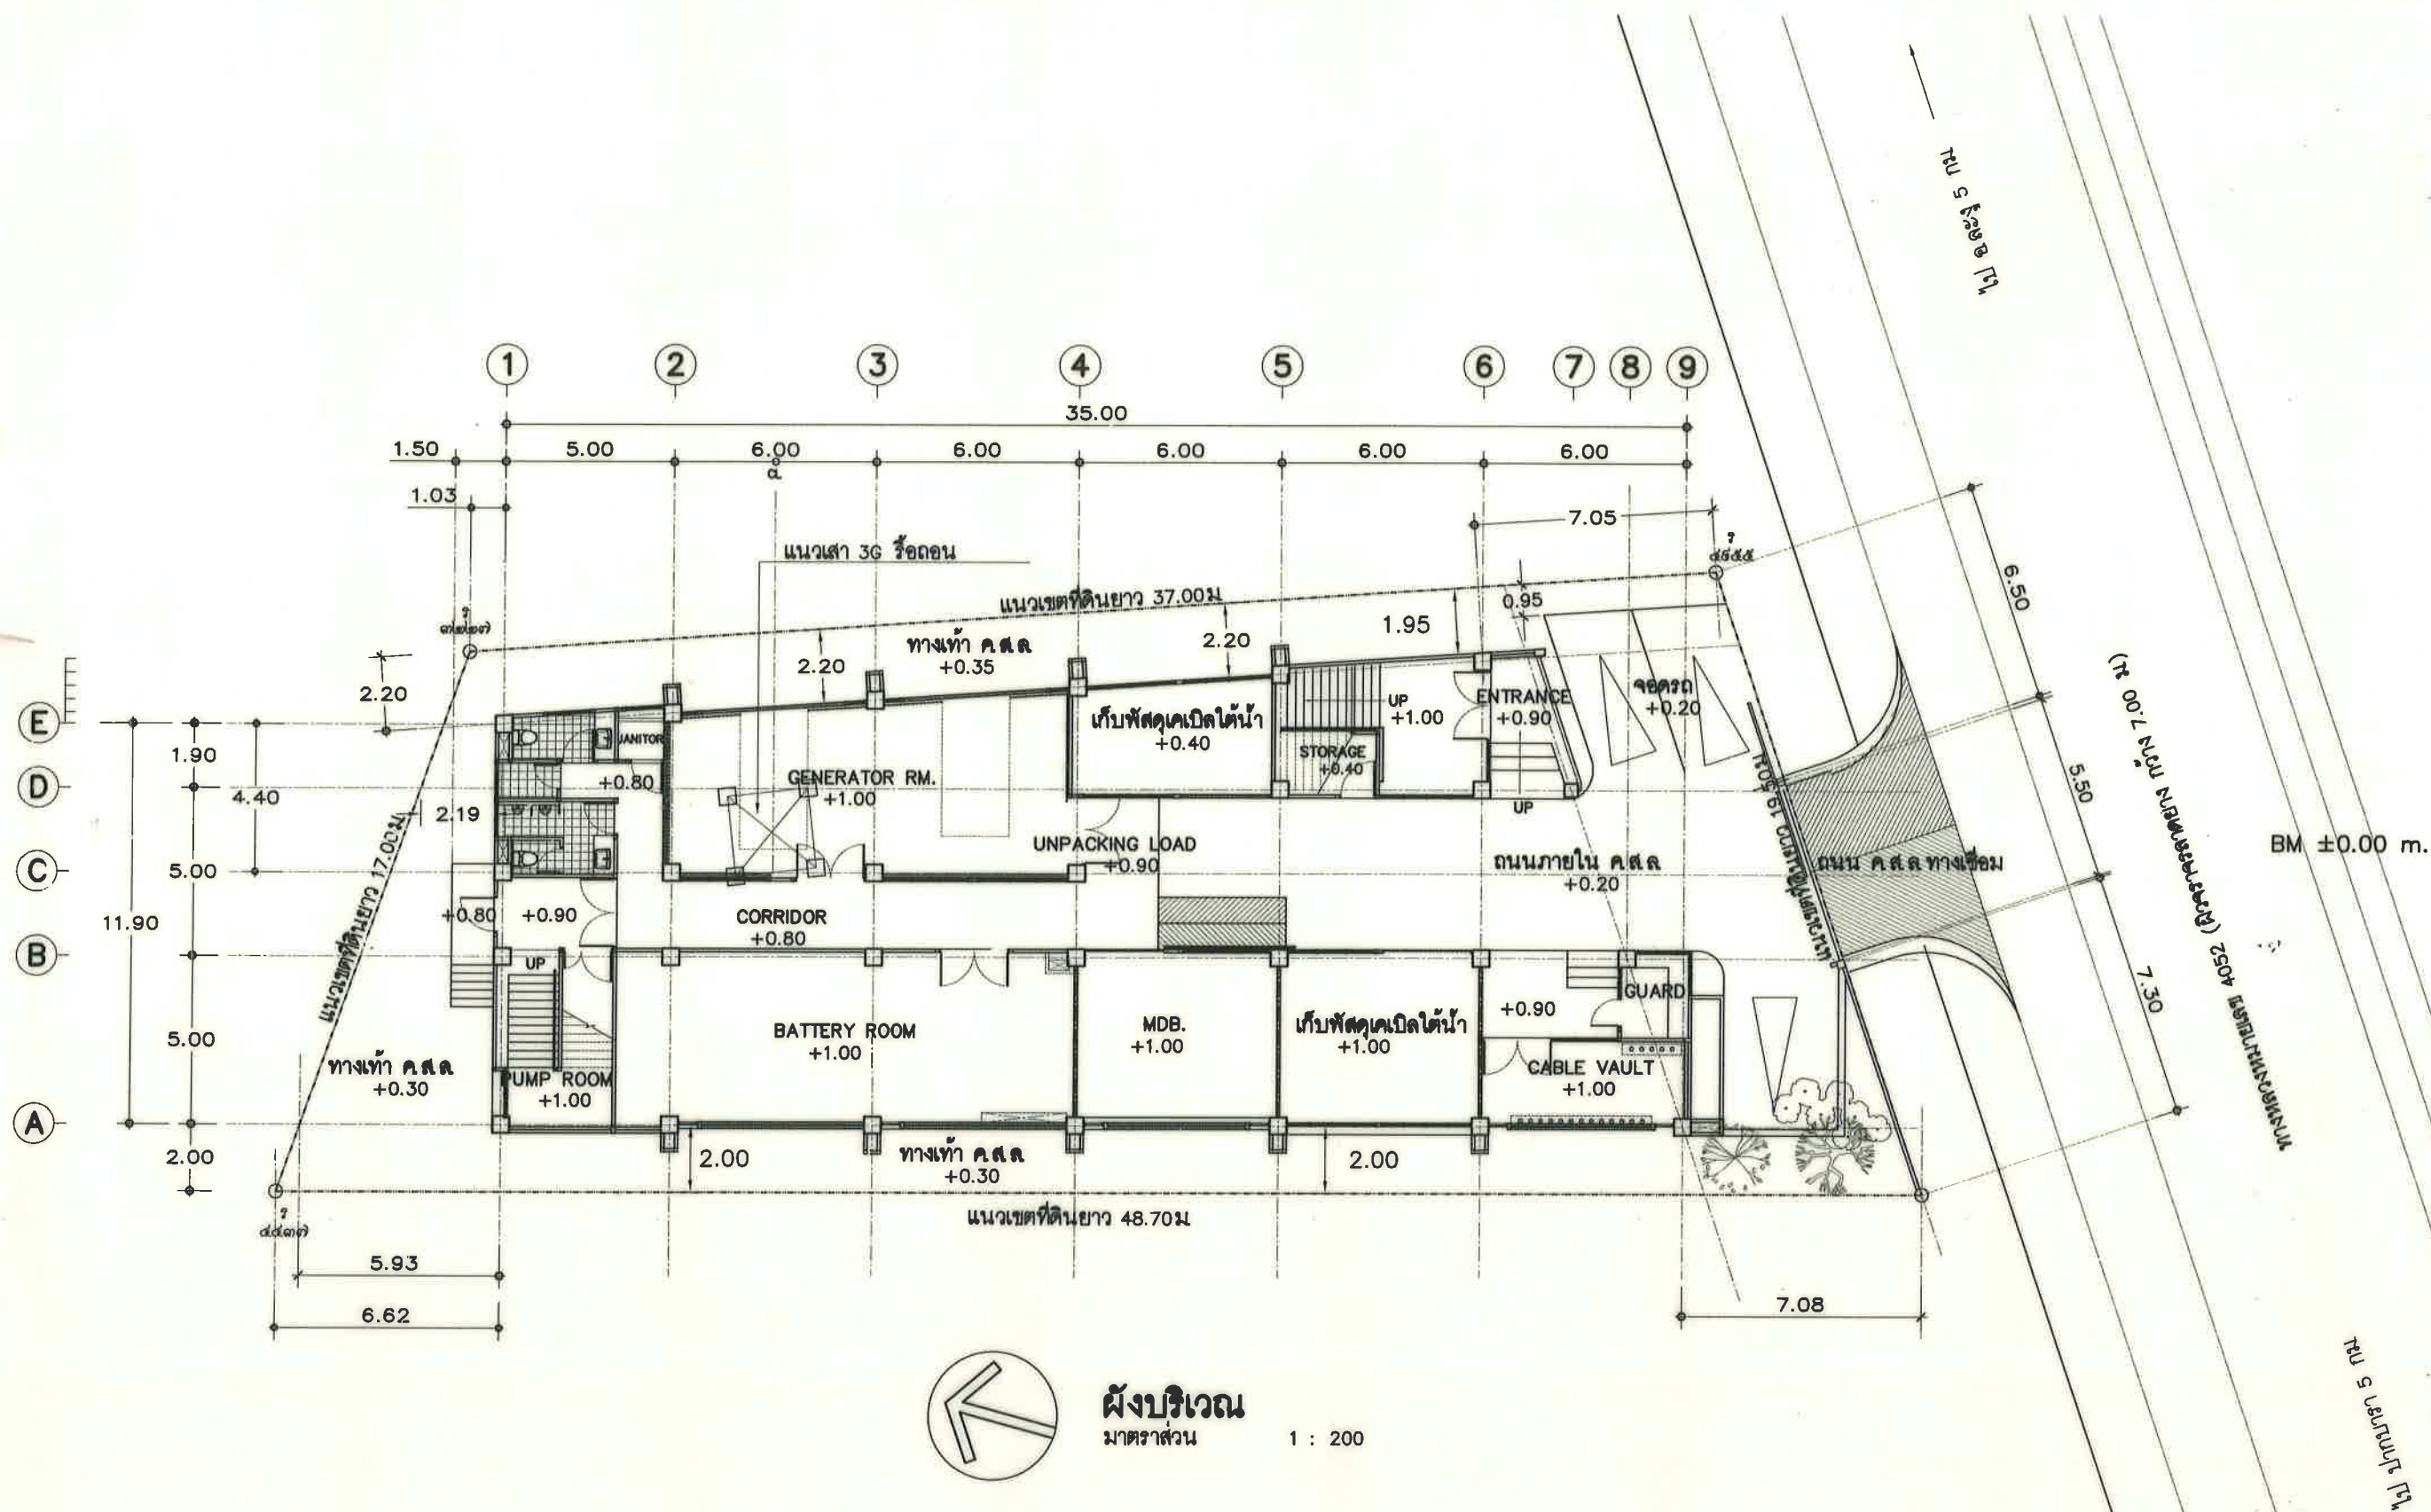


ผังบริเวณ
มาตราส่วน

1 : 200


 Property Management Department ฝ่ายบริหารทรัพย์สิน ส่วนออกแบบวิศวกรรมอาคาร	เจ้าของโครงการ	ฝ่ายพัฒนาผลิตภัณฑ์ระหว่างประเทศ	สถาปนิก	สนั่น นาคนิกร ภาท 6625	วิศวกรระบบไฟฟ้ากำลัง	เฉลิมชัย พงษ์พานิช ภาท 6625	วิศวกรระบบป้องกันอัคคีภัย	ประทีป อินทศักดิ์ ภาท 6707	ตรวจ	วิมลพร ภาท 6707	ผจ.สอทพ.	เลขที่แบบ
	แบบ	งานจ้างเหมาก่อสร้างอาคารตามโครงการขยายเคเบิลทีวี ปากบารา	วิศวกรโครงสร้าง	เอกสิทธิ์ จิระชัยเกียรติ สข 5778	วิศวกรระบบควบคุมอัตโนมัติ	พงษ์ศักดิ์ บุญทวี ภาท 5874	วิศวกรระบบดับเพลิงอัตโนมัติ	ปรีชา เหมฝัน สก 3014	เห็นชอบ	วิมลพร ภาท 6707	ผจ.สอทพ.	A-05
	แสดง	อ.และร. จ.สต. พร้อมงานติดตั้งระบบปรับอากาศ และงานรื้อถอน	วิศวกรระบบสุขาภิบาล	เฉลิมพล อุดมย์บุตร ภาท 21035	วิศวกรระบบสื่อสาร	ปานทิพย์ พูนผล	วิศวกรระบบปรับอากาศ	สุมิตร ศรีวิวัฒน์ ภาท 10666	อนุมัติ	วิมลพร ภาท 6707	ผจ.สอทพ.	แผ่นที่/รวม
	ผังบริเวณ	มาตราส่วน 1 : 200	เขียน	สนั่น นาคนิกร					อนุมัติ	วิมลพร ภาท 6707	ผจ.สอทพ.	5/49

9/358

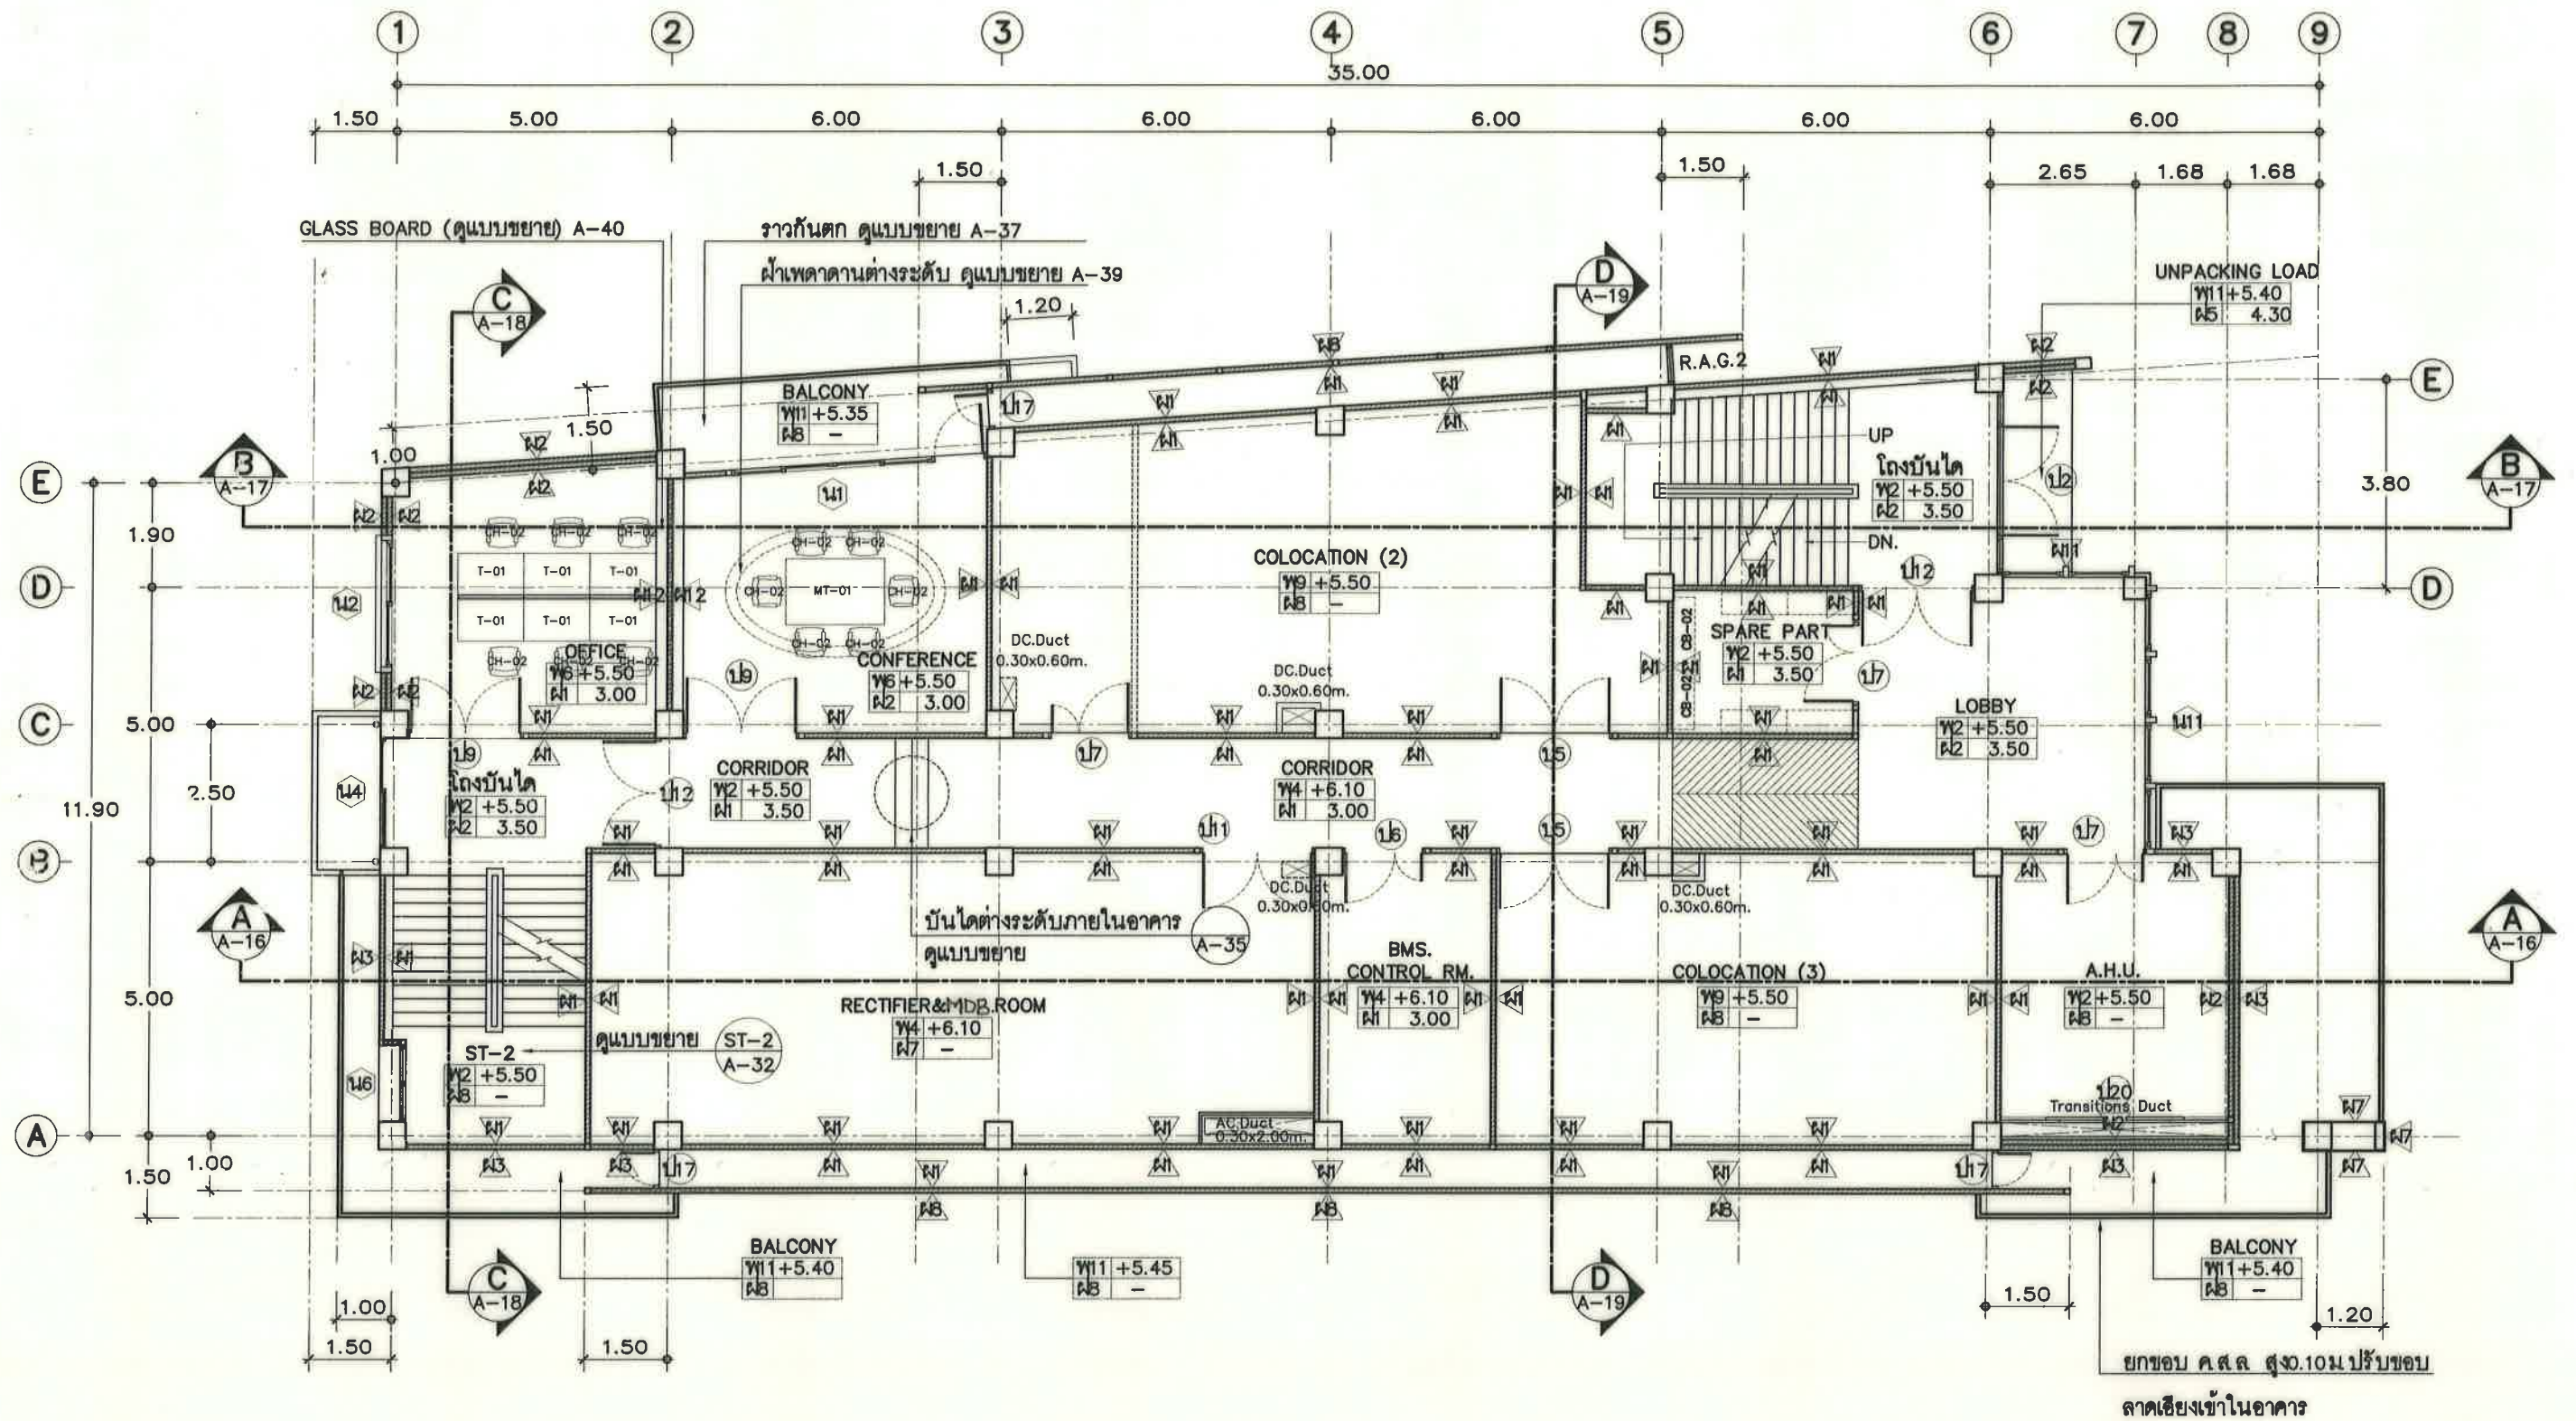


แปลนพื้นที่ 2
มาตราส่วน 1 : 125

 Property Management Department ฝ่ายบริหารทรัพย์สิน ส่วนอาคารและวิศวกรรมอาคาร	เจ้าของโครงการ	ฝ่ายพัฒนาผลิตภัณฑ์ระหว่างประเทศ	สถาปนิก	สนั่น นาคนิกร ก-สถ.9619	วิศวกรระบบไฟฟ้ากำลัง	เฉลิมชัย พุกขาวกร ภพท. 6625 จิระชัย เวชวิสุทธิคุณ ภพท. 19309	วิศวกรระบบป้องกันอัคคีภัย	ประทีป อินทรศักดิ์ ภพท. 6707	ตรวจ	วิรัชพงศ์ พิทยานามะ 26.05.52	เลขที่แบบ	A-07
	แบบ	งานจ้างเหมาก่อสร้างอาคารสถานีโครงการเคเบิลทีวี ปากบารา อลงกรณ์ จ.สตูล พร้อมงานติดตั้งระบบปรับอากาศ และงานรื้อถอน	วิศวกรโครงสร้าง	เอกสิทธิ์ จิงขจรเกียรติ สย.5778	วิศวกรระบบควบคุมอัตโนมัติ	พงษ์ศักดิ์ บุญทวี ภพท. 5874	วิศวกรระบบดับเพลิงอัตโนมัติ	ปรีชา เหมพันธ์ สท.3014	เห็นชอบ	ศิระ มาประเสริฐ 26.06.52	แผ่นที่/รวม	7/49
	แสดง	แปลนพื้นที่ 2	มาตราส่วน	1 : 125	วิศวกรระบบสุขาภิบาล	เฉลิมพล อุดยัมตร ภย. 21035	วิศวกรระบบปรับอากาศ	สุมิตร ศรีวิวัฒน์ ภท. 10666	อนุมัติ	สุชาติ ชัยสุข 27.06.52		
			เขียน	สิงห์ ธาษา								

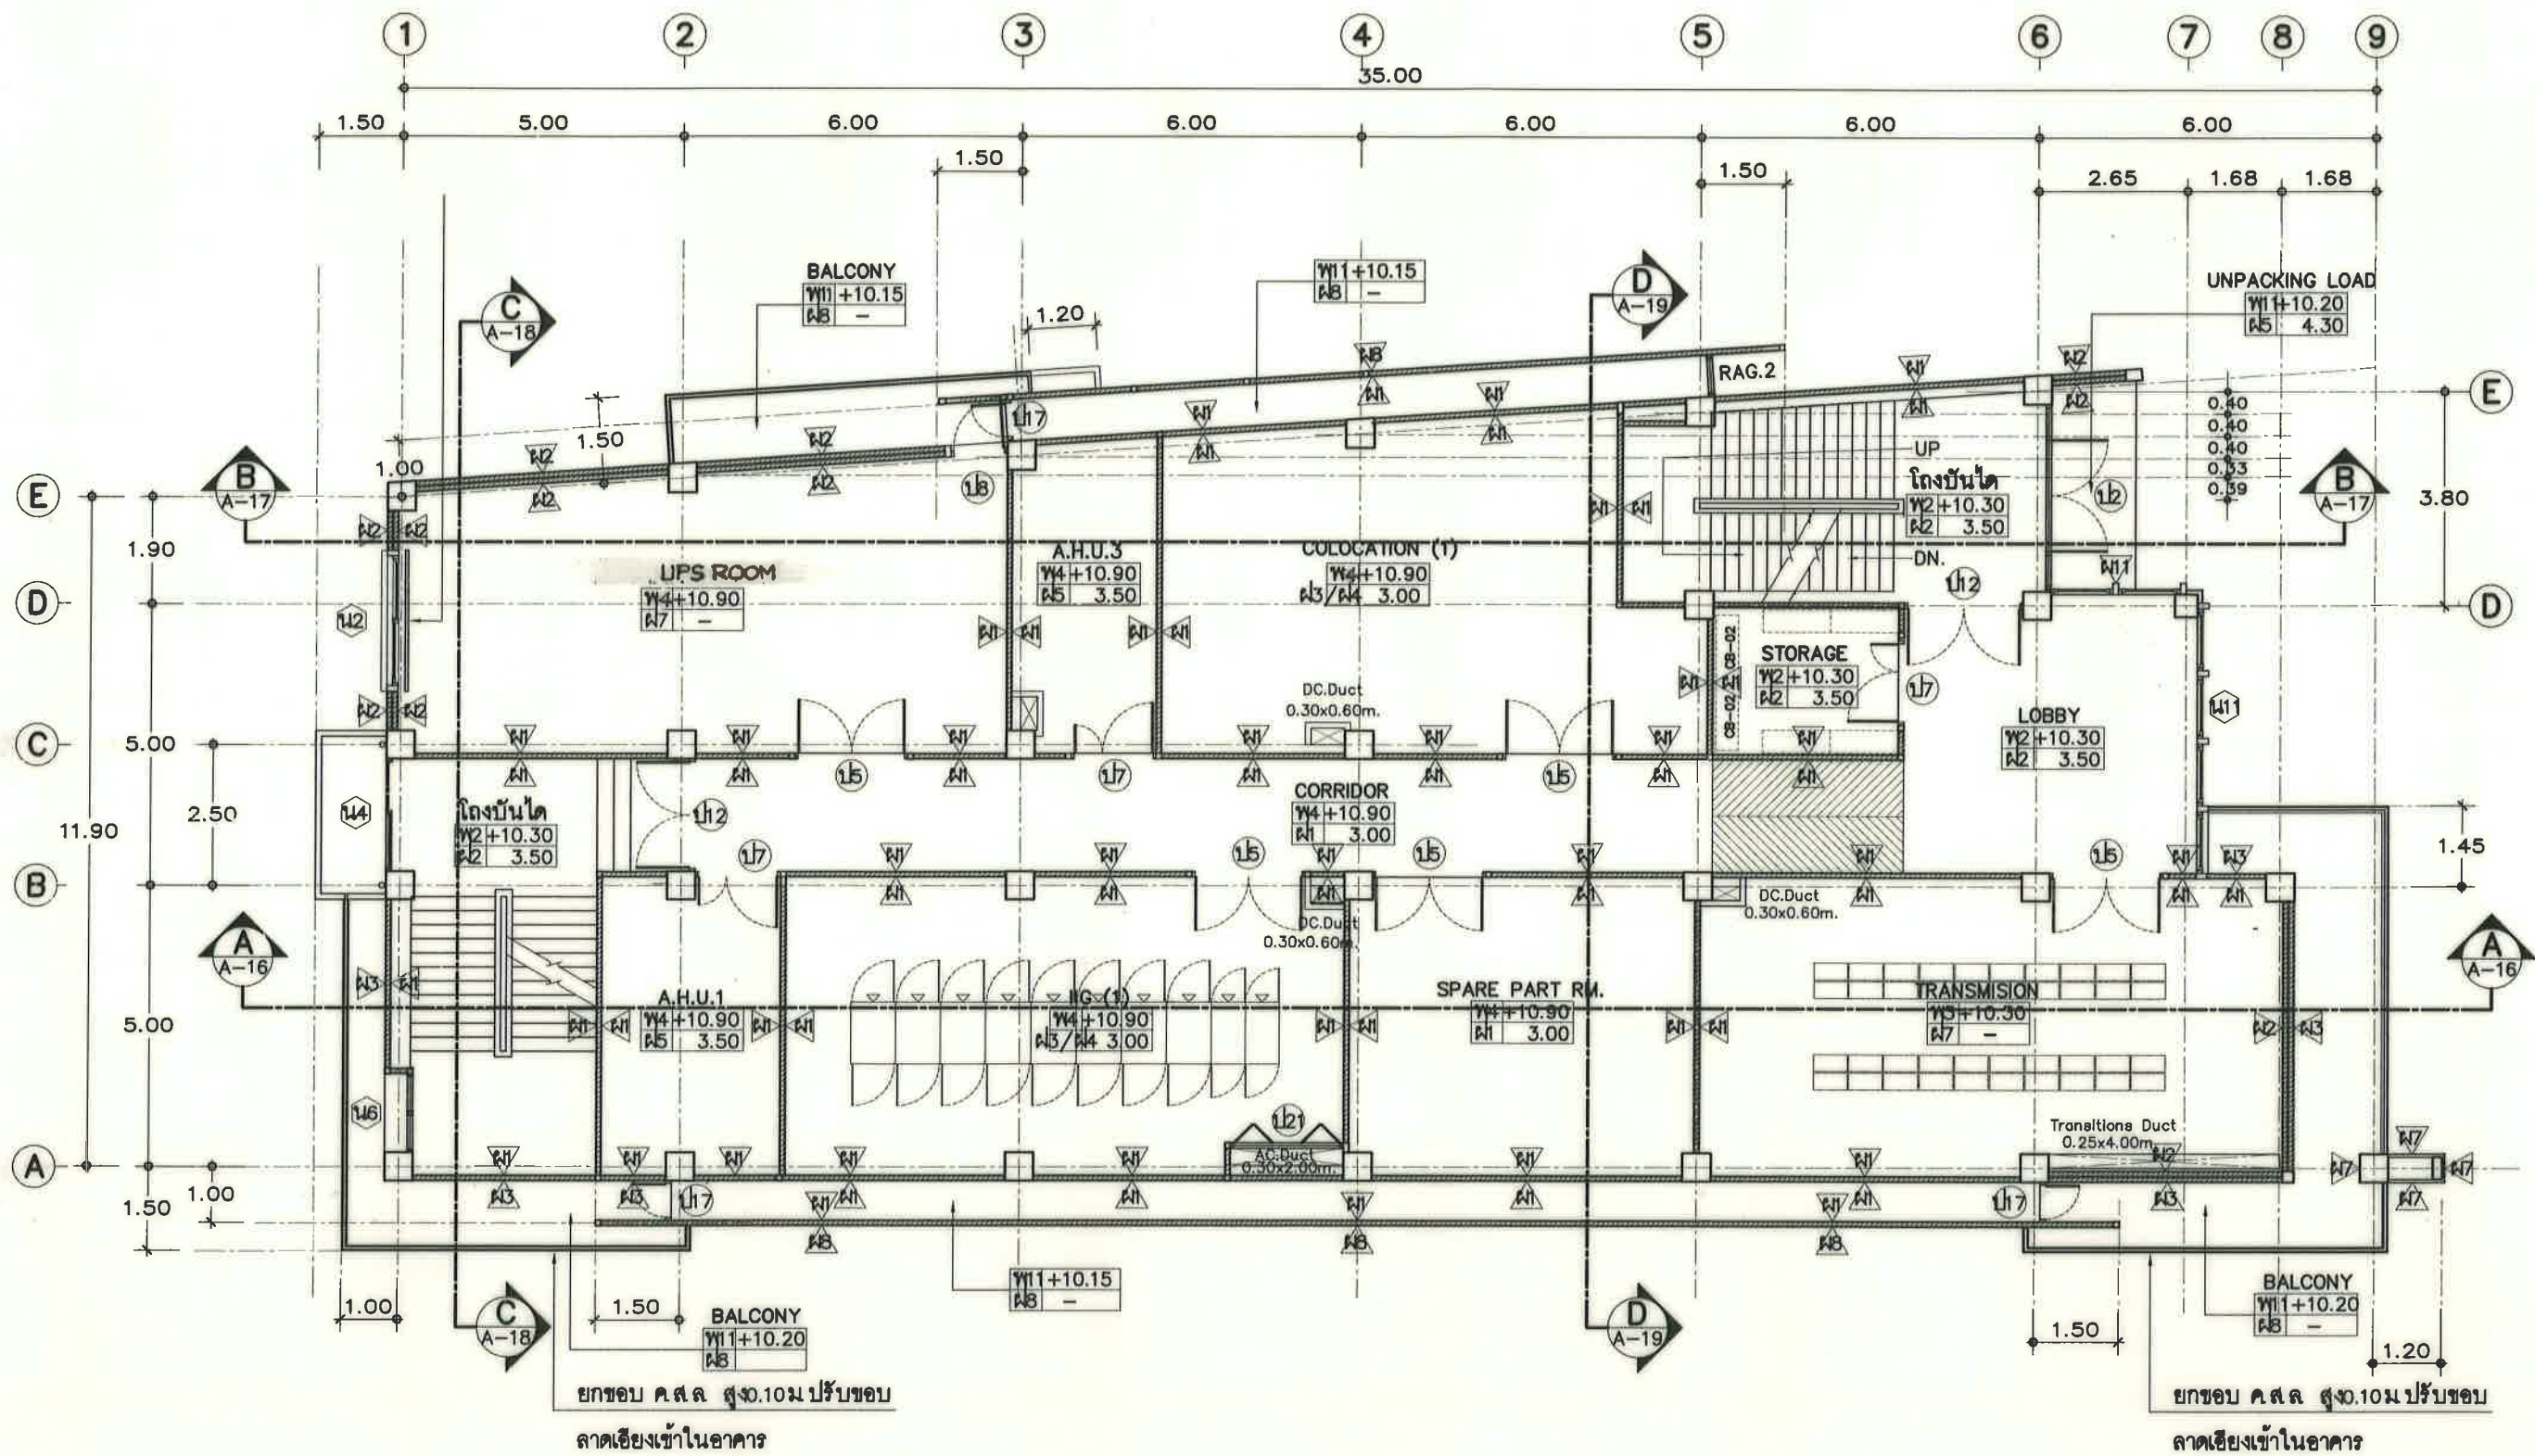


แปลนพื้นที่ 3
มาตราส่วน 1 : 125

 Property Management Department ฝ่ายบริหารทรัพย์สิน ส่วนอาคารและวิศวกรรมอาคาร	เจ้าของโครงการ	ฝ่ายพัฒนาผลิตภัณฑ์ระหว่างประเทศ	สถาปนิก	สนั่น นาคนิกร ภา-สถ.9619	วิศวกรระบบไฟฟ้ากำลัง	เฉลิมชัย พงษ์พานิช ภาทศ. 6625	วิศวกรระบบป้องกันอัคคีภัย	ประทีป อินทรพิทักษ์ ภาทศ. 6707	ตรวจ	วิมลพร วัฒนวิทย์ 16/04/57	ผจ.สอ.ทพ.	เลขที่แบบ
	แบบ	งานจ้างเหมาก่อสร้างอาคารสถานที่โครงการขายเคเบิลทีวี ปากบารา	วิศวกรโครงสร้าง	เอกสิทธิ์ จันทระเกียรติ สย.5778	วิศวกรระบบควบคุมอัตโนมัติ	จิระชาย เวชวิสุทธิคุณ ภาทศ. 19309	วิศวกรระบบดับเพลิงอัตโนมัติ	ปรีชา เหมพันธ์ สก.3014	เห็นชอบ	อ.อ.ทพ.	ผจ.สอ.ทพ.	A-08
	แสดง	อ.ละงู จ.สตูล พร้อมงานติดตั้งระบบปรับอากาศ และงานรื้อถอน	วิศวกรระบบสุขาภิบาล	เฉลิมพล อุดมย์นคร ภา. 21035	วิศวกรระบบสื่อสารสัญญาณ	พงษ์ศักดิ์ บุญทวี ภาทศ. 5874	วิศวกรระบบปรับอากาศ	สุวิตร ศรีพิพัฒน์ ภาทศ. 10666	อนุมัติ	อ.อ.ทพ.	ผจ.สอ.ทพ.	แผ่นที่/รวม
		แปลนพื้นที่ 3	เขียน	สนั่น นาคนิกร						อ.อ.ทพ.	ผจ.สอ.ทพ.	8/49

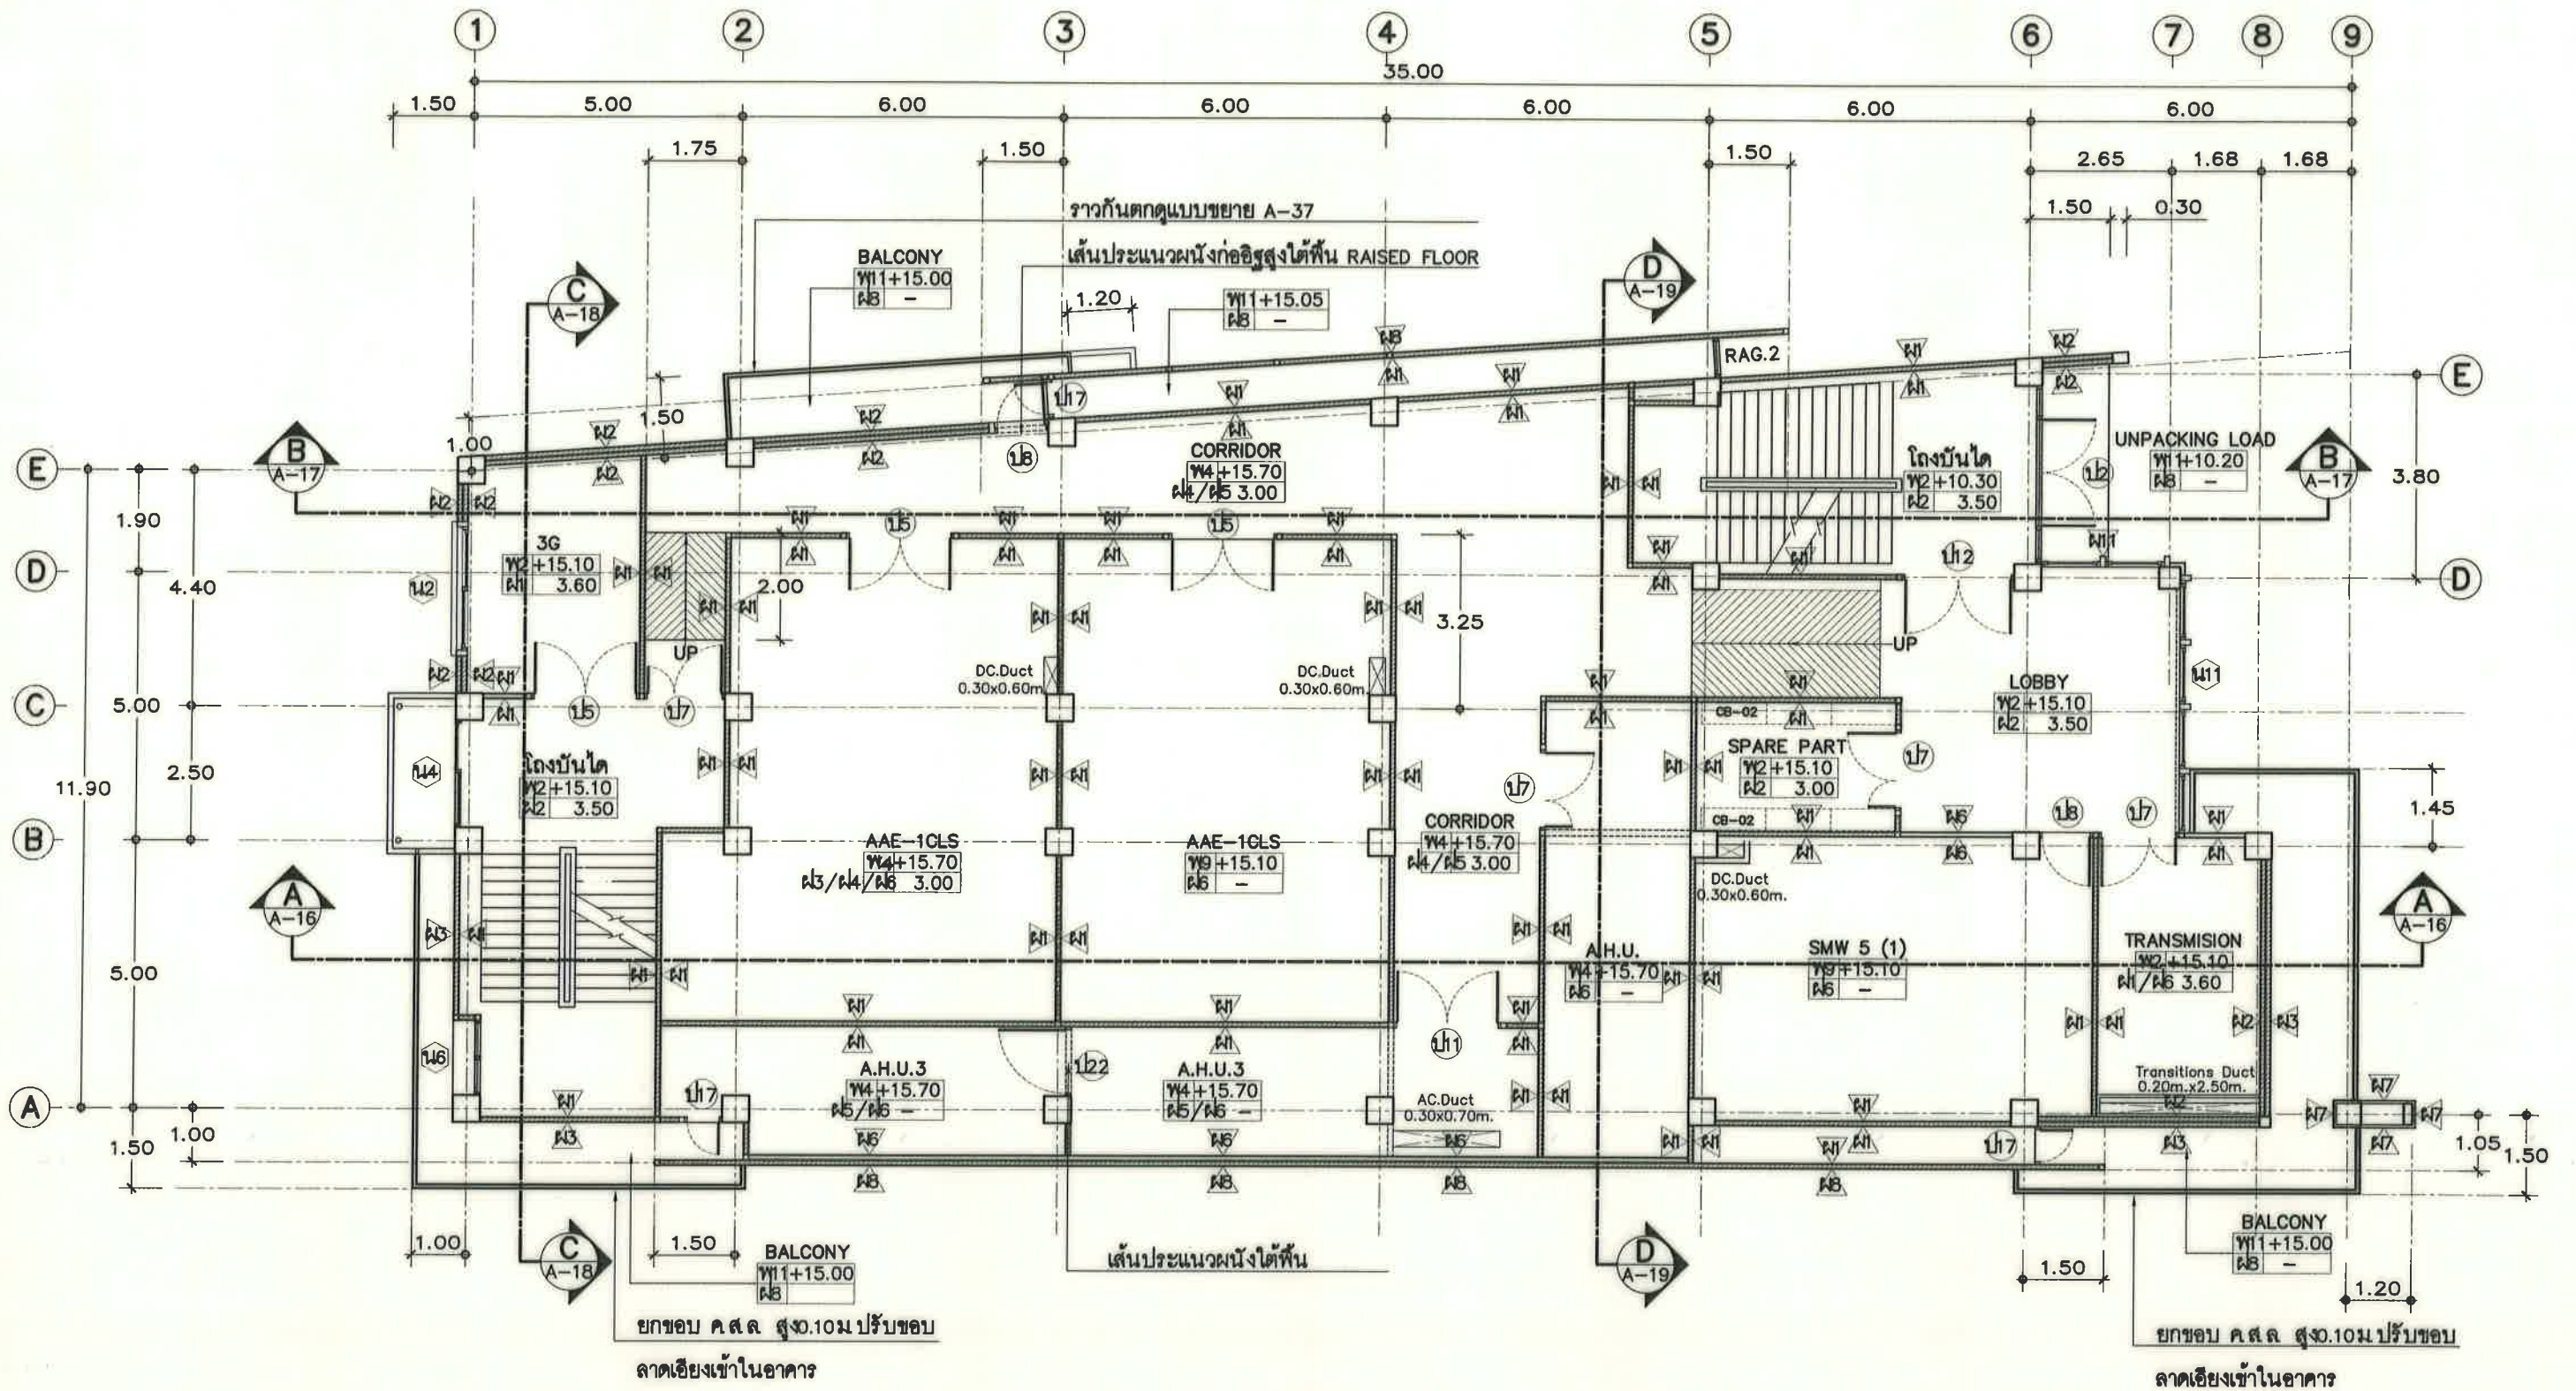


แปลนพื้นที่ 4
มาตราส่วน 1 : 125

TOT Property Management Department ฝ่ายบริหารทรัพย์สิน ส่วนอาคารและวิศวกรรมอาคาร	เจ้าของโครงการ	ฝ่ายพัฒนาผลิตภัณฑ์ระหว่างประเทศ	สถาปนิก	สนั่น นาคนิกร ๓-๙๙๙๖๑๙	วิศวกรระบบไฟฟ้ากำลัง	เดลินชัย พงษ์ชากร ๓๖๒๕	วิศวกรระบบป้องกันอัคคีภัย	ประทีป อินทพันธ์ ๓๖๒๗	ตรวจ	วิมลรัตน์ พิชัยมาศ 18/๓๓/๕๕	ผจ.สอ.พ.	เลขที่แบบ
	แบบ	งานจ้างเหมาก่อสร้างอาคารสถานที่มีโครงสร้างคานเหล็ก ปากบารา	วิศวกรโครงสร้าง	เอกสิทธิ์ จิระเกียรติ สย๕๗๗๘	วิศวกรระบบควบคุมอัตโนมัติ	จิระชัย เวชสุทธิคุณ ๓๖๓๐	วิศวกรระบบดับเพลิงอัตโนมัติ	ปรีชา เหมพันธ์ ๓๖๓๐๑๔	เห็นชอบ	วิมลรัตน์ พิชัยมาศ 18/๓๓/๕๕	ผจ.สอ.พ.	A-09
	แสดง	แปลนพื้นที่ 4	มาตราส่วน	1 : 125	วิศวกรระบบสุขาภิบาล	พนัสศักดิ์ บุญทวี ๓๖๓๕๗๔	วิศวกรระบบปรับอากาศ	สุมิตร ศรีวัฒน ๓๖๓๐๖๖	อนุมัติ	วิมลรัตน์ พิชัยมาศ 18/๓๓/๕๕	ผจ.สอ.พ.	แผ่นที่/รวม
		เขียน	สิงห์ ชาติ	เดลินชัย พงษ์ชากร ๓๖๒๕	ป่านทิพย์ พูนผล	๓๖๓๕๗๔			๓๖๓๕๗๔	๓๖๓๕๗๔	๓๖๓๕๗๔	9/49

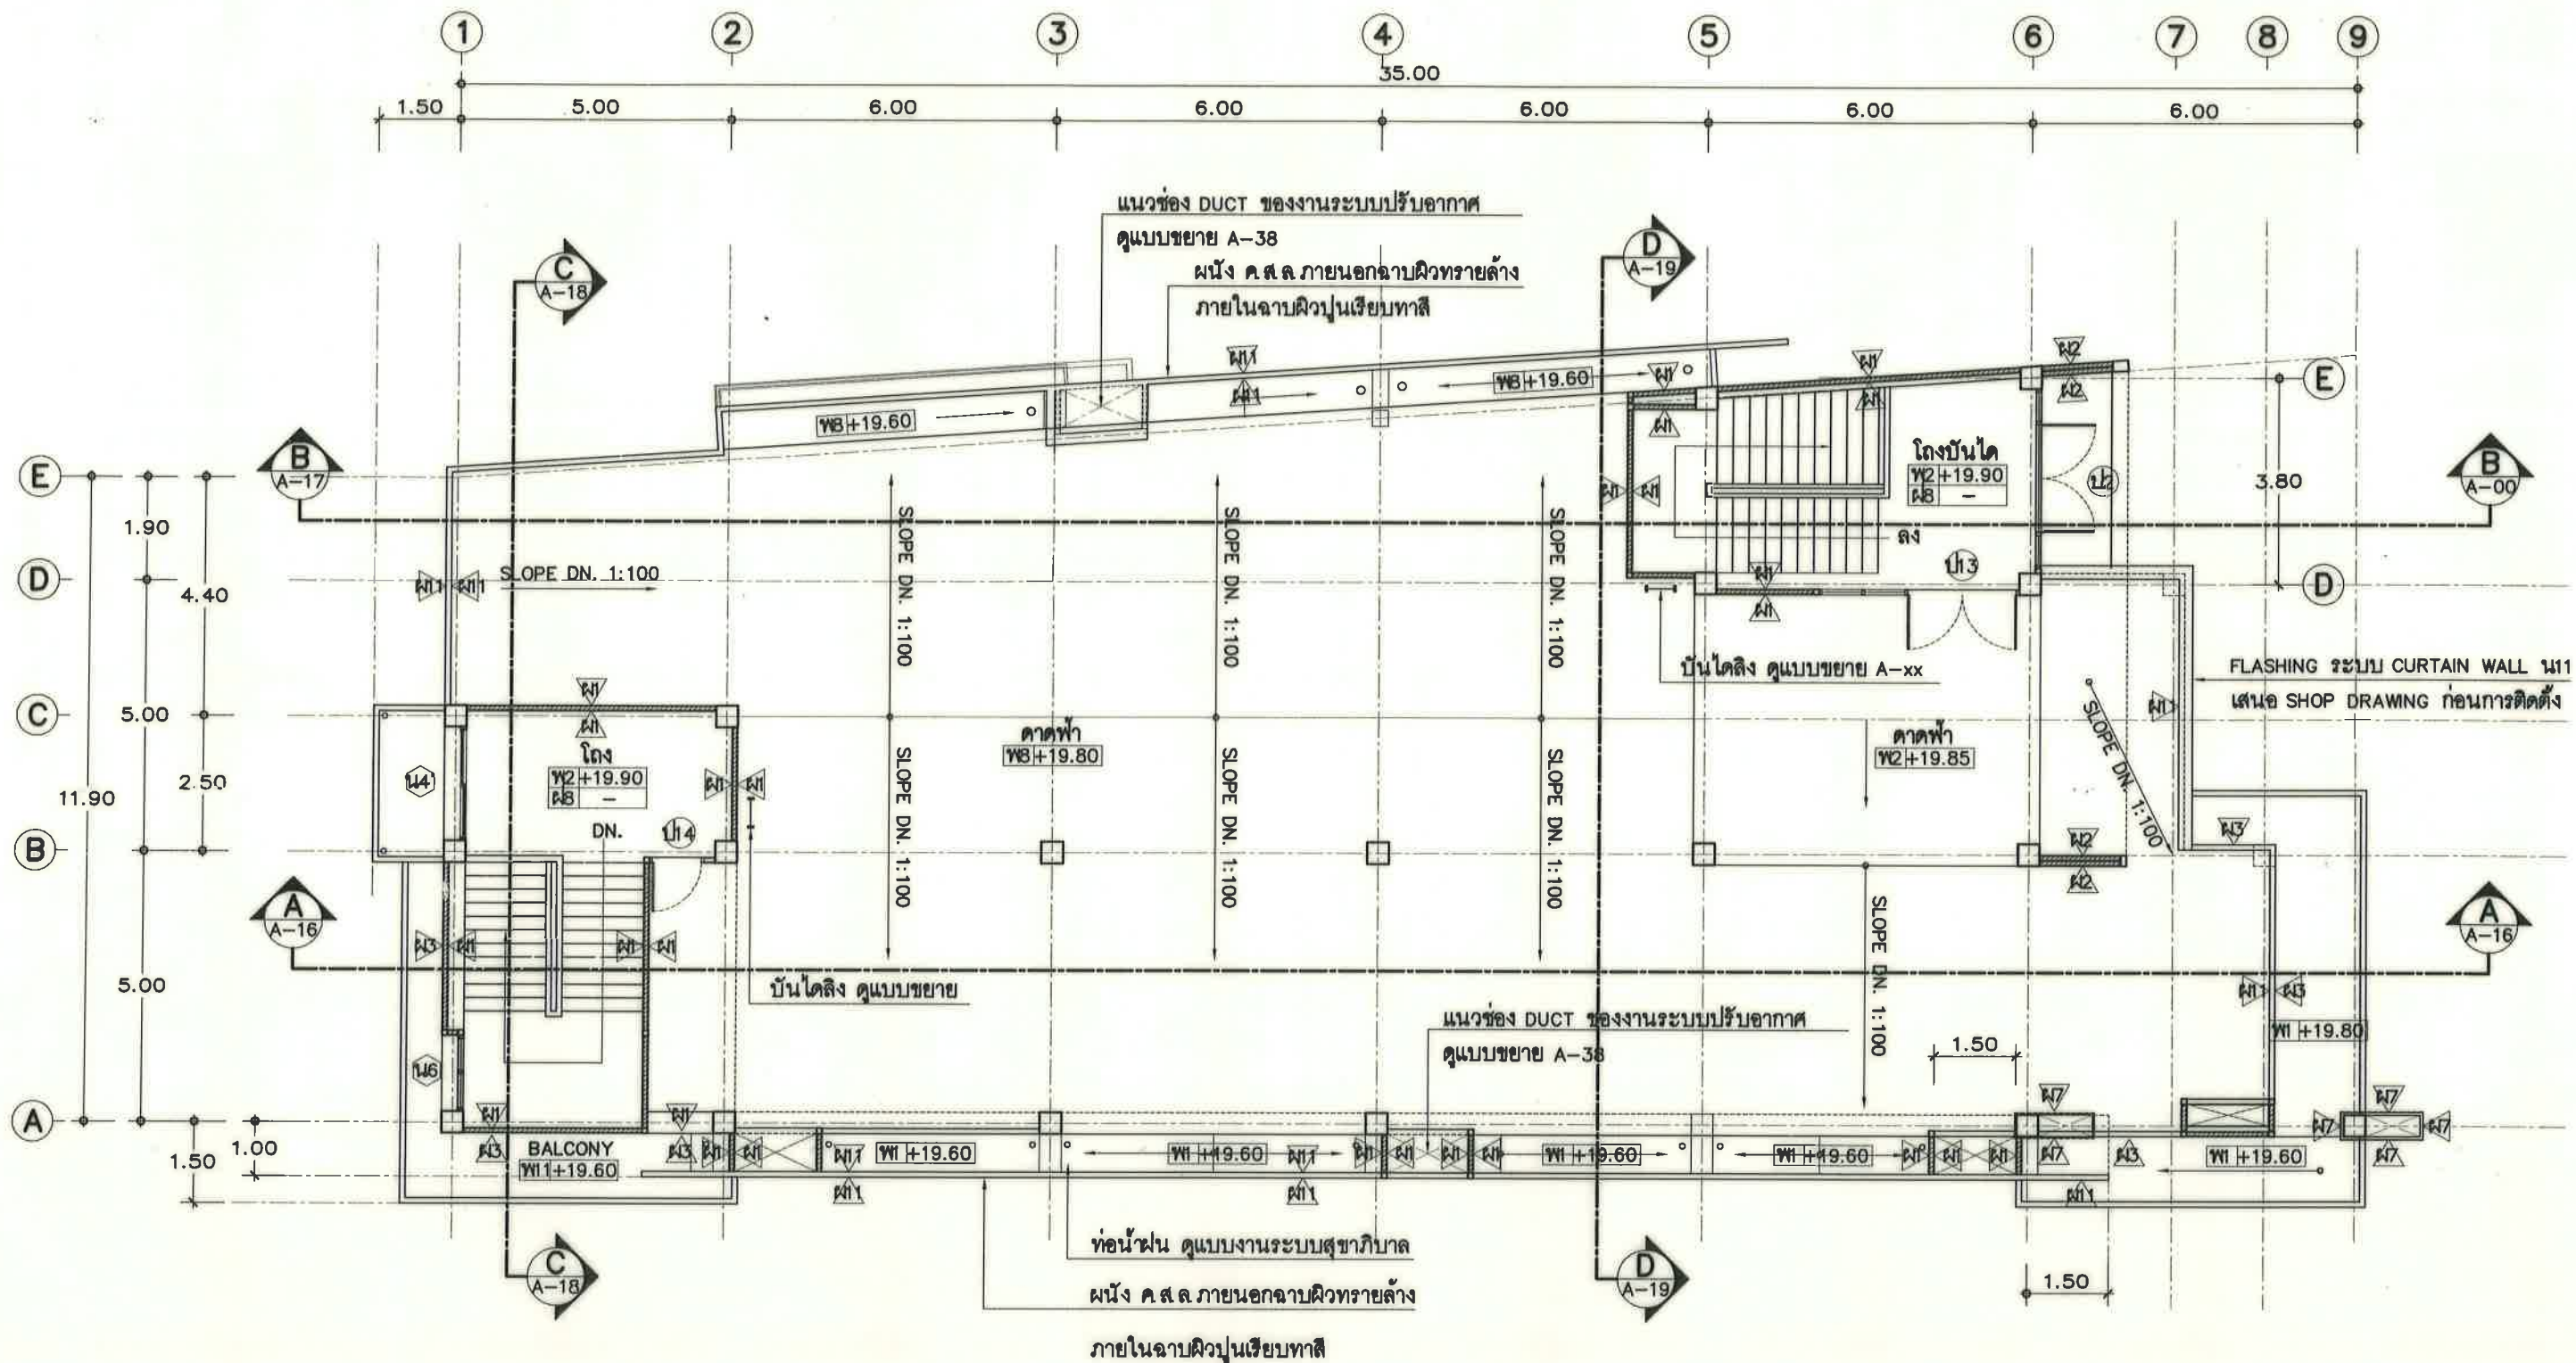


แปลนพื้นชั้นคาเฟ่
มาตราส่วน 1 : 125

 Property Management Department ฝ่ายบริหารทรัพย์สิน ส่วนอำนวยการวิศวกรรมอาคาร	เจ้าของโครงการ	ฝ่ายพัฒนาผลิตภัณฑ์ระหว่างประเทศ	สถาปนิก	สนั่น นาคนิกร ก-สถ.9619	วิศวกรระบบไฟฟ้ากำลัง	เฉลิมชัย พงษ์พานิช ภพ.6625	วิศวกรระบบป้องกันอัคคีภัย	ประทีป ชินทรศักดิ์ ภพ.6707	ตรวจ	วิมลรัตน์ วัฒนาศาสตร์ 18.04.52	เลขที่แบบ	A-10
	แบบ	งานจ้างเพื่อก่อสร้างอาคารสถานีโครงการเคเบิลโดรน ปากบารา	วิศวกรโครงสร้าง	เอกสิทธิ์ จิระกรเกียรติ สย.5778	วิศวกรระบบควบคุมอัตโนมัติ	พงษ์ศักดิ์ บุญทวี ภพ.5874	วิศวกรระบบดับเพลิงอัตโนมัติ	ปรีชา เหมมัน สก.3014	เห็นชอบ	วิมลรัตน์ วัฒนาศาสตร์ 26.04.52	แผนที่/รวม	10/49
	แสดง	อลง จ.สถ. พร้อมงานติดตั้งระบบปรับอากาศ และงานรื้อถอน	วิศวกรระบบสุขาภิบาล	เฉลิมพล อุดมย์นทร ภย.21035	วิศวกรระบบสื่อสารสัญญาณ	ปานทิพย์ พูนผล	วิศวกรระบบปรับอากาศ	สุมิตร ศรีวิวัฒน์ ภก.10666	อนุมัติ	สุชาติ ทรัพย์ 27.05.52		
	แปลนพื้นชั้นคาเฟ่		มาตราส่วน	1 : 125	เขียน		สนั่น นาคนิกร					

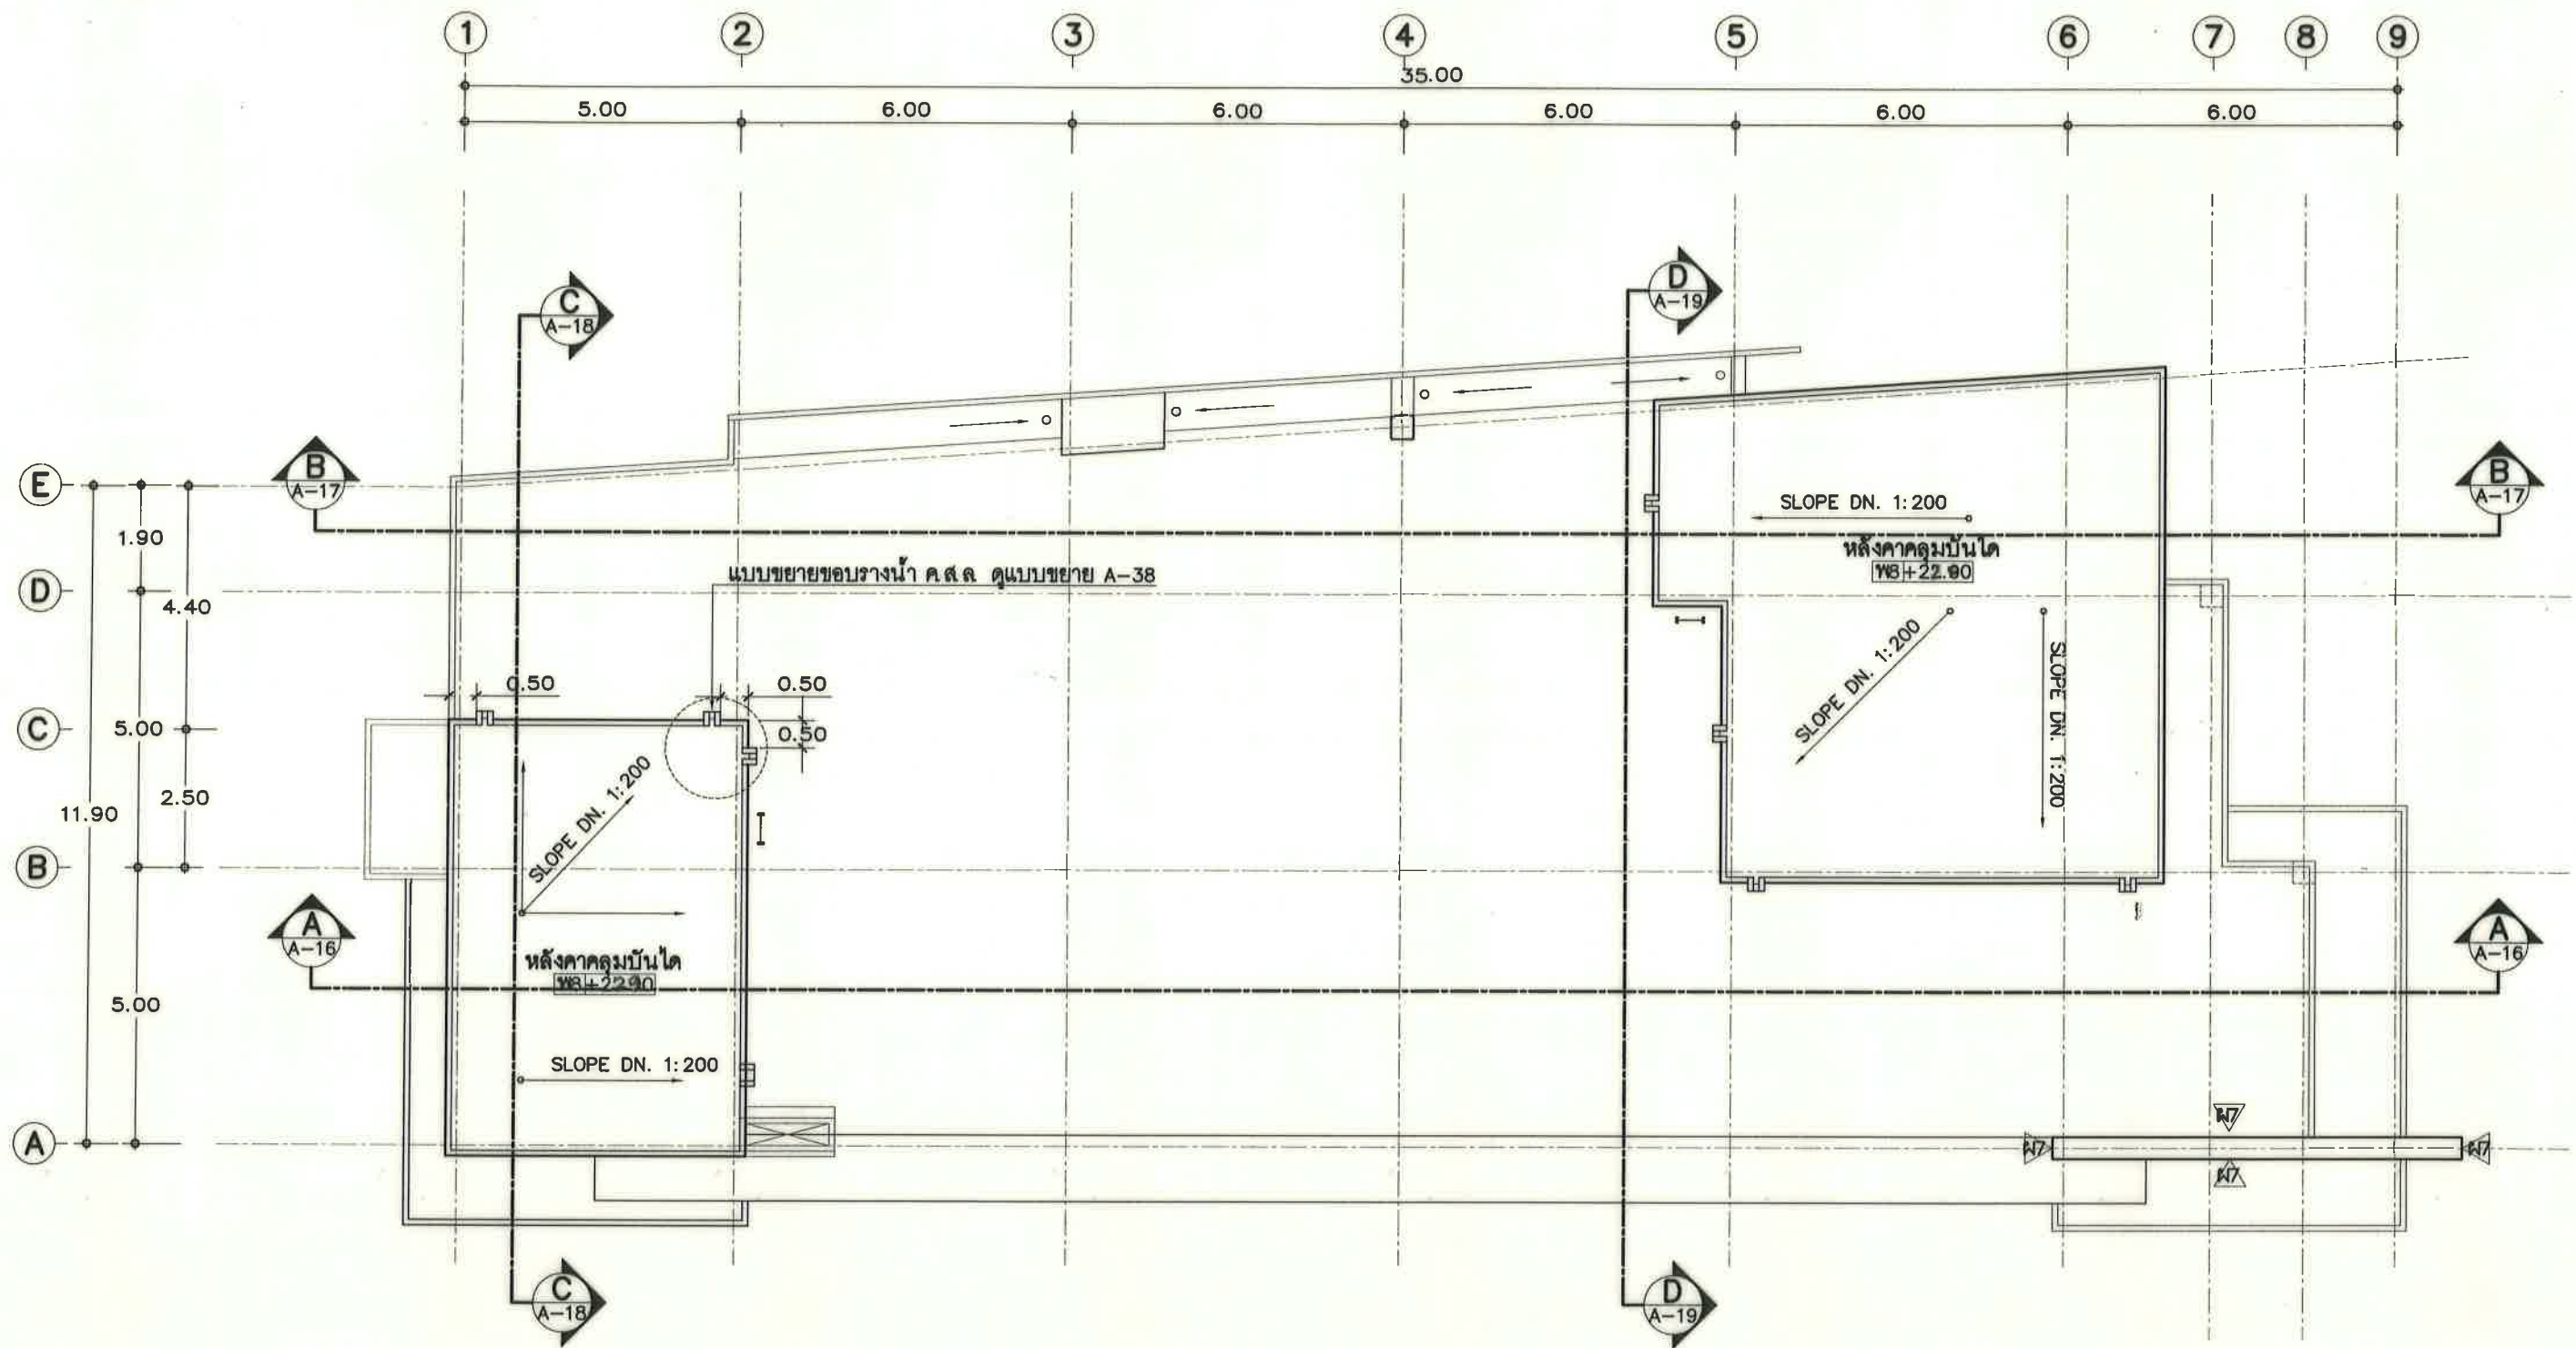


แปลนพื้นหลังคาคลุมบันได
มาตราส่วน 1 : 125

 Property Management Department ฝ่ายบริหารทรัพย์สิน ส่วนอาคารและวิศวกรรมอาคาร	เจ้าของโครงการ	ฝ่ายพัฒนาผลิตภัณฑ์ระหว่างประเทศ	สถาปนิก	สนั่น นาคนิกร ภา-สถ.9619	วิศวกรระบบไฟฟ้ากำลัง	เฉลิมชัย พงศากร ภาฟก 8625	วิศวกรระบบป้องกันอัคคีภัย	ประทีป อินทพงศ์ ภาฟค 6707	ตรวจ	ผจ.สอ.ทพ.	เลขที่แบบ
	แบบ	งานจ้างเหมาก่อสร้างอาคารสถานที่โครงการเคเบิลทีวี ปากบารา	วิศวกรโครงสร้าง	เอกสิทธิ์ จิงขจรเกียรติ สย.5778	วิศวกรระบบควบคุมอัตโนมัติ	พงษ์ศักดิ์ บุญทวี ภาฟค 5874	วิศวกรระบบดับเพลิงอัตโนมัติ	ปรีชา เหมมัน สก.3014	เห็นชอบ	ผจ.สอ.ทพ.	A-11
	แสดง	แปลนพื้นหลังคาคลุมบันได	มาตราส่วน	1 : 125	วิศวกรระบบสุขาภิบาล	เฉลิมพล อุดยัษฐ ภาข 21035	วิศวกรระบบปรับอากาศ	สุมิตร ศรีวิวัฒน์ ภาค.10666	อนุมัติ	ผจ.ทพ.	แผ่นที่/รวม
		สนั่น นาคนิกร	เขียน	สนั่น นาคนิกร					รชิต ทรัพย์	27	11/49

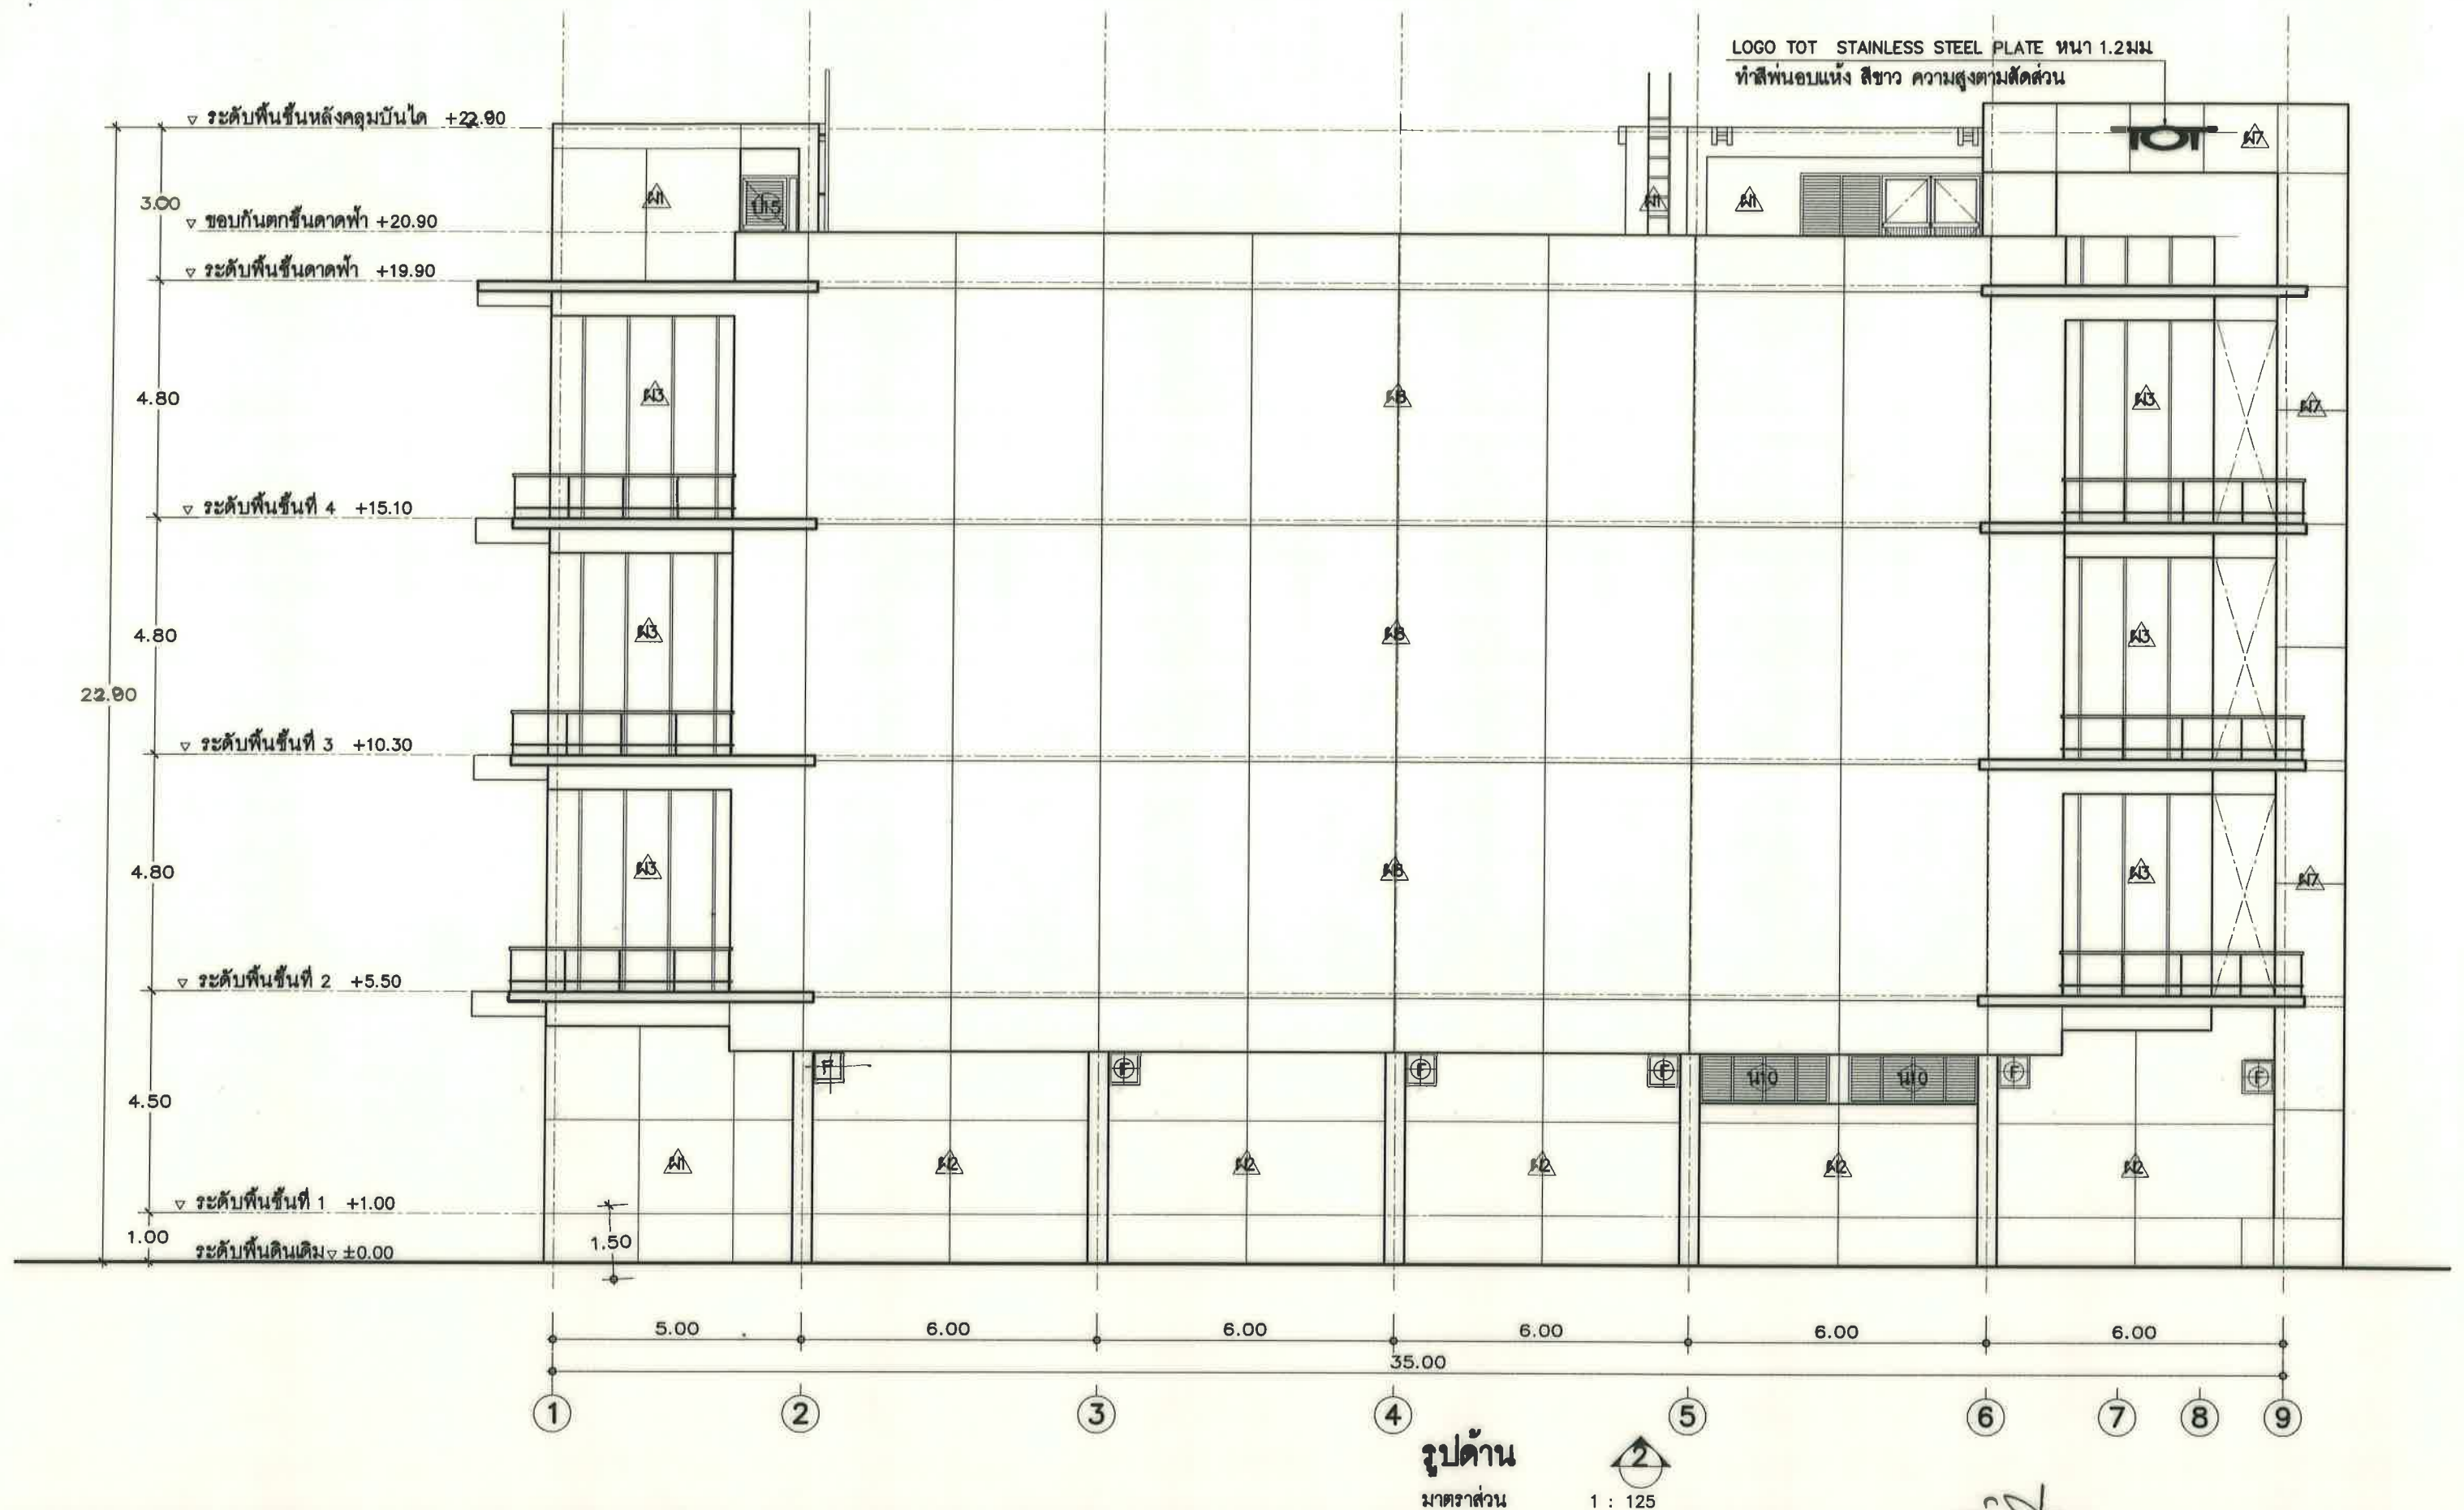

Property Management Department ฝ่ายบริหารทรัพย์สิน ส่วนออกใบอนุญาตอาคาร	เจ้าของโครงการ ฝ่ายพัฒนาผลิตภัณฑ์ระหว่างประเทศ แบบ งานจ้างเหมาก่อสร้างอาคารสถานีโครงการเคเบิลไต่หน้า ปากบารา อลูมิเนียม หรืองานติดตั้งระบบปรับอากาศ และงานรื้อถอน		สถาปนิก สนั่น นาคนิกร ภา-สถ.9619	วิศวกรระบบไฟฟ้ากำลัง เจริญชัย พงศขาร ภาทก 6625 จิระชาย เวชวิสุทธิคุณ ภาทก 19309	วิศวกรระบบป้องกันอัคคีภัย ประทีป อินทรศักดิ์ ภาทก 6707	ตรวจ วัชรพงศ์ พิทยามาศ 26/10/57 เห็นชอบ วัชรพงศ์ พิทยามาศ 26/10/57 อนุมัติ รุชติ ชัยสุข 27/10/57	เลขที่แบบ A-13 แผ่นที่/รวม 13/49
	มาตรฐาน 1 : 125		วิศวกรโครงสร้าง เอกสิทธิ์ จิระเกียรติ สข.5778	วิศวกรระบบควบคุมอัตโนมัติ พงษ์ศักดิ์ บุญทวี ภาทก.5874	วิศวกรระบบดับเพลิงอัตโนมัติ ปรีชา เหมมัน สก.3014	วิศวกรระบบปรับอากาศ สุมิตร ศรีวิวัฒน์ ภาท.10666	
	เขียน สนั่น นาคนิกร		วิศวกรระบบสุขาภิบาล เจริญพล อดุลย์บุตร ภาข. 21035	วิศวกรระบบสื่อสารสัญญาณ ปานทิพย์ พูนผล			
	รูปด้าน 2						

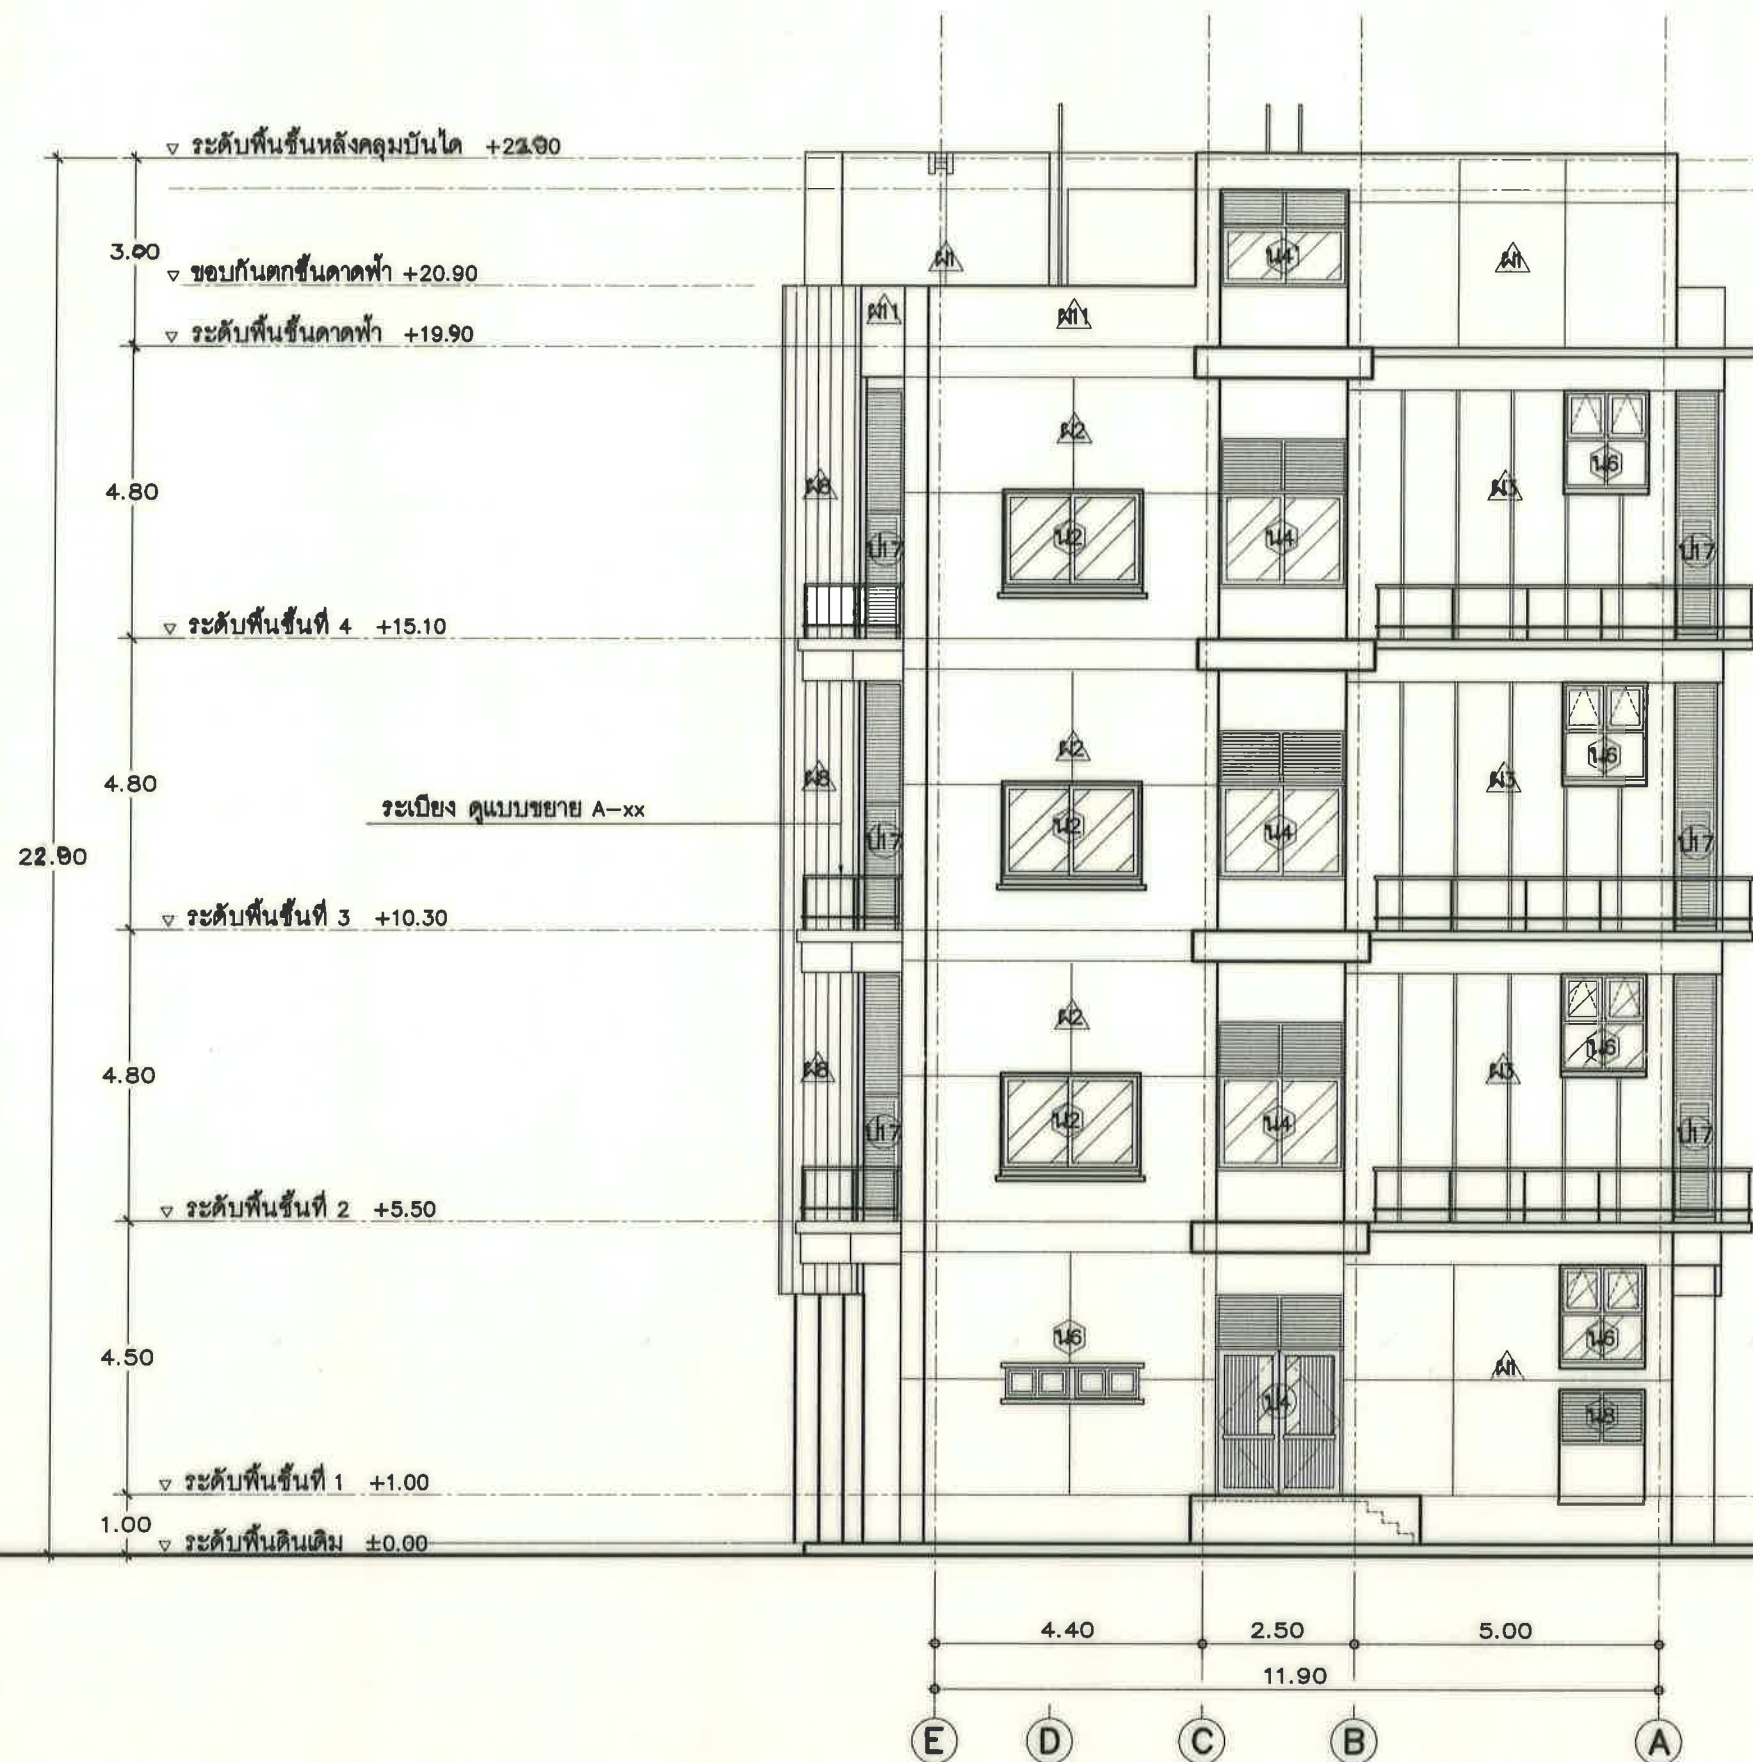


รูปด้าน

มาตราส่วน

3
1 : 125

 Property Management Department ฝ่ายบริหารทรัพย์สิน ส่วนอาคารและวิศวกรรมอาคาร	เจ้าของโครงการ	ฝ่ายพัฒนาผลิตภัณฑ์ระหว่างประเทศ	สถาปนิก	สนั่น นาคนิกร ๓-๕๑๑๖๑๙	วิศวกรระบบไฟฟ้ากำลัง	เฉลิมชัย พงษ์พานิช ๓๖๒๕	วิศวกรระบบป้องกันอัคคีภัย	ประทีป อินทรพิทักษ์ ๓๖๒๗	ตรวจ	วิมลพร/พิทยามาศ ๑๘/๑๑/๕๖	เลขที่แบบ	A-14
	แบบ	งานจ้างเหมาก่อสร้างอาคารสถานีโครงการเคเบิลไต่หน้า ปากบารา	วิศวกรโครงสร้าง	เอกสิทธิ์ จิระขจรเกียรติ ๕๗๗๘	วิศวกรระบบควบคุมอัตโนมัติ	พงษ์ศักดิ์ บุญทวี ๓๖๒๗	วิศวกรระบบดับเพลิงอัตโนมัติ	ปวิชา เหมสัน ๓๖๓๐๑๔	เห็นชอบ	คิระ มาประเสริฐ ๒๖/๑๑/๕๖	แผ่นที่/รวม	14/49
	แสดง	มาตรฐาน 1 : 125	วิศวกรระบบสุขาภิบาล	เฉลิมพล อดุลย์นคร ๓๖๒๕	วิศวกรระบบสื่อสารสัญญาณ	ปานทิพย์ พูนผล	วิศวกรระบบปรับอากาศ	สุมิตร ศรีวิวัฒน์ ๓๖๑๐๖๖	อนุมัติ	รุชติ ชาญ ๒๗/๑๑/๕๖		
	รูปด้าน 3	เขียน	สนั่น นาคนิกร									

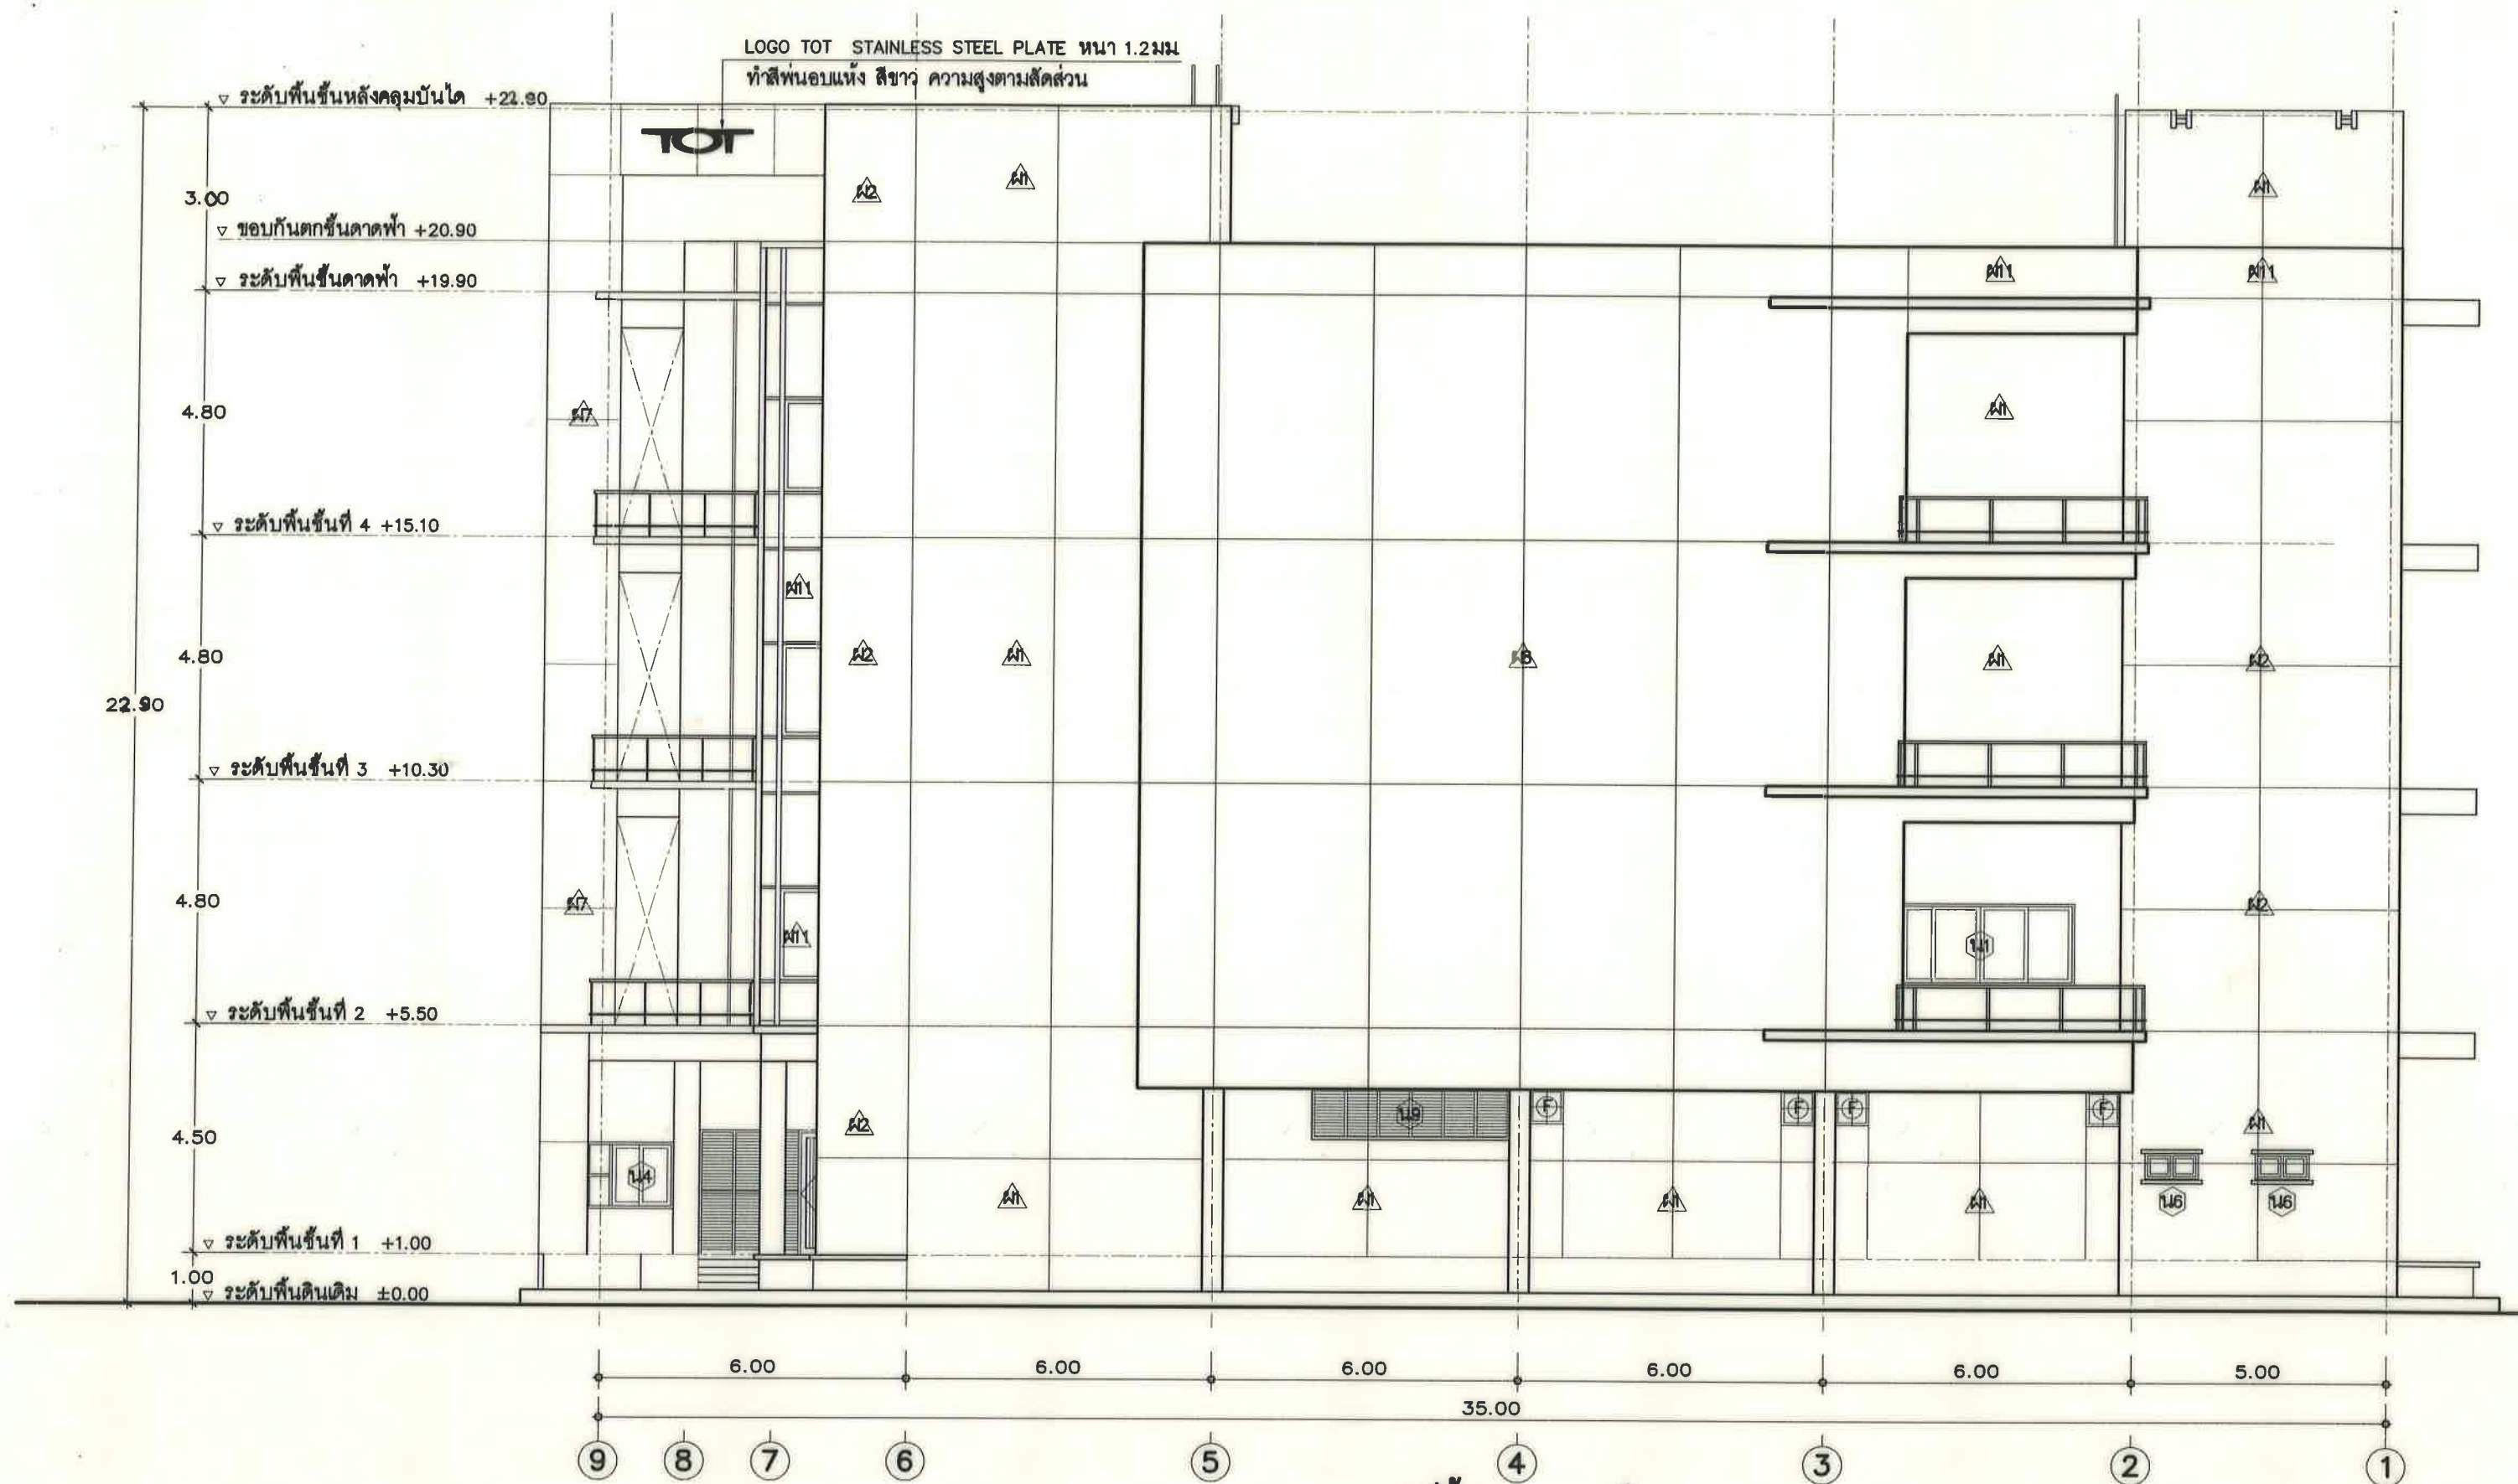


รูปด้าน

มาตราส่วน

1 : 125


Property Management Department ฝ่ายบริหารทรัพย์สิน ส่วนออกแบบวิศวกรรมอาคาร	เจ้าของโครงการ ฝ่ายพัฒนาผลิตภัณฑ์ระหว่างประเทศ		สถาปนิก	สนั่น นาคนิกร ๗-๑๑๙๖๑๙	วิศวกรระบบไฟฟ้ากำลัง	เฉลิมชัย พงษ์พานิช ๗๗๖ ๕๕๒๕	วิศวกรระบบป้องกันอัคคีภัย	ประทีป อินทรศักดิ์ ๗๗๖ ๕๕๒๕	ตรวจ	วิรัชพงศ์ วัฒนากุล ๗๗๖ ๕๕๒๕	เลขที่แบบ	A-15
	แบบ งานจ้างเหมาก่อสร้างอาคารสถานีโครงการเคเบิลไต่บันได ปากบารา		วิศวกรโครงสร้าง	เอกสิทธิ์ จันทระเกียรติ ๕๕๕ ๕๕๗๗	วิศวกรระบบควบคุมอัตโนมัติ	พงษ์ศักดิ์ บุญทวี ๗๗๖ ๕๕๒๕	วิศวกรระบบดับเพลิงอัตโนมัติ	ปรีชา เหมพันธ์ ๕๕๕ ๕๕๒๕	เห็นชอบ	พีระ มาประเสริฐ ๕๕๕ ๕๕๒๕	แผ่นที่/รวม	15/49
	แสดง		วิศวกรระบบสุขาภิบาล	เฉลิมพล อุดมบุตร ๗๗๖ ๕๕๒๕	วิศวกรระบบปรับอากาศ	ปานทิพย์ พูนผล ๕๕๕ ๕๕๒๕	วิศวกรระบบปรับอากาศ	สุมิตร ศรีวิวัฒน์ ๗๗๖ ๕๕๒๕	อนุมัติ	สุชาติ ชัยสุข ๕๕๕ ๕๕๒๕		
	รูปด้าน 4		มาตราส่วน	1 : 125	เขียน	สนั่น นาคนิกร						

19/358

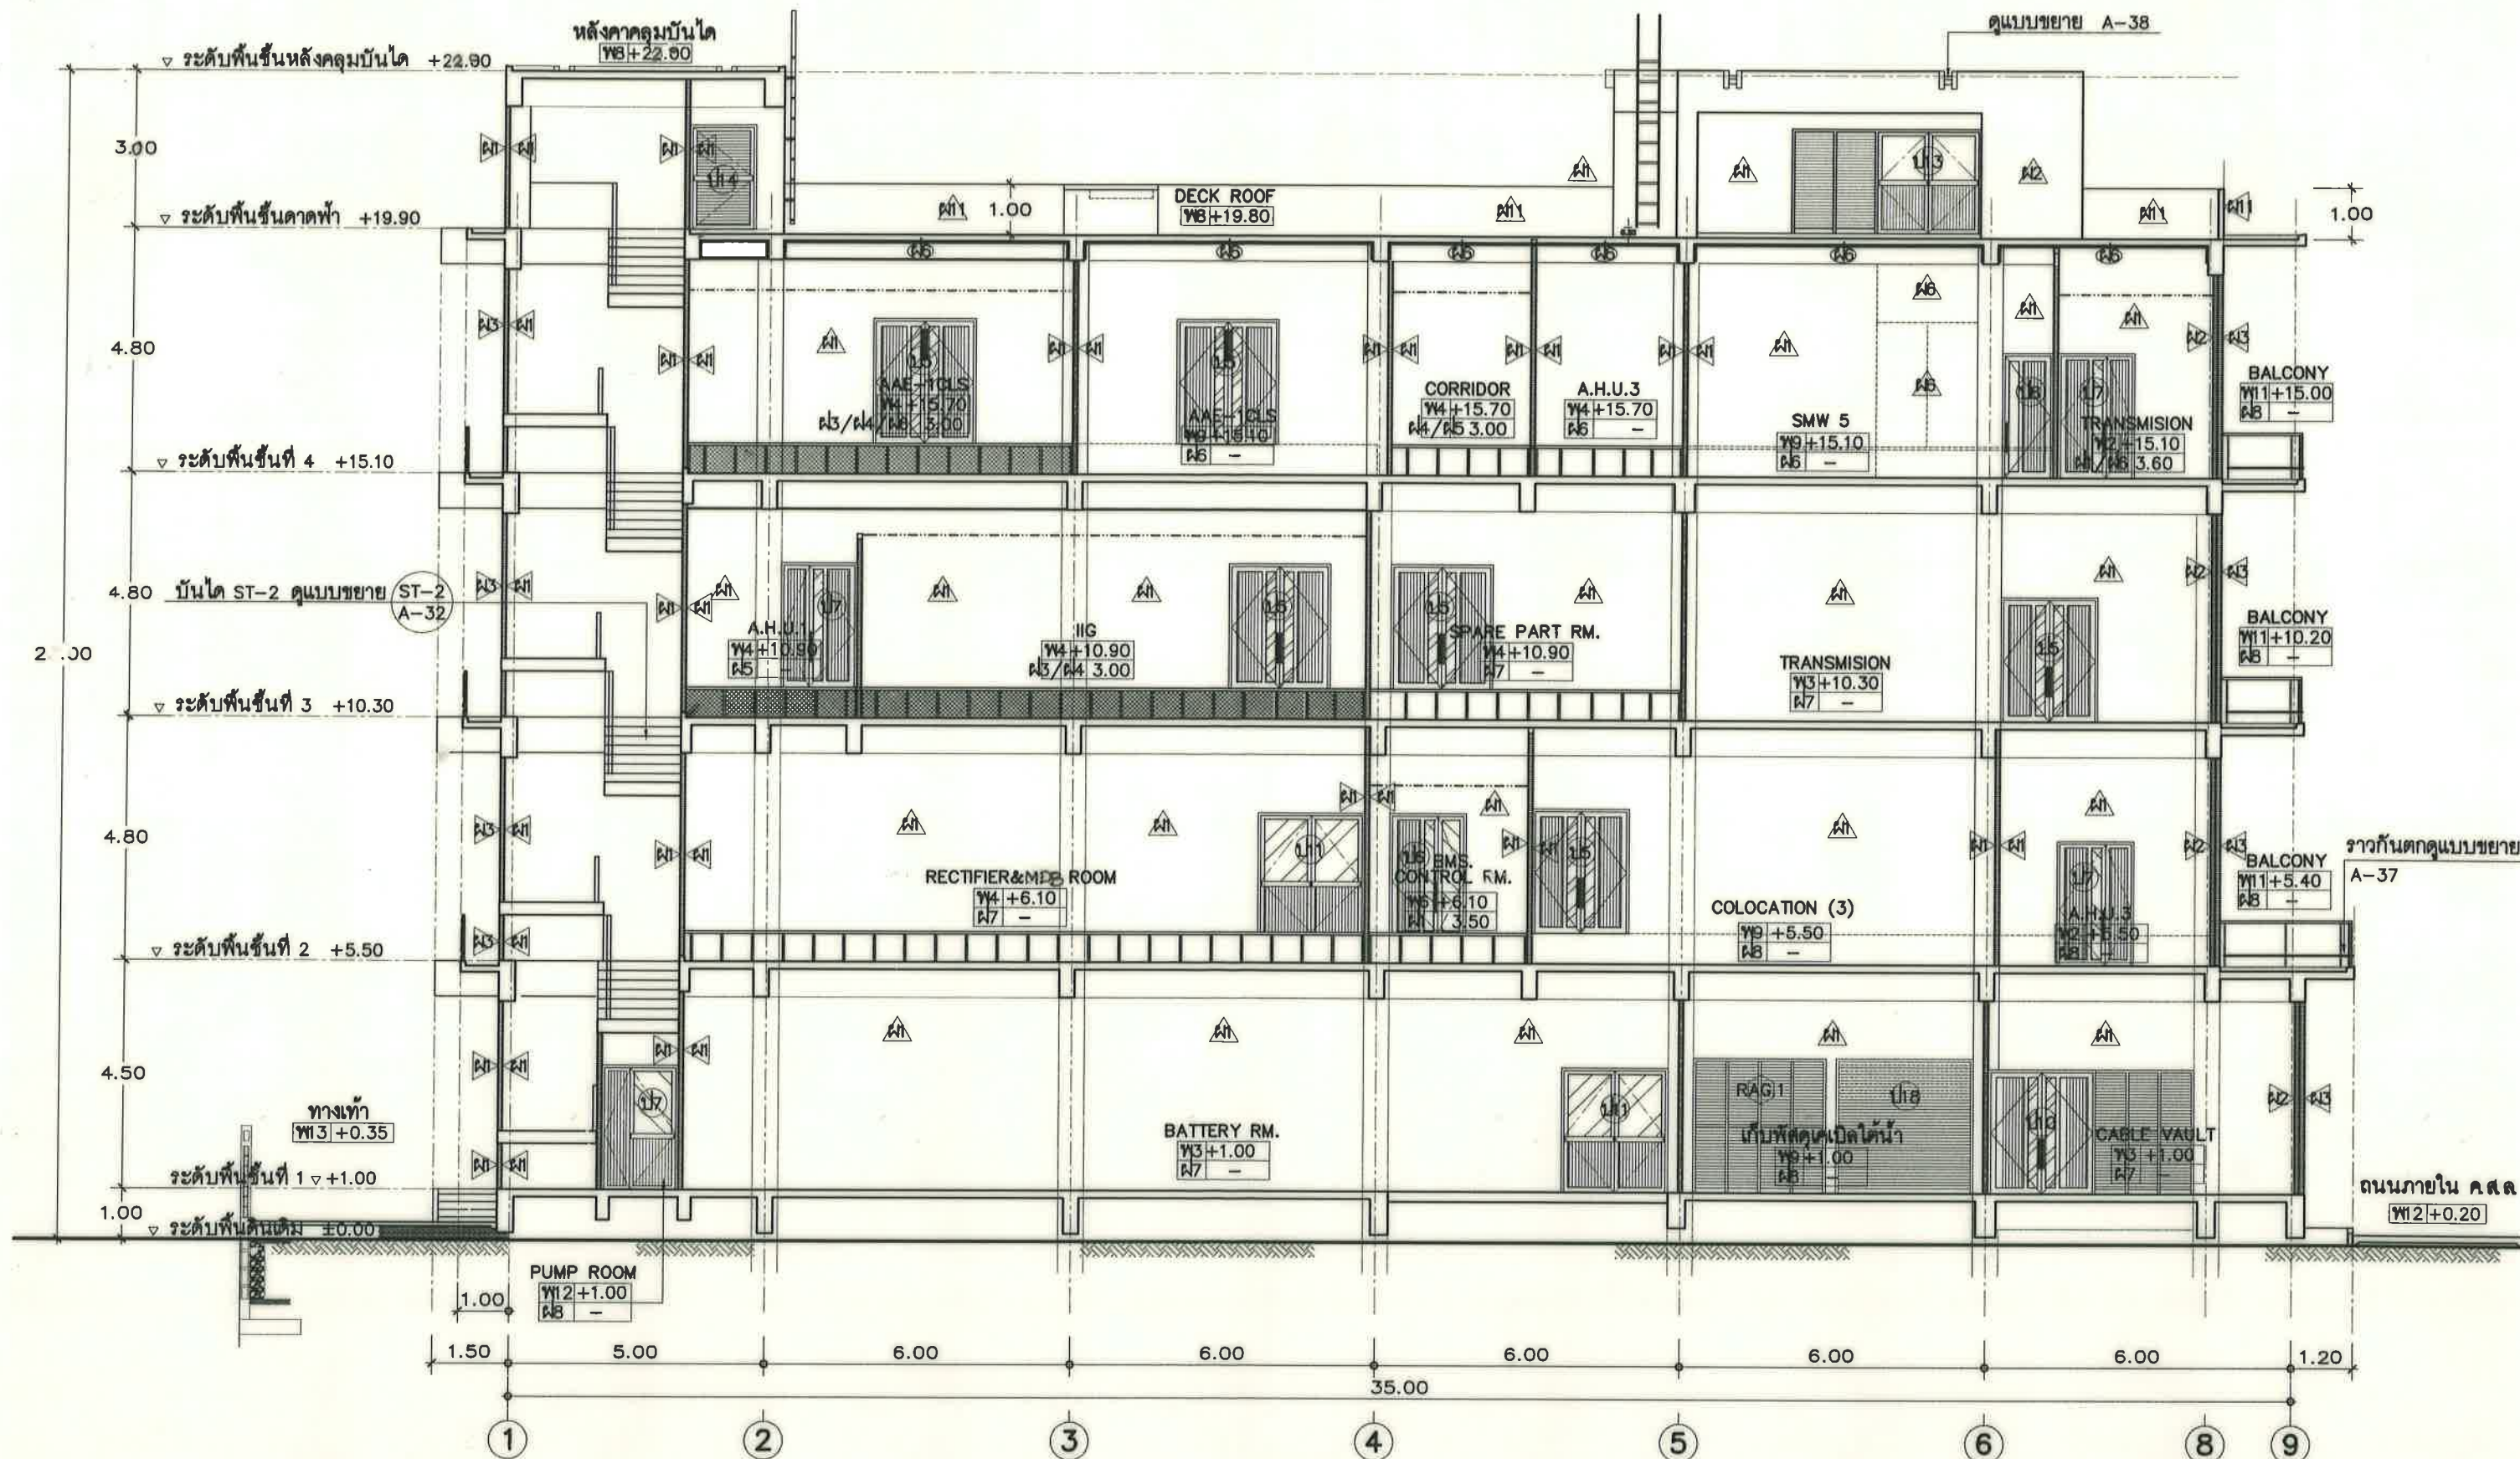


รูปตัด A-A
มาตราส่วน 1 : 125


Property Management Department ฝ่ายบริหารทรัพย์สิน ส่วนออกแบบวิศวกรรมอาคาร	เจ้าของโครงการ ฝ่ายพัฒนาผลิตภัณฑ์ระหว่างประเทศ		สถาปนิก	สนั่น นาคนิกร ก-สถ9619	วิศวกรระบบไฟฟ้ากำลัง	เฉลิมชัย พงศากร ภพท 6625	วิศวกรระบบป้องกันอัคคีภัย	ประทีป อินทศักดิ์ ภพท 6707	ตรวจ	วิรัชพงศ์ คุ้มยามมาศ 15.08.57	เลขที่แบบ
	แบบ งานจ้างเหมาก่อสร้างอาคารสถานีโครงการเขตเปิดป่า ปากบารา		วิศวกรโครงสร้าง	เอกสิทธิ์ จิระวงษ์เกียรติ สย5778	วิศวกรระบบควบคุมอัตโนมัติ	จิระชาย เจริญสุทธิคุณ ภพท 19309	วิศวกรระบบดับเพลิงอัตโนมัติ	ปรีชา เหมมัน สก3014	เห็นชอบ	วิรัชพงศ์ คุ้มยามมาศ 15.08.57	A-16
	แสดง		วิศวกรระบบสุขาภิบาล	เฉลิมพร อุดยัมบุตร ภย 21035	วิศวกรระบบสื่อสาร	ปานทิพย์ พูนผล	วิศวกรระบบปรับอากาศ	สุมิตร ศรีวิวัฒน์ ภก10666	อนุมัติ	วิรัชพงศ์ คุ้มยามมาศ 15.08.57	แผ่นที่/รวม
	รูปตัด A-A		เขียน	สนั่น นาคนิกร					อนุมัติ	วิรัชพงศ์ คุ้มยามมาศ 15.08.57	16/49

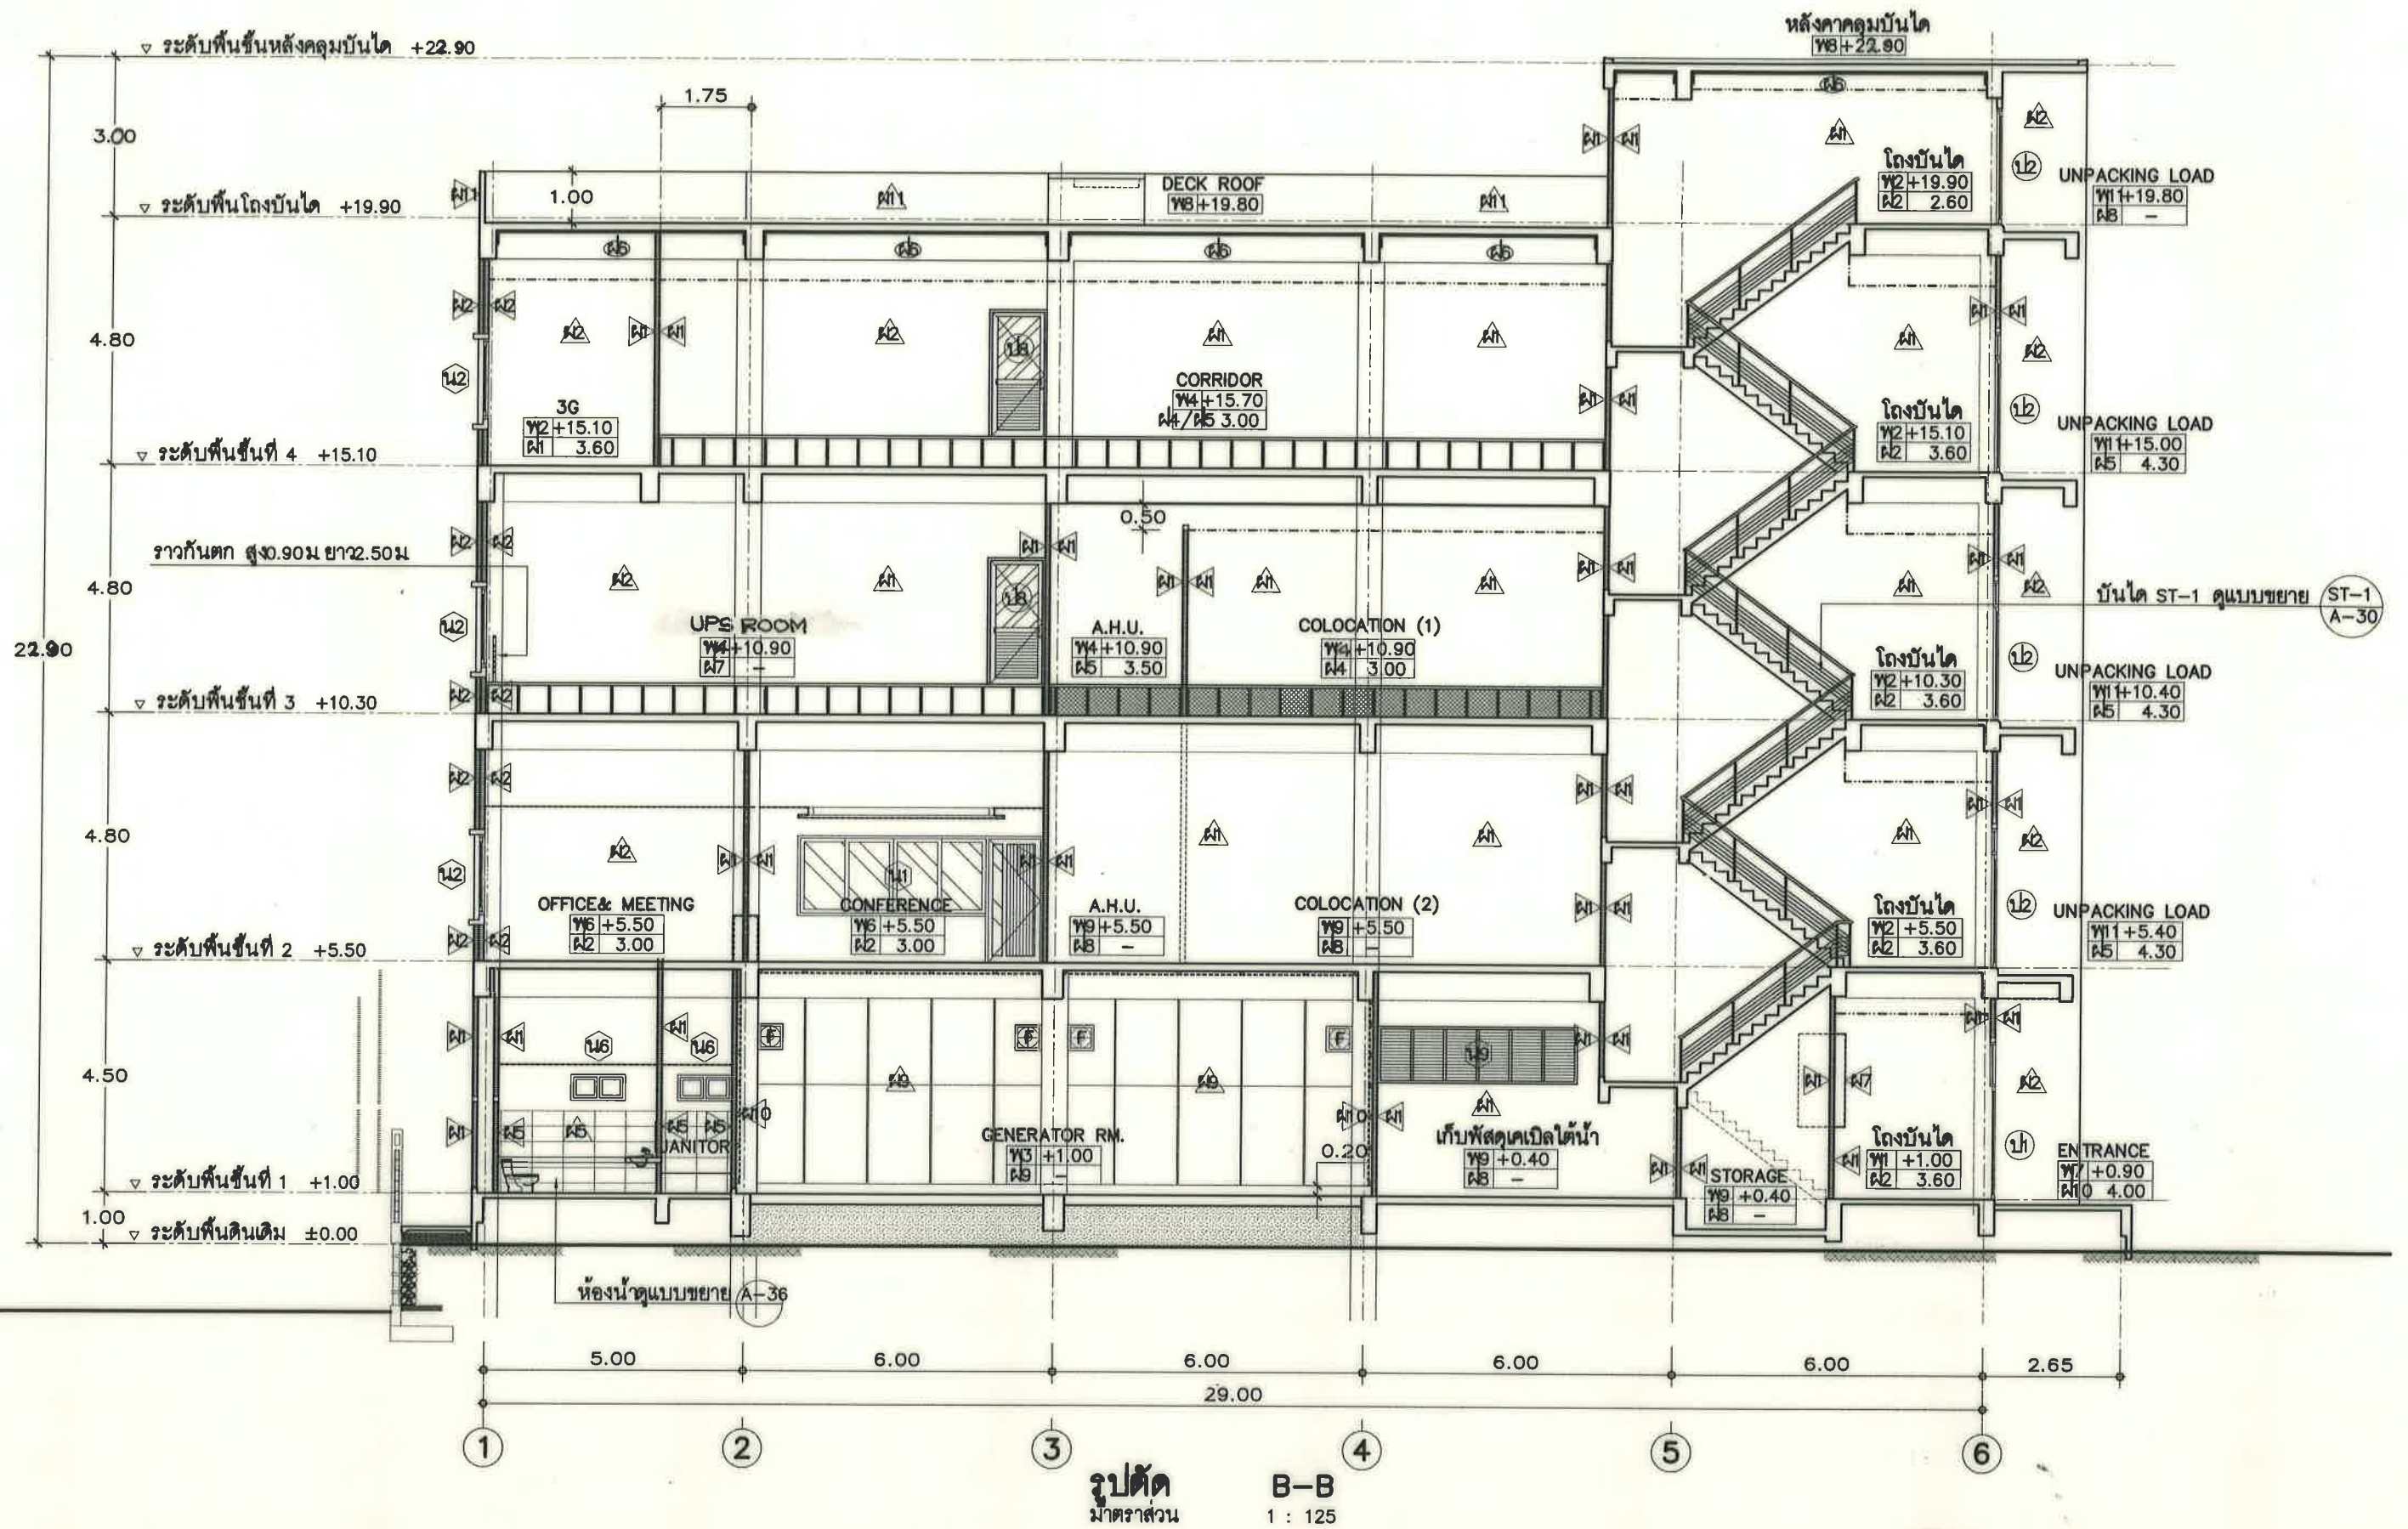


TOT Property Management Department ฝ่ายบริการทรัพย์สิน ส่วนอาคารและวิศวกรรมอาคาร	เจ้าของโครงการ	ฝ่ายพัฒนาผลิตภัณฑ์ระหว่างประเทศ	สถาปนิก	สนั่น นาคนิกร ก-สถ9619	วิศวกรระบบไฟฟ้ากำลัง	เฉลิมชัย พงกษารักษ์ ภพท 6625	วิศวกรระบบป้องกันอัคคีภัย	ประทีป อินทรศักดิ์ ภพท 6707	ตรวจสอบ	วิระพงษ์ พิทยามาศ 18.04.52	เลขที่แบบ	A-17
	แบบ	งานจ้างเหมาก่อสร้างอาคารสถานีโครงการสายเคเบิลได้นำ ปากบารา อ.สระบุรี จ.สระบุรี พร้อมงานติดตั้งระบบปรับอากาศ และงานรื้อถอน	วิศวกรโครงสร้าง	เอกสิทธิ์ จิงขจรเกียรติ สข5778	วิศวกรระบบควบคุมอัตโนมัติ	พงษ์ศักดิ์ บุญทวี ภพท 5874	วิศวกรระบบดับเพลิงอัตโนมัติ	ปรีชา เหมมื่น สก3014	เห็นชอบ	กฤษ มาประเสริฐ 26.04.52	แผ่นที่/รวม	17/49
	แสดง	รูปตัด ๑-๑	มาตราส่วน	1 : 125	วิศวกรระบบสุขาภิบาล	เฉลิมพล อุดยัมพร ภข 21035	วิศวกรระบบปรับอากาศ	สุมิตร ศรีวิวัฒน์ ภค10666	อนุมัติ	สุชาติ รวยสุข 27.04.52		
			เขียน	สนั่น นาคนิกร								

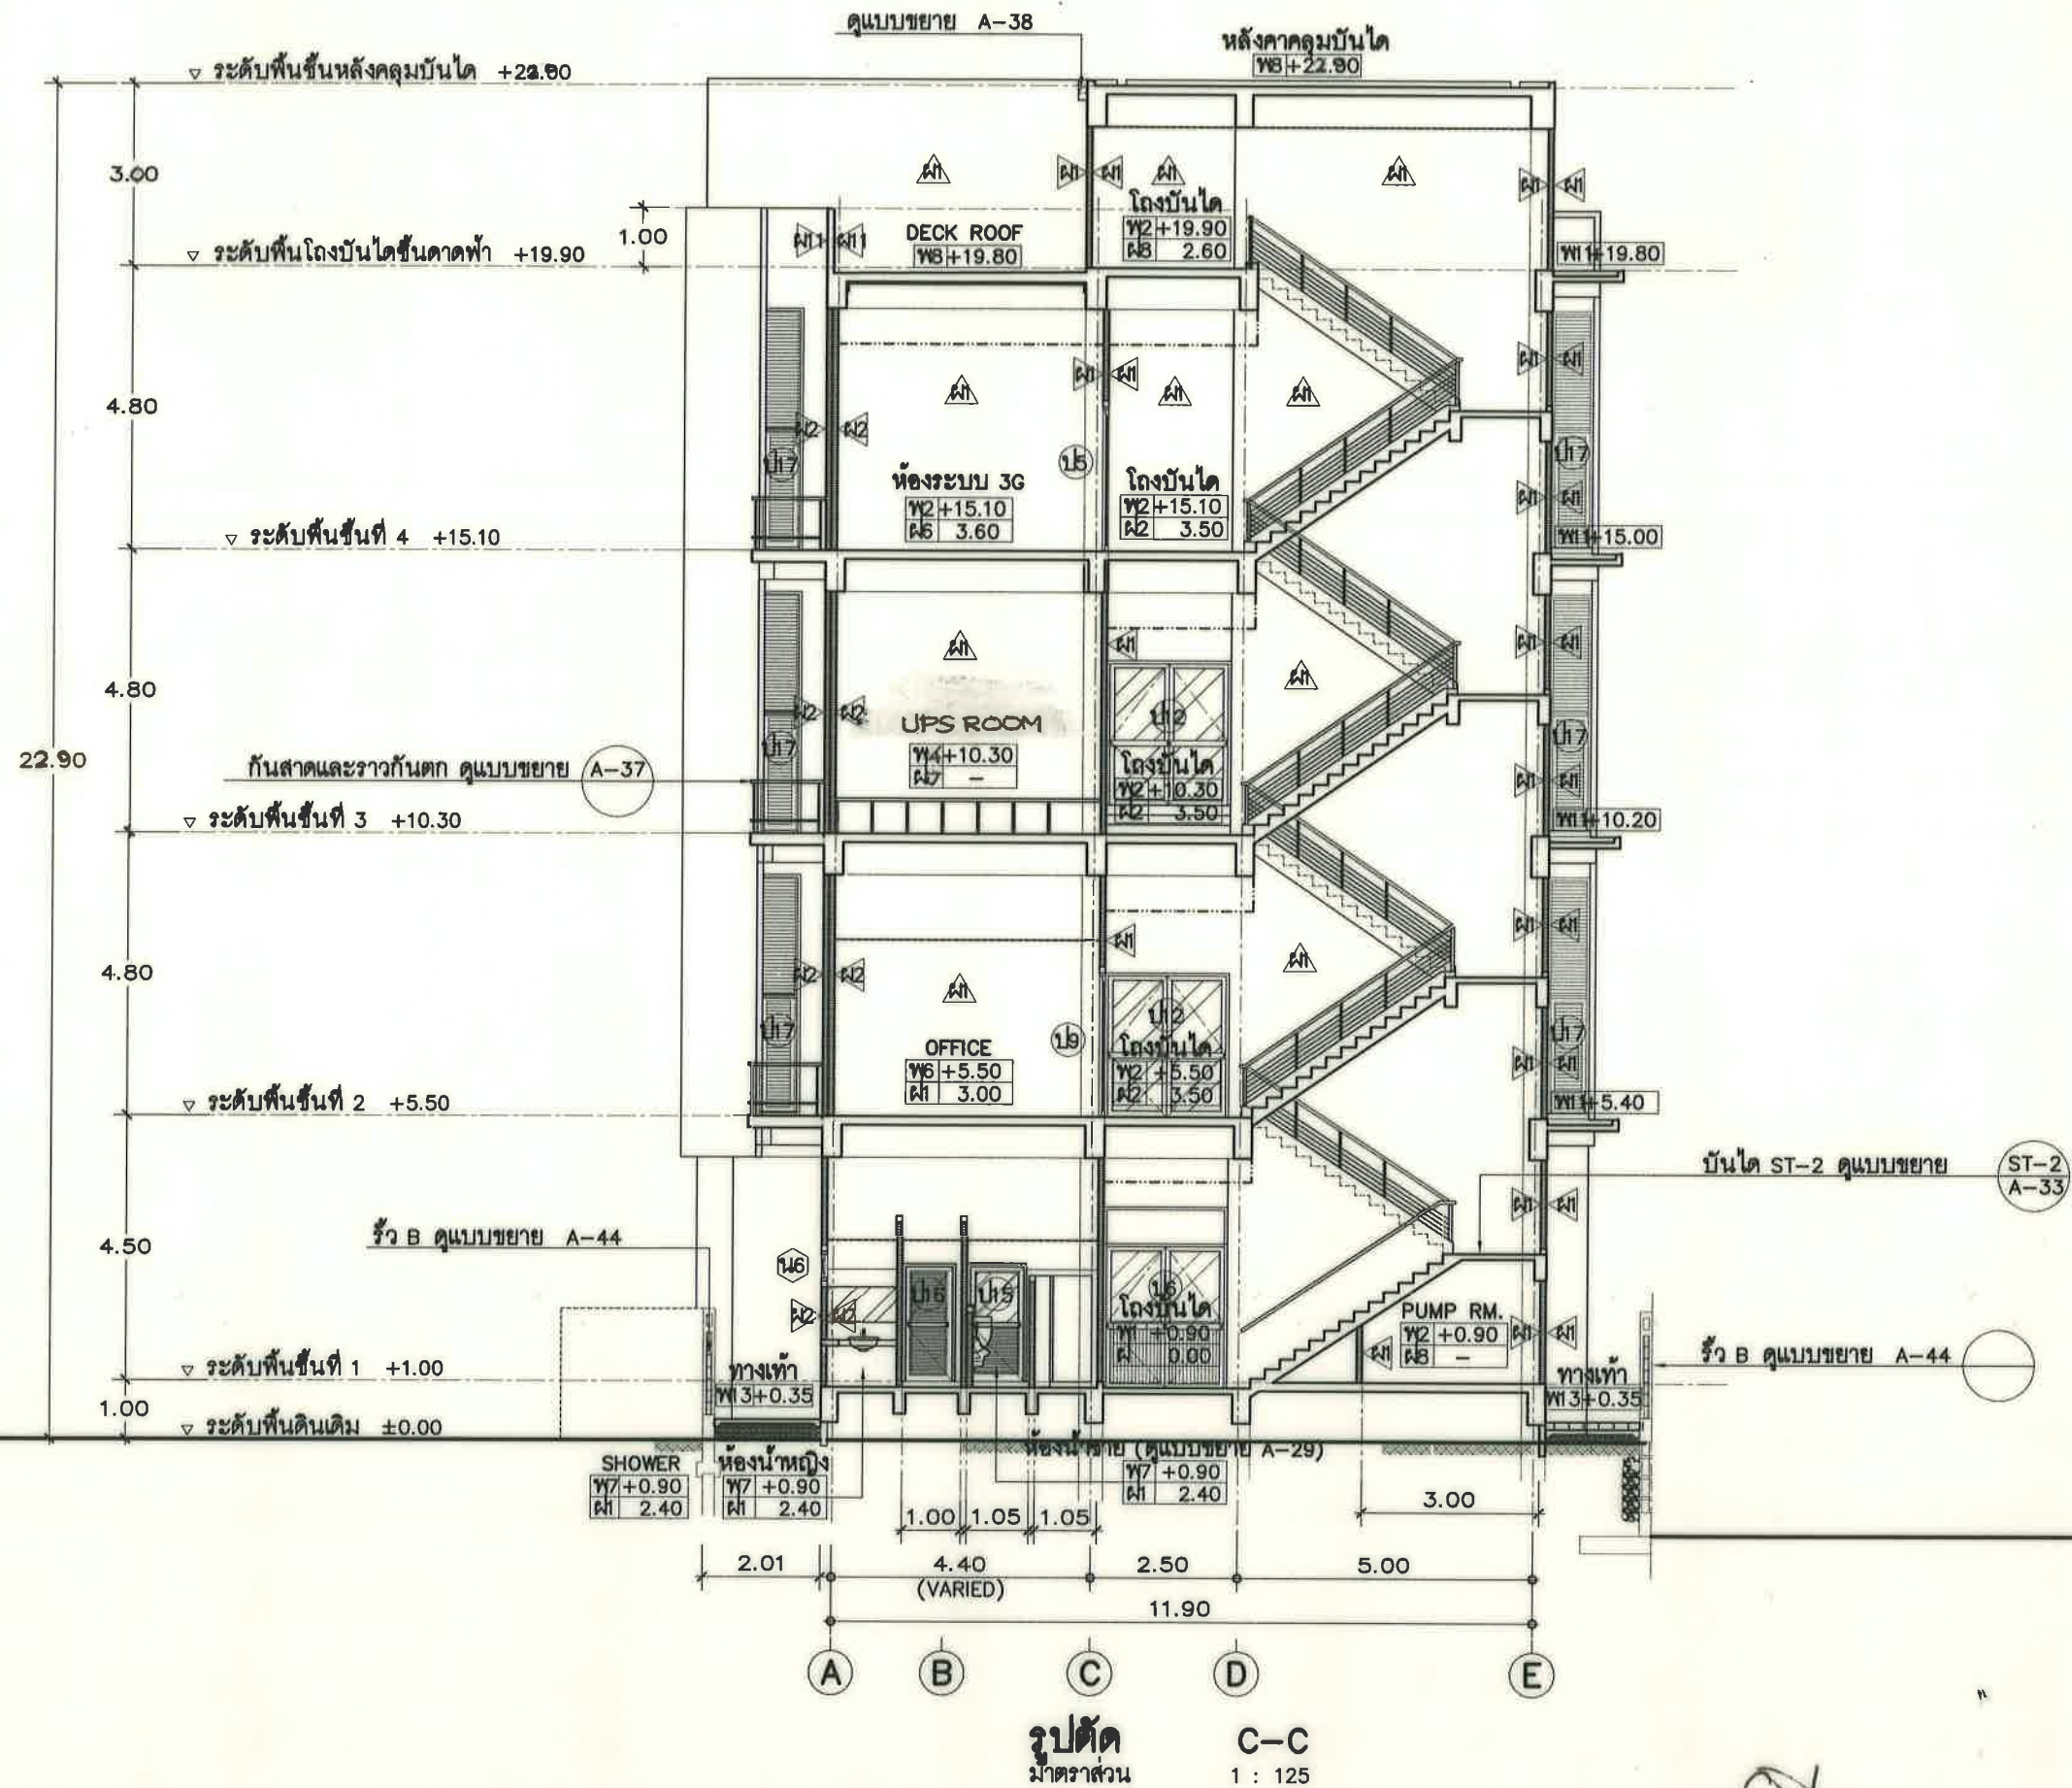


 TOT Property Management Department ฝ่ายบริหารทรัพย์สิน ส่วนอาคารและวิศวกรรมอาคาร	เจ้าของโครงการ	ฝ่ายพัฒนาผลิตภัณฑ์ระหว่างประเทศ	สถาปนิก	สนั่น นาคนิกร ๓-๘๘๙๖๑๙	วิศวกรระบบไฟฟ้ากำลัง	เฉลิมชัย พงษ์ชากร ๓๗๖ ๖๖๒๕	วิศวกรระบบป้องกันอัคคีภัย	ประทีป อินทรศักดิ์ ๓๗๖ ๖๗๐๗	ตรวจ	วิมลพร วัฒนมาศ ๑๘/๑๐/๕๖	เลขที่แบบ	A-18
	แบบ	งานจ้างเหมาก่อสร้างอาคารสถานี่โครงการเคเบิ้ลไต้ น้ำ ปากบารา	วิศวกรโครงสร้าง	เอกสิทธิ์ จิระขจรเกียรติ ๕๗๕๗๗๕	วิศวกรระบบควบคุมอัตโนมัติ	จิระชัย เจริญสุขธิคุณ ๓๗๖ ๑๙๓๐๙	วิศวกรระบบดับเพลิงอัตโนมัติ	ปรีชา เหมมัน ๓๗๖ ๓๐๑๔	เห็นชอบ	ศิริมา ประเสริฐ ๒๖/๑๐/๕๖	แผนที่/รวม	18/49
	แสดง	รูปตัด	มาตราส่วน	1 : 125	วิศวกรระบบสุขาภิบาล	พนัสศักดิ์ บุญทวี ๓๗๖ ๕๐๗๔	วิศวกรระบบปรับอากาศ	สุเมธ ศรีวิวัฒน์ ๓๗๖ ๑๐๖๖๕	อนุมัติ	สุชาติ ช่าง ๒๗/๑๐/๕๖		
			เขียน	สนั่น นาคนิกร	วิศวกรระบบสุขาภิบาล	เฉลิมพล อดุลย์บุตร ๓๗๖ ๒๑๐๓๕	วิศวกรระบบปรับอากาศ	สุเมธ ศรีวิวัฒน์ ๓๗๖ ๑๐๖๖๕				

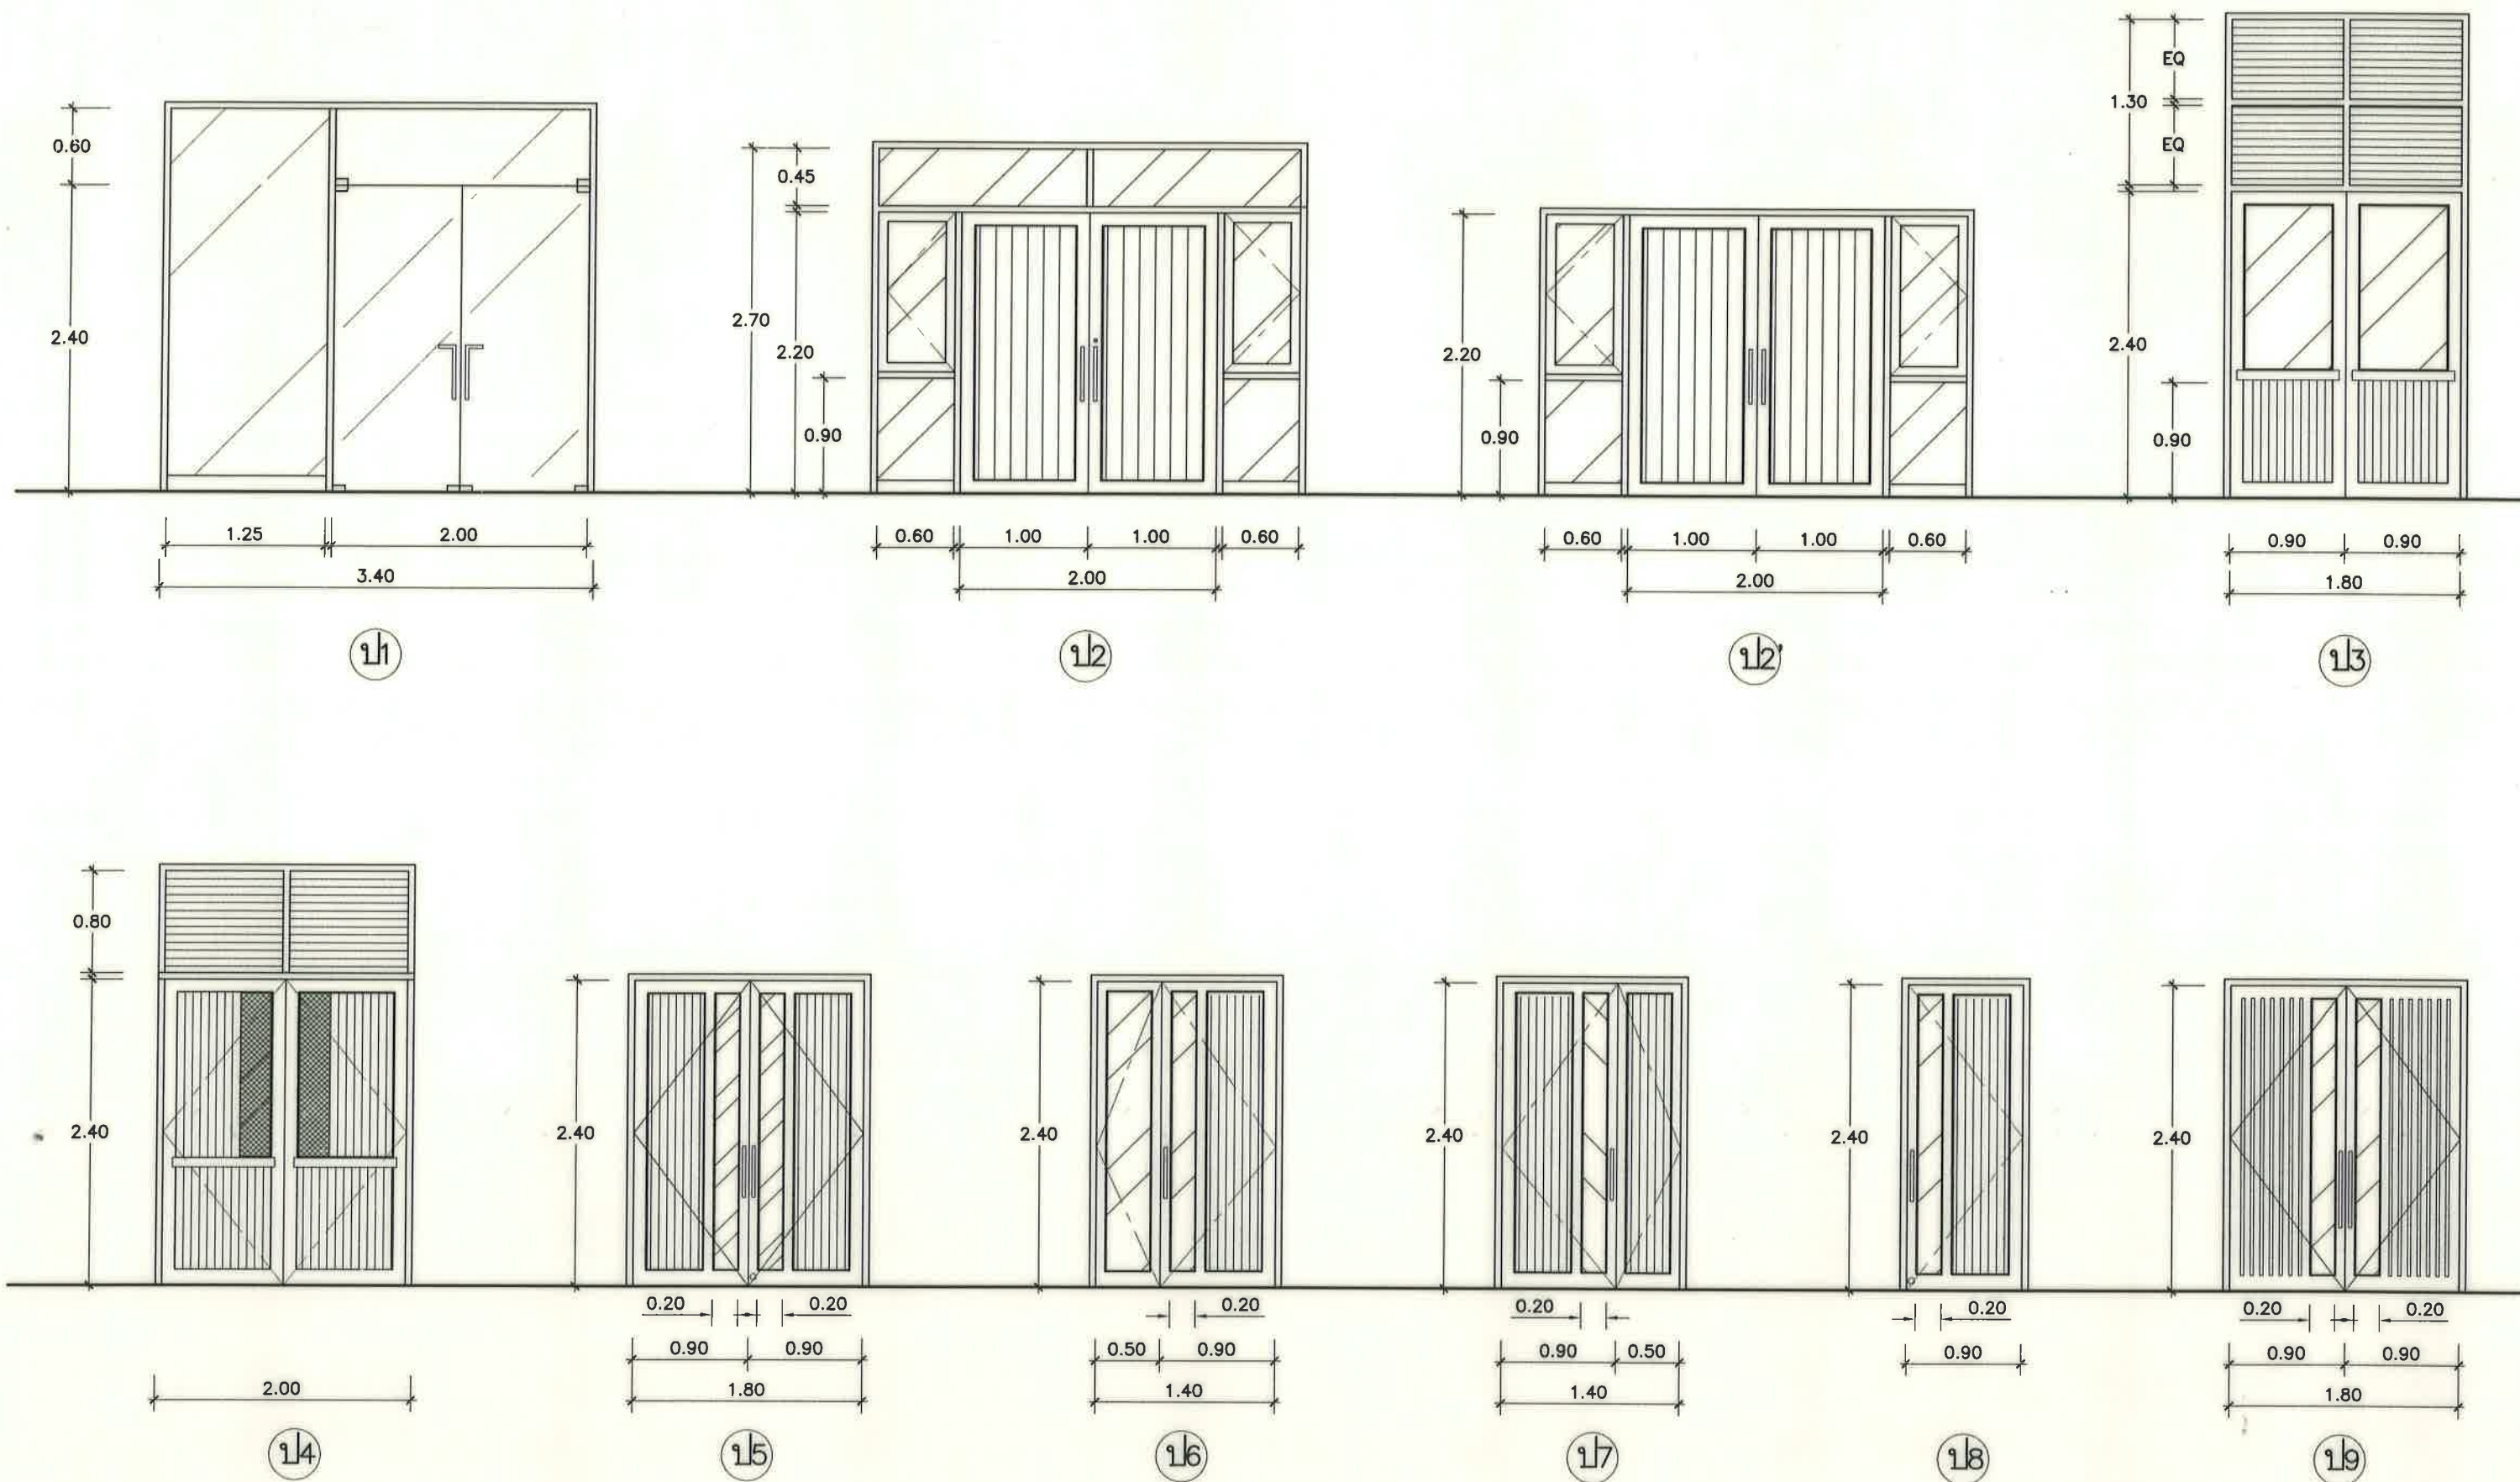


TOT Property Management Department ฝ่ายบริหารทรัพย์สิน ส่วนกองแบบวิศวกรรมอาคาร	เจ้าของโครงการ	ฝ่ายพัฒนาผลิตภัณฑ์ระหว่างประเทศ	สถาปนิก	สนั่น นาคนิกร ๓-๕๓๙๖๑๙	วิศวกรระบบไฟฟ้ากำลัง	เฉลิมชัย พงษ์พานิช ๓๖๒๕	วิศวกรระบบป้องกันอัคคีภัย	ประทีป อินทรศักดิ์ ๓๖๓๗	ตรวจ	วิมลพร/พิทยามาต ๑๖.๐๖/๕๓	เลขที่แบบ	A-20
	แบบ	งานจ้างเหมาก่อสร้างอาคารสถานีโครงการเคเบิลไต่เขา ปากบารา	วิศวกรโครงสร้าง	เอกสิทธิ์ จิงขจรเกียรติ ๕๕๕๗๗๘	วิศวกรระบบควบคุมอัตโนมัติ	พงษ์ศักดิ์ บุญทวี ๓๖๓๕๗๔	วิศวกรระบบดับเพลิงอัตโนมัติ	ปรีชา เหมมัน ๓๓๓๐๑๔	เห็นชอบ	พิระ มาประเสริฐ ๑๖.๐๖/๕๓	แผ่นที่/รวม	20/49
	แสดง	มาตราส่วน 1:50	วิศวกรระบบสุขาภิบาล	เฉลิมพล อุดมย์นคร ๓๒๑๐๓๕	วิศวกรระบบสื่อสารสัญญาณ	ปานทิพย์ พูนผล	วิศวกรระบบปรับอากาศ	สุมิตร ศรีวิพัฒน์ ๓๓๑๐๖๖๖	อนุมัติ	รุชชาติ ขวัญ ๑๗.๐๖/๕๓		
	แบบขยายประตู ป๑-๑๒	เขียน	สนั่น นาคนิกร									

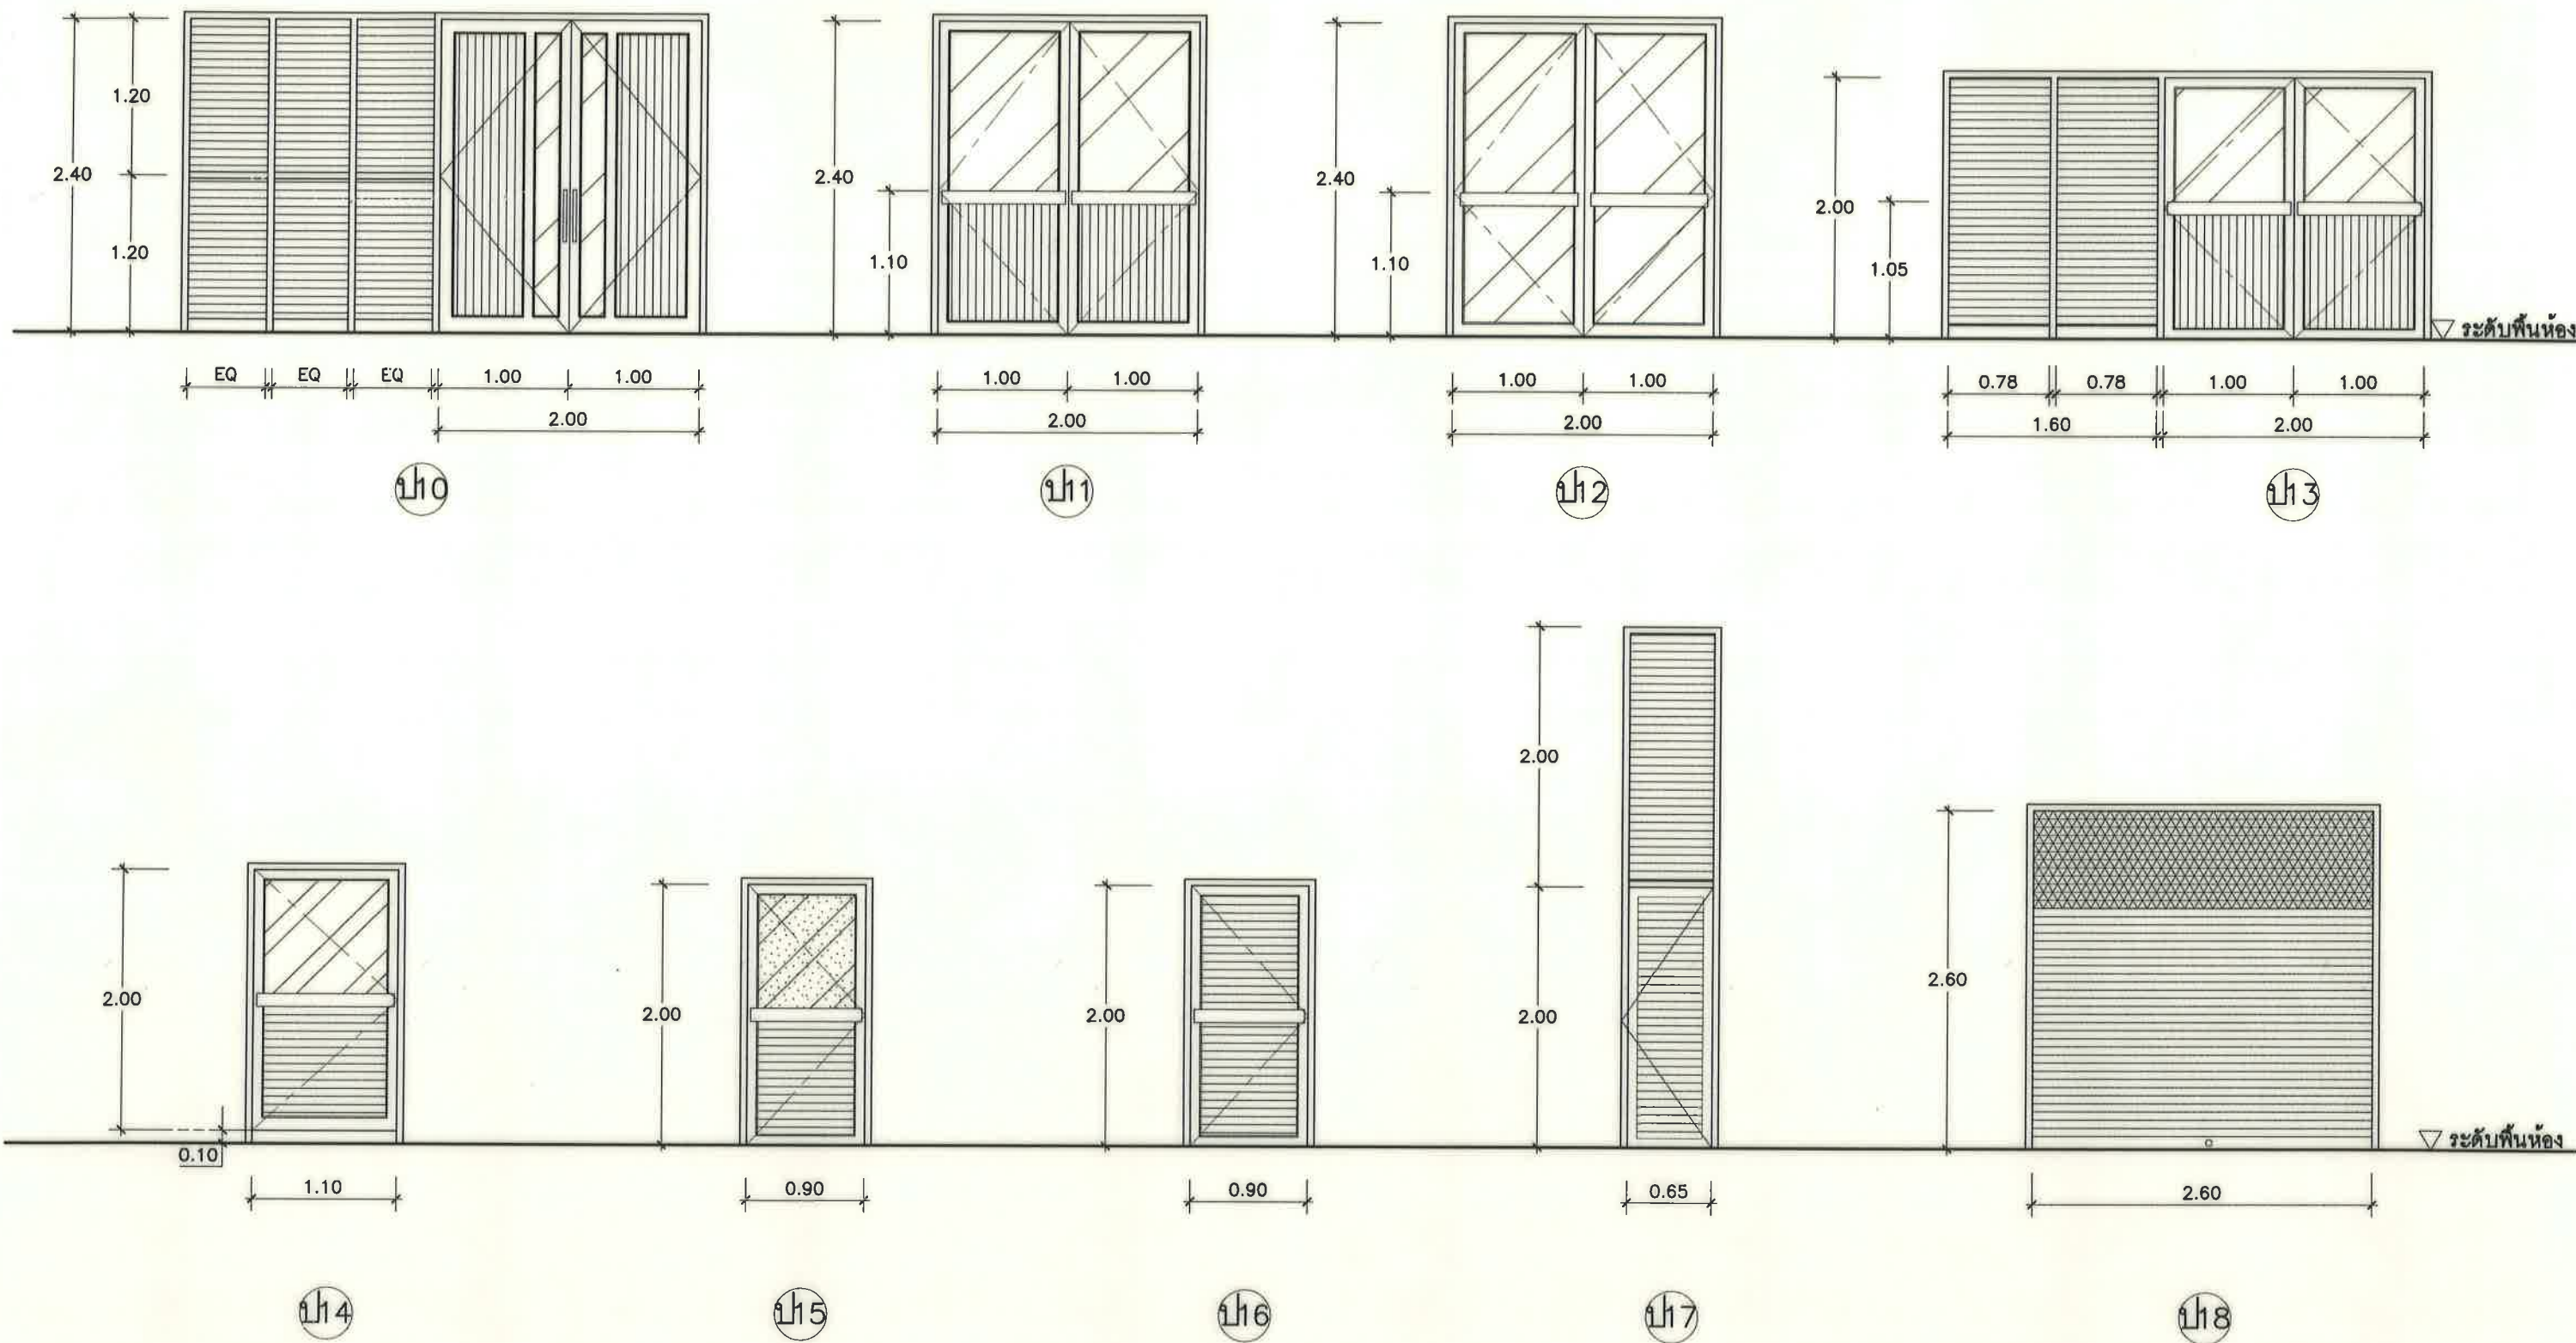


	เจ้าของโครงการ	ฝ่ายพัฒนาผลิตภัณฑ์ระหว่างประเทศ	สถาปนิก	สนั่น นาคนิกร ภา-สธ9619	วิศวกรระบบไฟฟ้ากำลัง	เฉลิมชัย พงษ์พานิช ภาทก 6625	วิศวกรระบบป้องกันอัคคีภัย	ประทีป อินทรศักดิ์ ภาทล 6707	ตรวจ	วิรัช วัฒนวิทย์ ภาทล 57	เลขที่แบบ	A-21
	แบบ	งานจ้างเนกอกสร้างอาคารสถานีโครงการเคเบิลไต่หน้า ปากบารา	วิศวกรโครงสร้าง	เอกสิทธิ์ จิระจวนเกียรติ สธ5778	วิศวกรระบบควบคุมอัตโนมัติ	พงษ์ศักดิ์ บุญทวี ภาทก 5874	วิศวกรระบบดับเพลิงอัตโนมัติ	ปรีชา เหมมัน สก.3014	เห็นชอบ	พิระ มาประเสริฐ ภาทล 57	แผ่นที่/รวม	21/49
	แสดง	มาตรฐาน 1: 50	วิศวกรระบบสุขาภิบาล	เฉลิมพล อุดยัมพร ภาท 21035	วิศวกรระบบสื่อสารสัญญาณ	ปานทิพย์ พูนผล	วิศวกรระบบปรับอากาศ	สุมิตร ศรีวิวัฒน์ ภาท10666	อนุมัติ	บุชาติ ช่าง ภาท 57		
	แบบขยายประตู ปา10-ปา8	เขียน	สนั่น นาคนิกร									

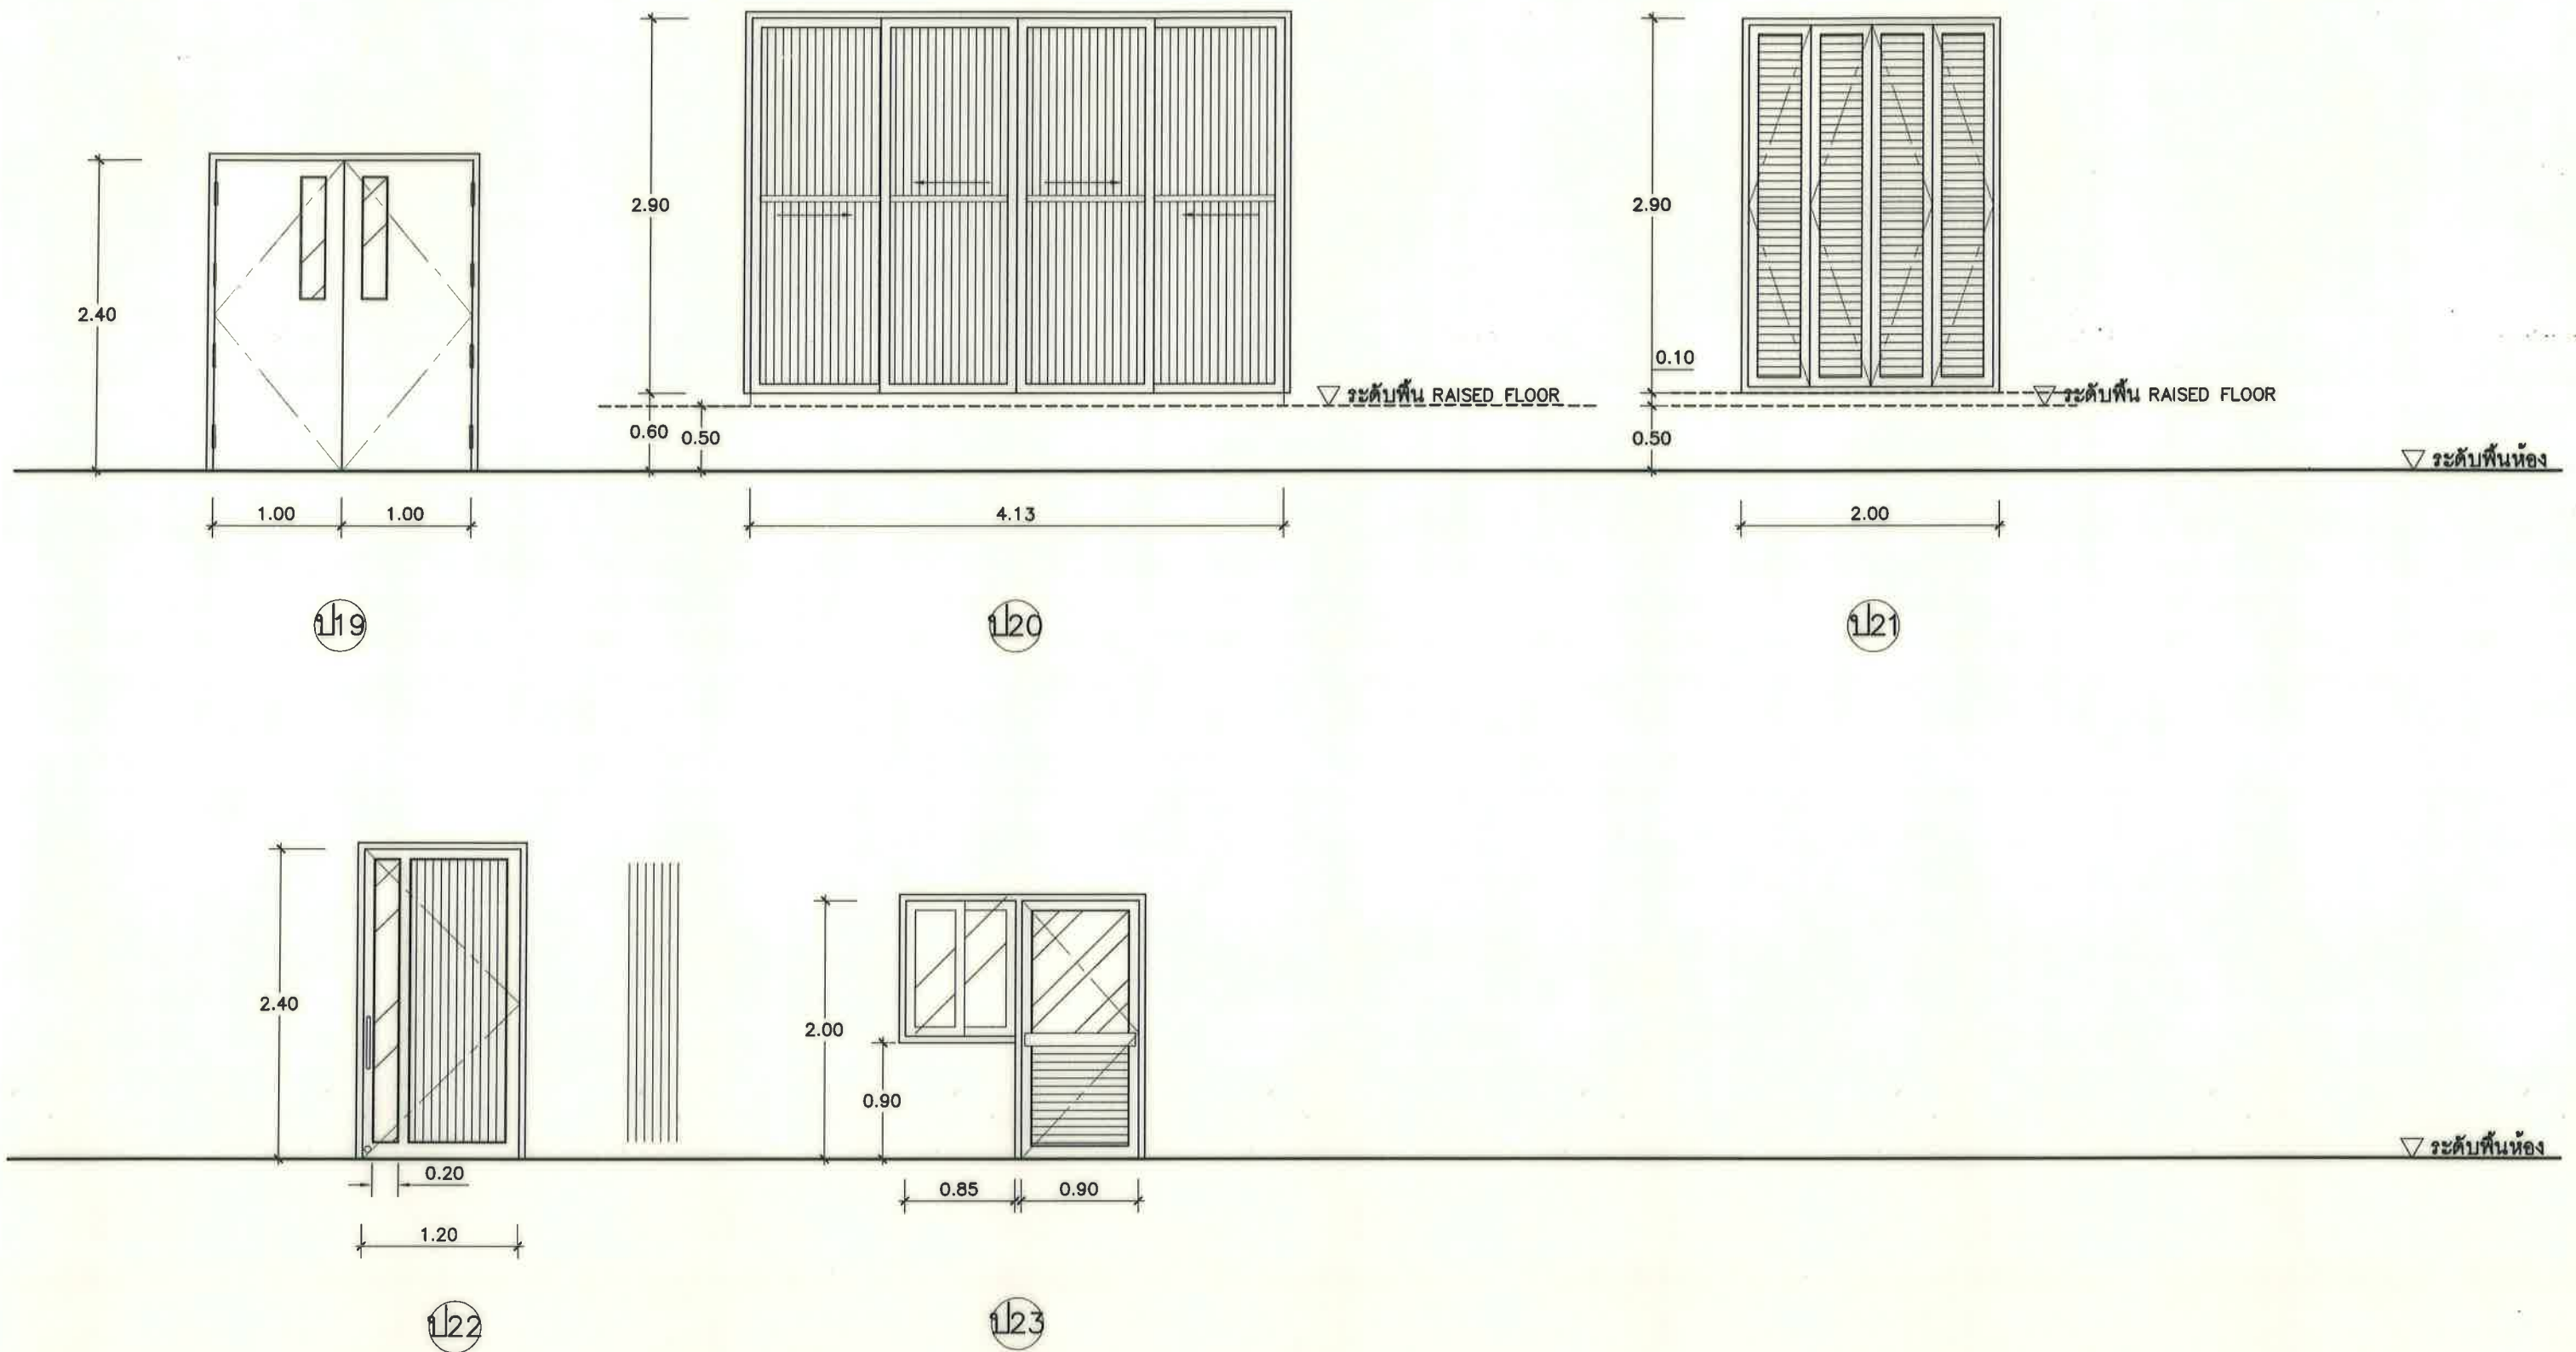

 Property Management Department ฝ่ายบริหารทรัพย์สิน ส่วนอาคารและวิศวกรรมอาคาร	เจ้าของโครงการ	ฝ่ายพัฒนาผลิตภัณฑ์ระหว่างประเทศ	สถาปนิก	สนั่น นาคนิกร ๓-๕๙๙๖๑๙	วิศวกรระบบไฟฟ้ากำลัง	เฉลิมชัย พงศ์ชากร ๓๗๓ ๖๖๒๕	วิศวกรระบบป้องกันอัคคีภัย	ประทีป อินทรศักดิ์ ๓๗๓ ๖๗๐๗	ตรวจ	วิมล ๒๖/๕๖	เลขที่แบบ	A-22
	แบบ	งานจ้างเหมาก่อสร้างอาคารสถานที่โครงการขายเคเบิลทีวี ปากบารา	วิศวกรโครงสร้าง	เอกสิทธิ์ จิระขจรเกียรติ ๕๕๕๗๗๘	วิศวกรระบบควบคุมอัตโนมัติ	พงษ์ศักดิ์ บุญทวี ๓๗๓ ๕๘๗๔	วิศวกรระบบดับเพลิงอัตโนมัติ	ปรีชา เหมฝัน ๓๓๓ ๓๐๑๔	เห็นชอบ	๒๖/๕๖	แผ่นที่/รวม	22/49
	แสดง	มาตรฐาน 1:50	วิศวกรระบบสุขาภิบาล	เฉลิมพล อดุลย์บุตร ๓๗๓ ๒๑๐๓๕	วิศวกรระบบสื่อสารสัญญาณ	ปานทิพย์ พูนผล	วิศวกรระบบปรับอากาศ	สุมิตร ศรีวิวัฒน์ ๓๓๓ ๑๐๖๖๖	อนุมัติ	๒๖/๕๖		
	แบบขยายประตู ป๑-๒๓	เขียน	สนั่น นาคนิกร									

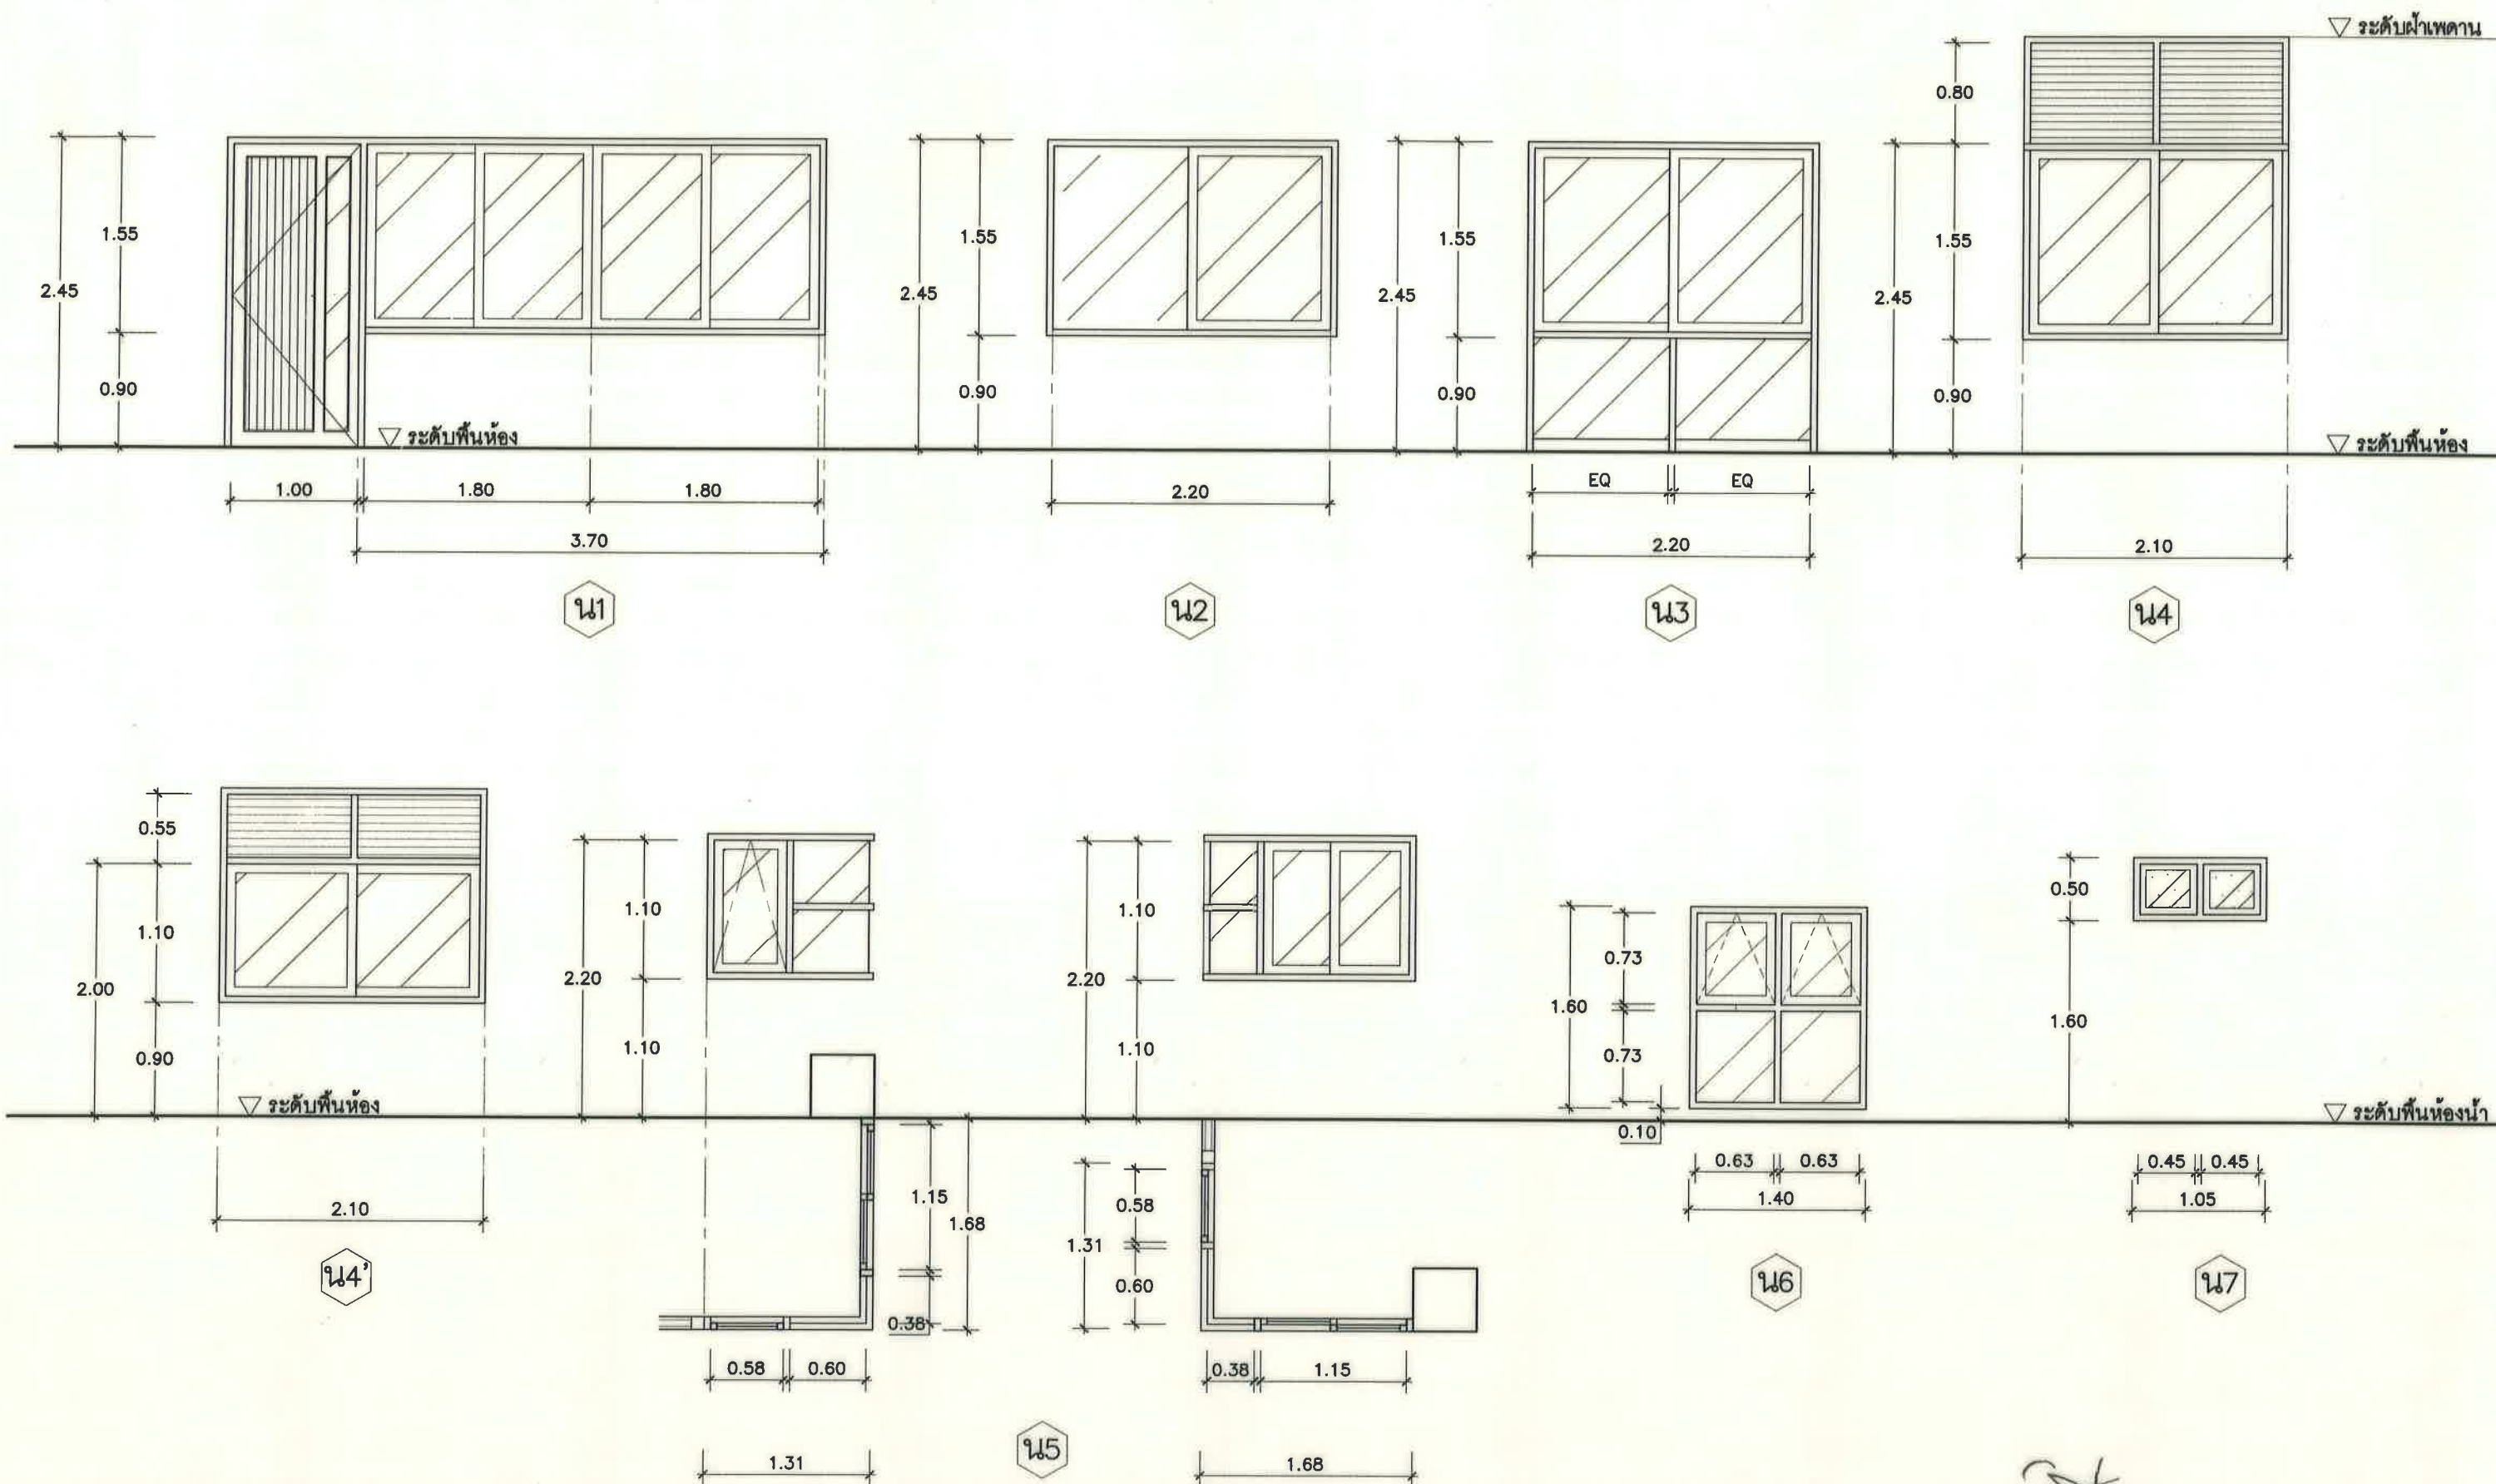

TOT Property Management Department ฝ่ายบริหารทรัพย์สิน ส่วนอาคารและวิศวกรรมอาคาร	เจ้าของโครงการ	ฝ่ายพัฒนาผลิตภัณฑ์ระหว่างประเทศ	สถาปนิก	สนั่น นาคนิกร ๙-๘๙๙๖๑๙	วิศวกรระบบไฟฟ้ากำลัง	เฉลิมชัย พงษ์พานิช ๙๖๒๕	วิศวกรระบบป้องกันอัคคีภัย	ประทีป อินทพงศ์ ๙๖๐๗	ตรวจสอบ	18.๐๐/๕๓	เลขที่แบบ	A-23
	แบบ	งานจ้างเหมาก่อสร้างอาคารสถานีโครงการเคเบิลไต่หน้า ปากบารา	วิศวกรโครงสร้าง	เอกสิทธิ์ จังจรรย์เกียรติ ๘๙๕๗๗๘	จรรยา งามวิสุทธิคุณ ๙๖๓๐๙	วิศวกรระบบควบคุมอัตโนมัติ	วิชา งามมัน ๘๙๓๐๑๔	เห็นชอบ	18.๐๐/๕๓	ผ.ส.อ.พ.	แผ่นที่/รวม	23/49
	แสดง	มาตราส่วน 1:50	วิศวกรระบบสุขาภิบาล	เฉลิมพล อุดมบุตร ๙๖๒๐๓๕	ปานทิพย์ พูนผล	วิศวกรระบบปรับอากาศ	สุมิตร ศรีพัฒน์ ๙๙๑๐๘๘	อนุมัติ	18.๐๐/๕๓	ผ.จ.ท.พ.		
	แบบขยายหน้าต่าง น1-น7	เขียน	สนั่น นาคนิกร									

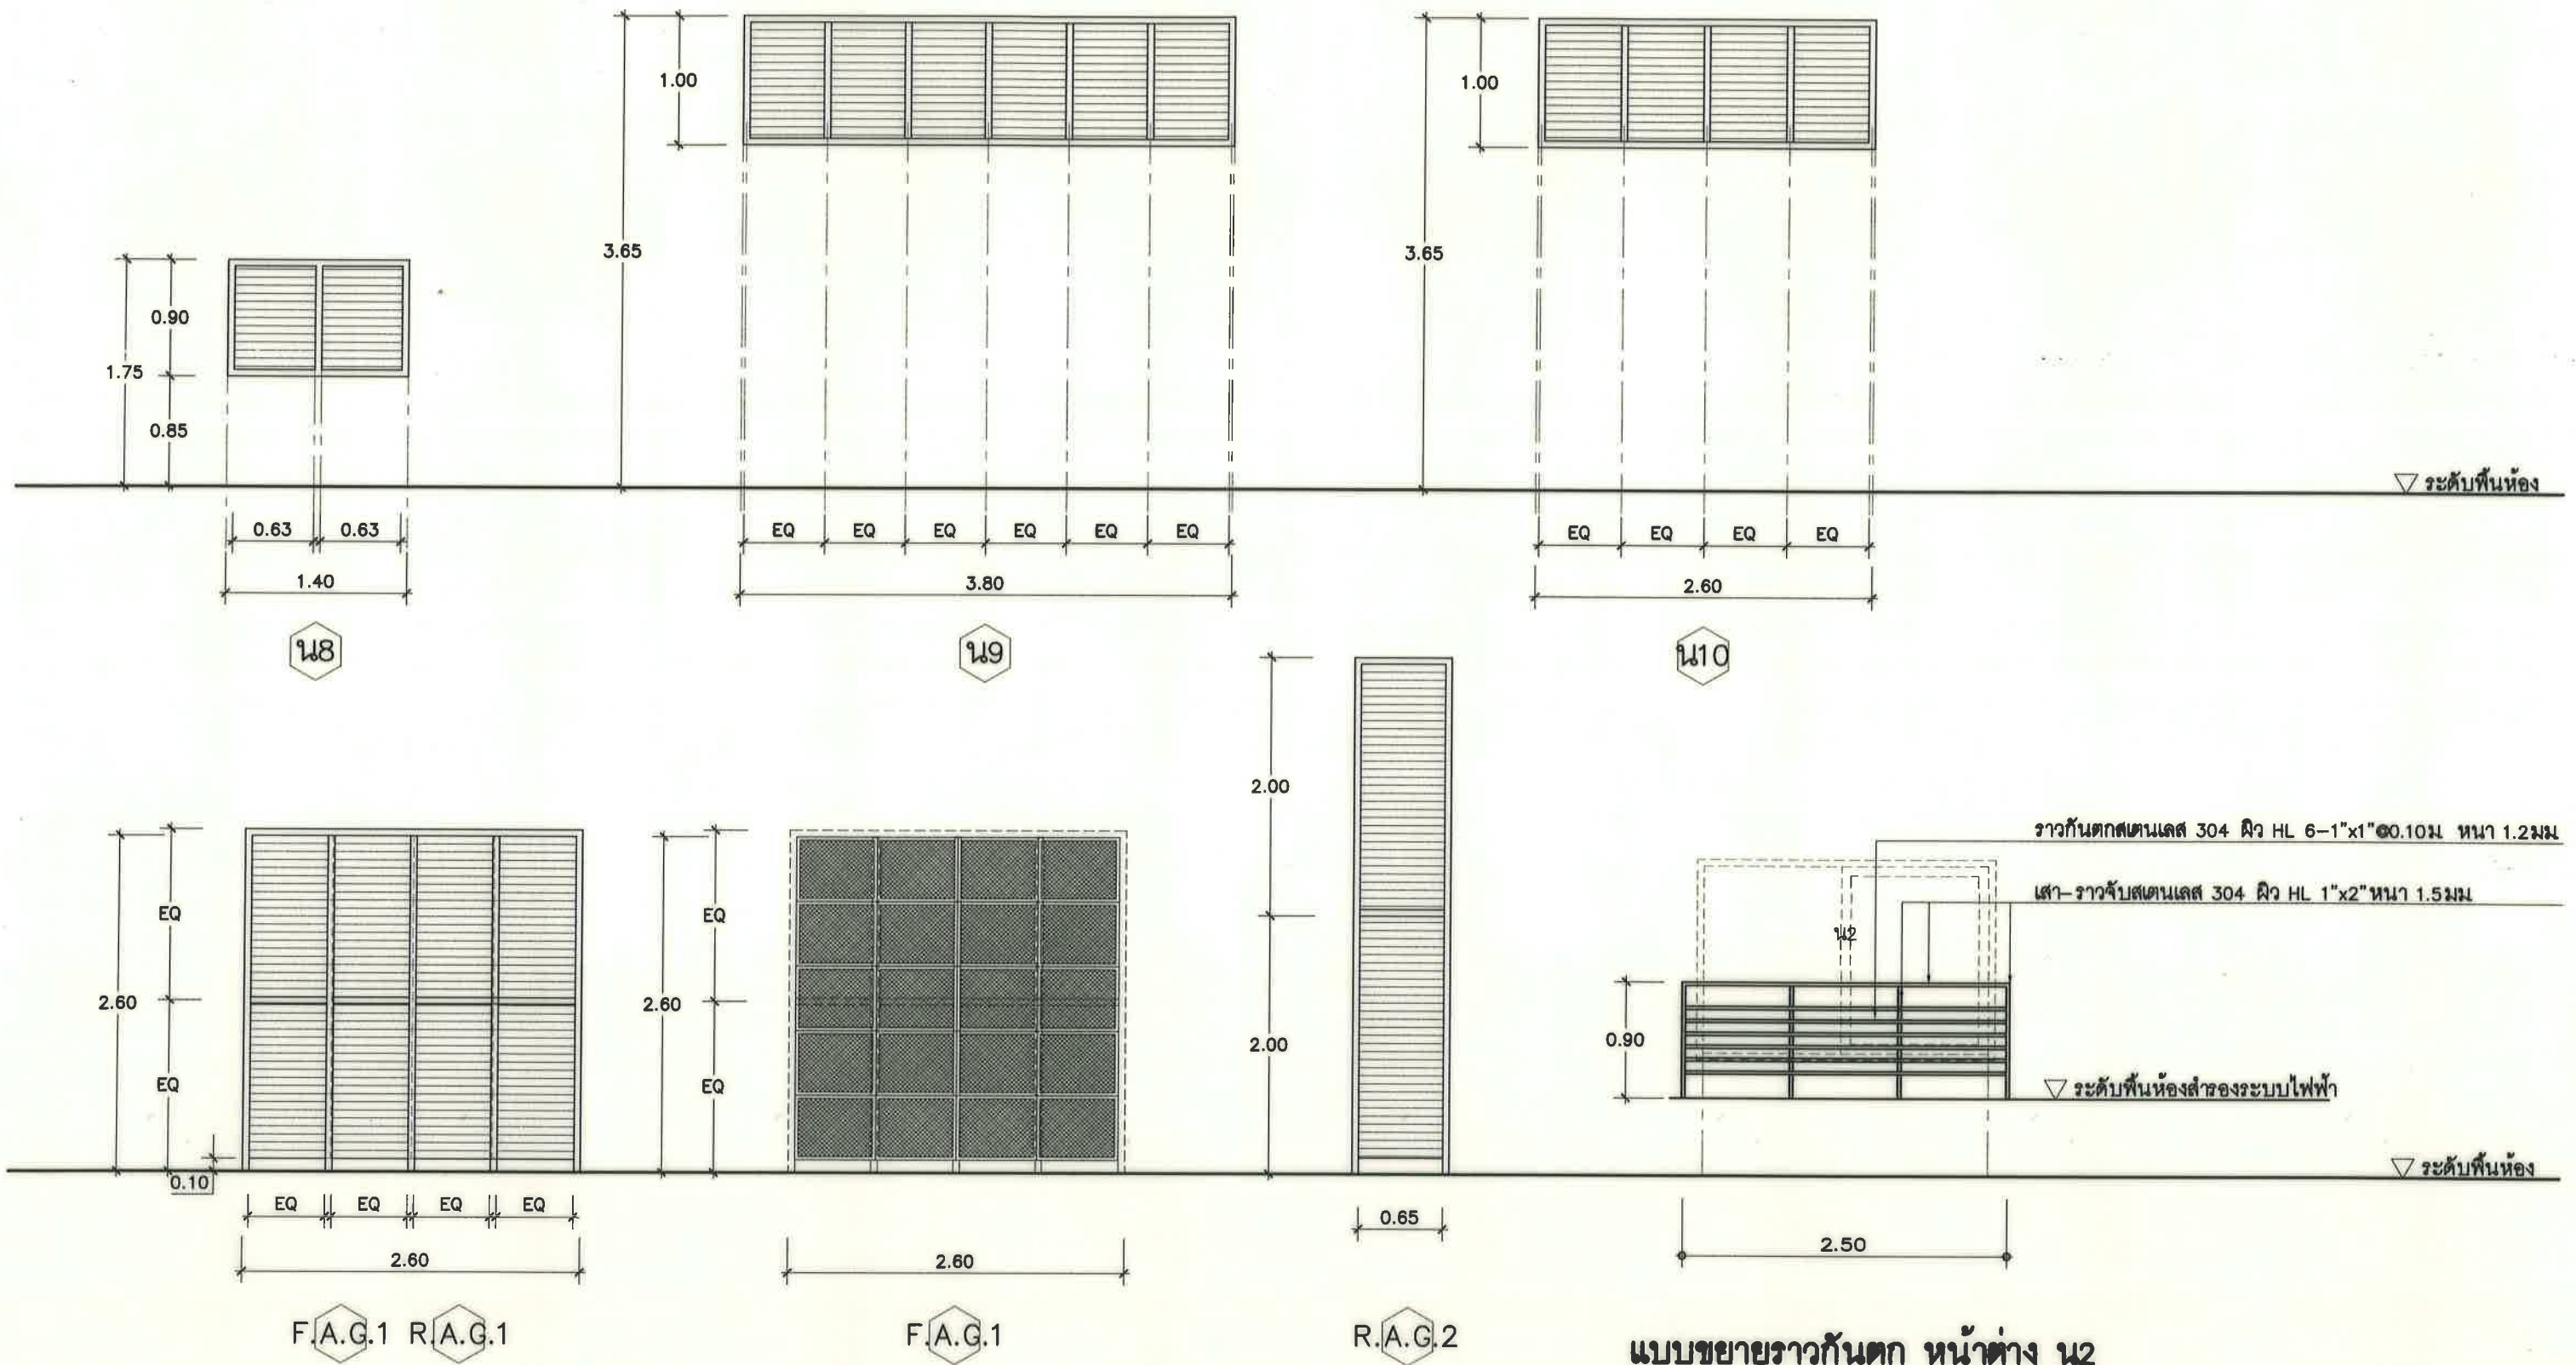


แบบขยายราวกันตก หน้าต่าง น2

มาตราส่วน


1 : 50

เฉพาะห้องสำหรับระบบไฟฟ้า ชั้น 3

TOT Property Management Department ฝ่ายบริหารทรัพย์สิน ส่วนอาคารและวิศวกรรมอาคาร	เจ้าของโครงการ	ฝ่ายพัฒนาผลิตภัณฑ์ระหว่างประเทศ	สถาปนิก	สนั่น นาคนิกร ๓-๓๑๑๖19	วิศวกรระบบไฟฟ้ากำลัง	เฉลิมชัย พงษ์ชากร ภพ ๑๑๒๕	วิศวกรระบบป้องกันอัคคีภัย	ประทีป อินทศักดิ์ ภพ ๑๗๐๗	ตรวจ	วิมลรัตน์/พิพัฒน์	ผจ.สอ.ทพ.	เลขที่แบบ
	แบบ	งานจ้างเหมาก่อสร้างอาคารพาณิชย์โครงการศูนย์การค้าปิ่นเกล้า	วิศวกรโครงสร้าง	เอกสิทธิ์ ชิงขจรเกียรติ สย ๕๗๗๘	วิศวกรระบบควบคุมอัตโนมัติ	พงษ์ศักดิ์ บุญทวี ภพ ๕๑๗๔	วิศวกรระบบดับเพลิงอัตโนมัติ	ปรีชา เหมมัน สก ๓๐๑๔	เห็นชอบ	ปิระ มาประเสริฐ	ผส.อ.ทพ.	A-24
	แสดง	แบบขยายหน้าต่าง น8-น10	มาตราส่วน	1: 50	วิศวกรระบบสุขาภิบาล	เฉลิมพล อุดลย์พร ภย ๒๑๐๓๕	วิศวกรระบบปรับอากาศ	สุวิทย์ ศรีวิวัฒน์ ภก ๑๐๑๑๕	อนุมัติ	รุชดา ช่าง	ผจ.ทพ.	แผ่นที่/รวม
		FAG.1, 2 RAG.1, 2	เขียน	สนั่น นาคนิกร								24/49

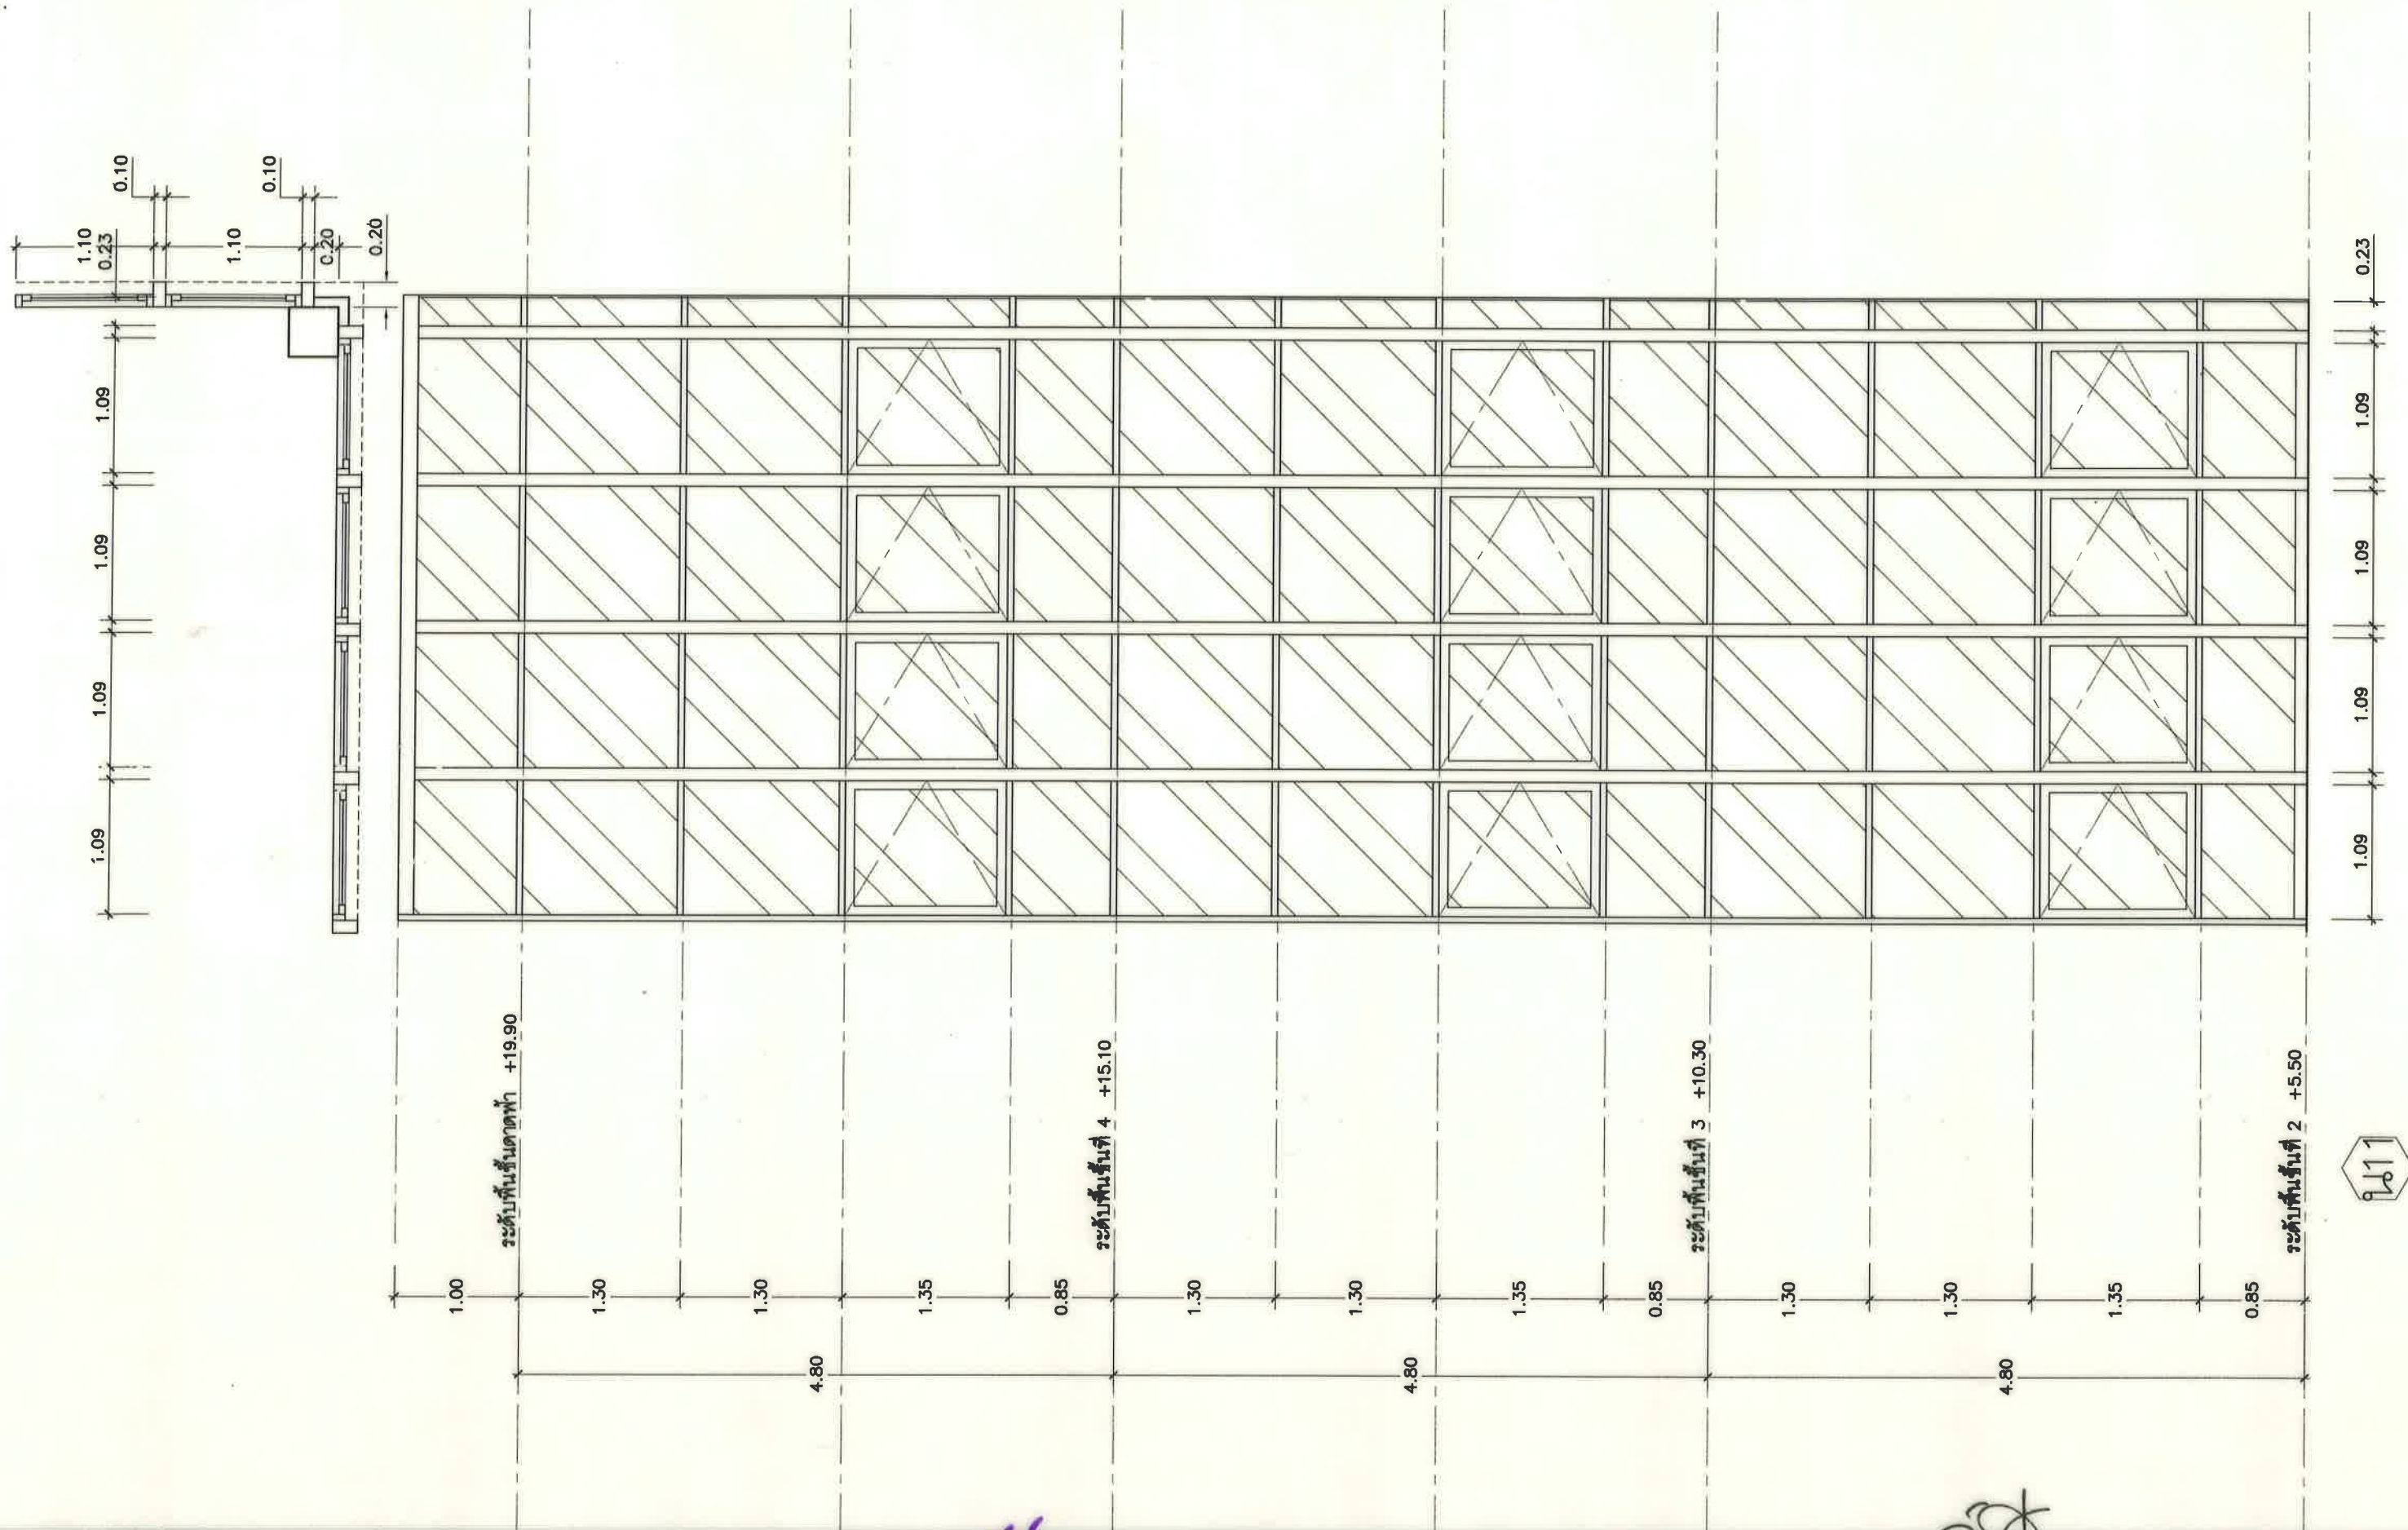


TOT Property Management Department ฝ่ายบริหารทรัพย์สิน ส่วนออกใบบิลค่ากรรมอาคาร	เจ้าของโครงการ ฝ่ายพัฒนาผลิตภัณฑ์ระหว่างประเทศ		สถาปนิก สนั่น นาคนิก ๓-๘๘๑๖๑๙	วิศวกรระบบไฟฟ้ากำลัง เฉลิมชัย พุดชากร ๓๒๒๕ จิระชาย เจริญสุขคุณ ๓๒๓๐๙	วิศวกรระบบป้องกันอัคคีภัย ประทีป อินทรศักดิ์ ๓๒๓๐๗	ตรวจ วิฑูรย์ ทรัพย์มาศ ๓๒๓๐๗	เลขที่แบบ
	แบบ งานจ้างเหมาก่อสร้างอาคารพาณิชย์โครงการศูนย์การค้าปิ่นเกล้า		วิศวกรโครงสร้าง เอกสิทธิ์ จิระเกียรติ ๓๒๕๗๗๘	วิศวกรระบบควบคุมอัตโนมัติ พงษ์ศักดิ์ บุญทวี ๓๒๓๕๗๔	วิศวกรระบบดับเพลิงอัตโนมัติ ปรีชา เหมมัน ๓๒๓๐๑๔	เห็นชอบ ปิยะ มาประเสริฐ ๓๒๓๐๗	A-25
	แสดง แบบขยายผนังกระจก		วิศวกรระบบสุขาภิบาล เฉลิมพล อุดมบุตร ๓๒๓๐๓๕	วิศวกรระบบสื่อสารสัญญาณ ปานทิพย์ พูนผล	วิศวกรระบบปรับอากาศ สุเมธ ศรีวิวัฒน์ ๓๒๓๐๖๖	อนุมัติ สุชาติ ชัยสุข ๓๒๓๐๗	แผ่นที่/รวม
	มาตราส่วน		เขียน สนั่น นาคนิก			25/49	

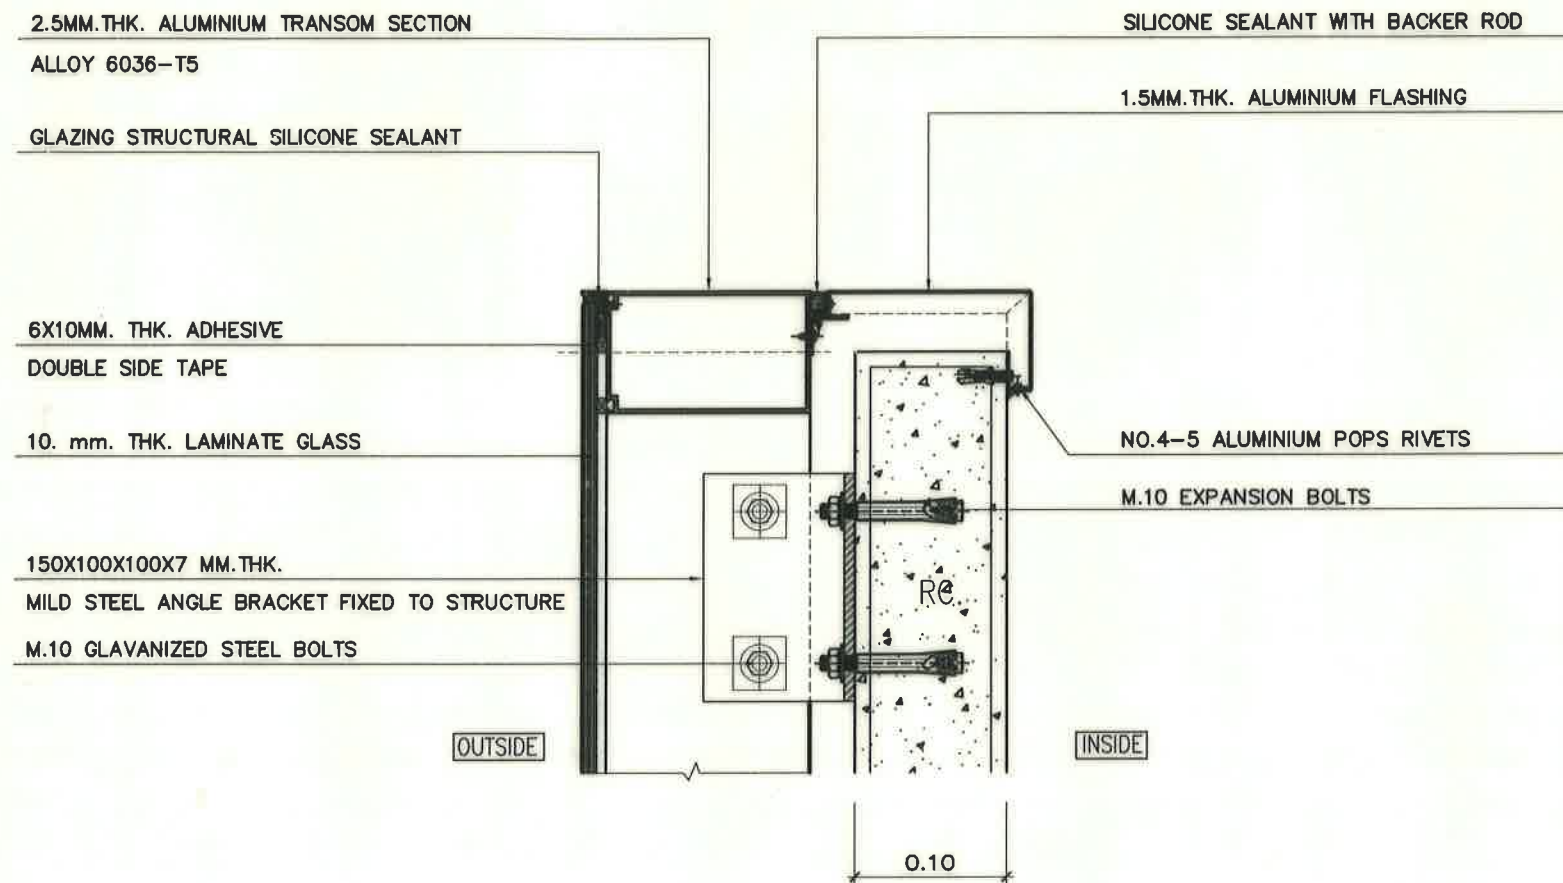


VERTICAL DETAIL

SCALE 1 : 5

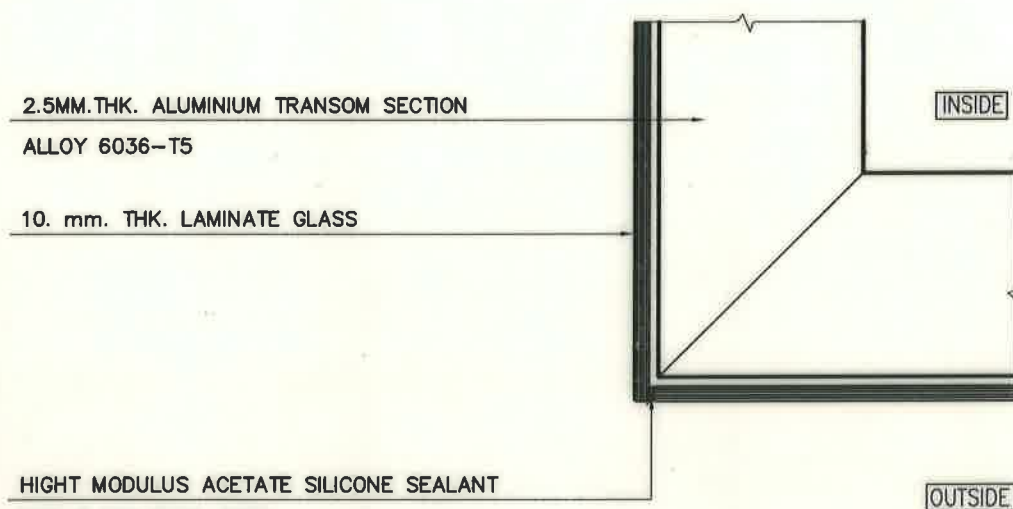


HORIZONTAL DETAIL

SCALE 1 : 10

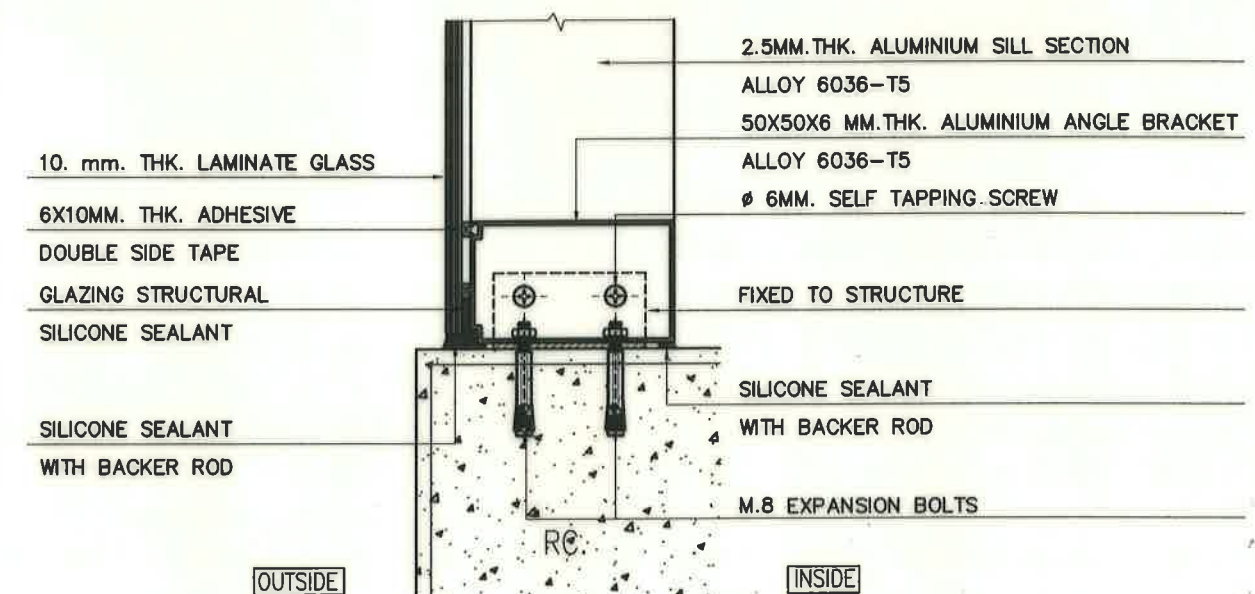

VERTICAL DETAIL

SCALE 1 : 5

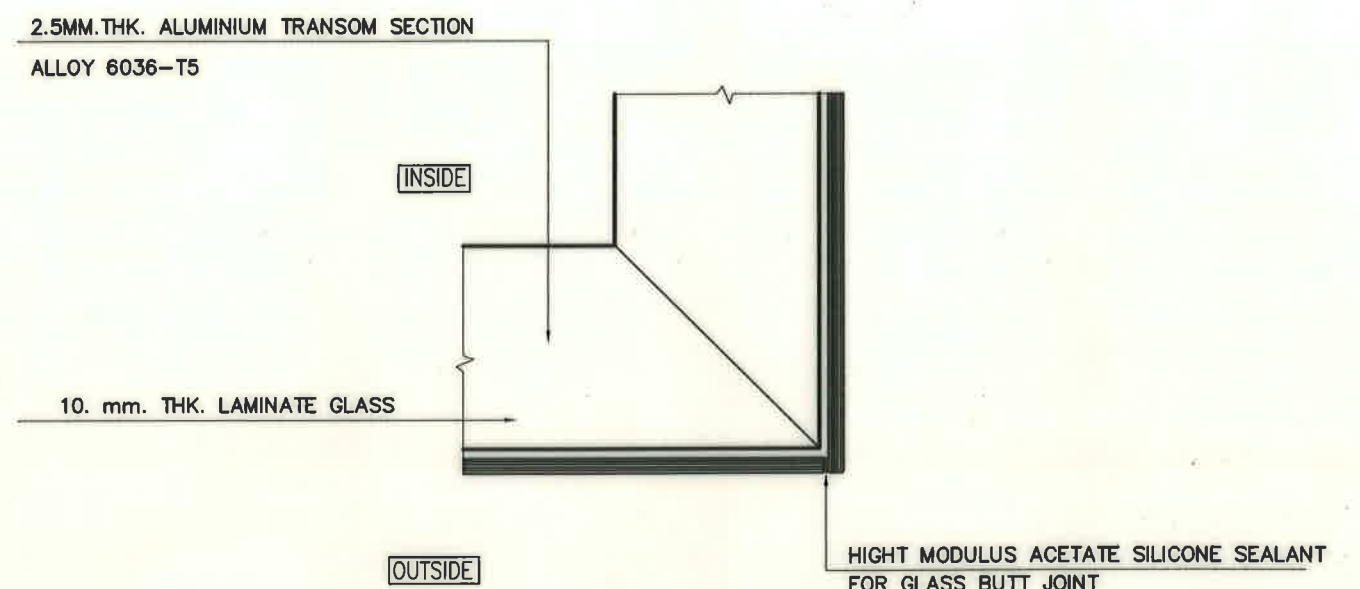

HORIZONTAL DETAIL

SCALE 1 : 10

TOT Property Management Department ฝ่ายบริหารทรัพย์สิน ส่วนอาคารและวิศวกรรมอาคาร	เจ้าของโครงการ	ฝ่ายพัฒนาผลิตภัณฑ์ระหว่างประเทศ	สถาปนิก	สนั่น นาคนิกร ภา-๓๑๙๖๑๙	วิศวกรระบบไฟฟ้ากำลัง	เฉลิมชัย พงษ์พานิช ภาฟก ๖๖๒๕	วิศวกรระบบป้องกันอัคคีภัย	ประทีป อินทพรศักดิ์ ภาฟค ๖๗๐๗	ตรวจ	วิมลพร วัฒนวิทย์ ภาฟค ๖๖๖๖	เลขที่แบบ	A-26
	แบบ	งานจ้างเหมาก่อสร้างอาคารสำนักงานโครงการศูนย์บริการลูกค้า	วิศวกรโครงสร้าง	เอกสิทธิ์ จันทะนัยรัตน์ สย๕๗๗๘	วิศวกรระบบควบคุมอัตโนมัติ	พงษ์ศักดิ์ บุญทวี ภาฟค ๕๘๗๔	วิศวกรระบบดับเพลิงอัตโนมัติ	ปวิชา เหมมื่น สก๓๐๑๔	เห็นชอบ	วิมลพร วัฒนวิทย์ ภาฟค ๖๖๖๖	แผ่นที่/รวม	26/49
	แสดง	แบบขยายผนัง กระจาก น11	มาตราส่วน	1 : 10	วิศวกรระบบสุขาภิบาล	เฉลิมพล อุดมย์บวร ภาข ๒๑๐๓๕	วิศวกรระบบปรับอากาศ	สุเมธ ศรีวิวัฒน์ ภาค 10๖๖๕	อนุมัติ	วิมลพร วัฒนวิทย์ ภาฟค ๖๖๖๖		
			เขียน	สนั่น นาคนิกร								

รายการประกอบแบบประตู่

[illegible]

 Property Management Department ฝ่ายบริการทรัพย์สิน ส่วนนอกแบบวิศวกรรมอาคาร	เจ้าของโครงการ ฝ่ายพัฒนาผลิตภัณฑ์ระหว่างประเทศ		สถาปนิก	สนั่น นาคนิกร ภา-สถ.9619	วิศวกรระบบไฟฟ้ากำลัง	เฉลิมชัย พุดชุกร ภาฟ. 6625	วิศวกรระบบป้องกันอัคคีภัย	ประทีป อินทพงศ์ ภาฟ. 6707	ตรวจสอบ	18/10/57	เลขที่แบบ
	แบบ งานจ้างเหมาก่อสร้างอาคารสถานที่โครงการชายเคเบิลใต้ฟ้า ปากบารา อ.ละงู จ.สตูล พร้อมงานติดตั้งระบบปรับอากาศ และงานรื้อถอน		วิศวกรโครงสร้าง	เอกสิทธิ์ จิงขจรเกียรติ สย.5778	วิศวกรระบบควบคุมอัตโนมัติ	พงษ์ศักดิ์ บุญทวี ภาฟ.5874	วิศวกรระบบดับเพลิงอัตโนมัติ	ปิรัช เหมมัน สก.3014	เห็นชอบ	26/10/57	A-27
	แสดง		วิศวกรระบบสุขาภิบาล	เฉลิมพล อุดลย์ภท ทย. 21035	วิศวกรระบบสื่อสารสัญญาณ	ปานทิพย์ พูนผล	วิศวกรระบบปรับอากาศ	สุมิตร ศรีวิพัฒน์ ภาท.10666	อนุมัติ	27/49	แผ่นที่/รวม
	รายการประกอบแบบประตู		เขียน	สนั่น นาคนิกร							

[illegible]


รายการวัสดุอุปกรณ์ประตุ-หน้าต่าง

- | | |
|---|--|
| <ul style="list-style-type: none"> - น11 ให้ผู้รับจ้างเสนอแบบ SHOP DRAWING การติดตั้งผนังกระจกระบบ CURTAIN WALL - FAG.1 พร้อมติดตั้ง FILTER กรองอากาศ ขนาด 20"x25" กรอบอลูมิเนียม และสามารถถอดล้างทำความสะอาดได้ - ป19 ประตูบานเปิดเหล็ก ผลิตจากเหล็ก COLD ROLLED STEEL SHEET ความหนาไม่น้อยกว่า 1.6 มม 2 แผ่นประกอบภายในบุฉนวนกันเสียง ผลิตภัณฑ์ของ สยามประตูเหล็ก, SPR, บ.ไทยโรลลิ่ง ชัตเตอร์ จก หรือเทียบเท่า - RAG.2 และ ป18 พร้อมติดตั้ง ตะแกรงกันนก แอนตี้-เบิร์ด เน็ต (Anti-Bird Net) ขนาดช่องไม่มากกว่า 15 มม - ประตูม้วนแบบโปร่ง(ชนิดใช้มือดึง) ผู้ผลิต SPR, บ.ไทยโรลลิ่ง ชัตเตอร์ จก , SMC, VARINPORNSHUTTER หรือเทียบเท่า - ประตูไม้อัดแน่นเรียบ, ประตูแผ่นไม้ประกอบ(ไม้อัดสำเร็จรูป) ผู้ผลิตวิสตู ตราช้าง 3 เชือก, บ.ไม้อัดไทย จก , สยามวู้ด หรือเทียบเท่า | <ul style="list-style-type: none"> - กลอนชนิดฝังเรียบเสมอลิวนาน ผลิตภัณฑ์ HAFELE, PENTACO, VVP, COLT หรือเทียบเท่า - ญุญแจก้านบิด ผลิตภัณฑ์ HAFELE, PENTACO, VVP, COLT หรือเทียบเท่า - ญุญแจฝังบาน(สำหรับประตูบานเลื่อน, บานเปิดทางเดียว, บานเปิดสองทาง ผลิตภัณฑ์ HAFELE, LOUIS, VVP, COMMY หรือเทียบเท่า - ญุญแจลูกบิด ผลิตภัณฑ์ HAFELE, VVP, SKUL THAI LOCK ,YALE หรือเทียบเท่า - ขอรับ- ขอสับ มือจับ, DOOR STOP ผลิตภัณฑ์ HAFELE, PENTACO, VVP, COLT หรือเทียบเท่า - DOOR CLOSE ,บานพับฝังพื้นและบานพับปรับมุมชนิดฝัง ผลิตภัณฑ์ HAFELE, DORMA, PENTACO, VVP, หรือเทียบเท่า - บานพับสองปีก ผลิตภัณฑ์ VVP, COLT, PENTACO, หรือเทียบเท่า - อุปกรณ์มือจับบานเลื่อน, บานสวิง ผลิตภัณฑ์ HAFELE, RELIANCE, VVP, COLT หรือเทียบเท่า |
|---|--|

 TOT Property Management Department ฝ่ายบริหารทรัพย์สิน ส่วนอาคารและวิศวกรรมอาคาร	เจ้าของโครงการ	ฝ่ายพัฒนาผลิตภัณฑ์ระหว่างประเทศ	สถาปนิก	สนั่น นาคนิค ภ-สด9619	วิศวกรระบบไฟฟ้ากำลัง	เฉลิมชัย พุกษาการ ภพท 8625 จิระชาย เวชวิสุทธิคุณ ภพท 19309	วิศวกรระบบป้องกันอัคคีภัย	ประทีป อินทรศักดิ์ ภพท 6707	ตรวจ	ธีรพงศ์ ทักษิณมาศ	ผจ.สอพท. กษ. อาภ.52	เลขที่แบบ	A-28
	แบบ	งานจ้างเหมาก่อสร้างอาคารสถานที่โครงการเคอเนลไดโนเสาร์ ปาชาวรา อสังหาริมทรัพย์ จ.สตูล พร้อมงานติดตั้งระบบปรับอากาศ และงานร้อยท่อ	วิศวกรโครงสร้าง	เอกสิทธิ์ จึงขจรเกียรติ สย5778	วิศวกรระบบควบคุมอัตโนมัติ	พงษ์ศักดิ์ บุญทวี ภพท.5874	วิศวกรระดับเพลิงอัตโนมัติ	ปรัชญา เหมมัน สก.3014	เห็นชอบ	กฤษ มาประเสริฐ	ผจ.สอพท. 26.ธ.บ.57	แผ่นที่/รวม	
	แสดง	มาตราสวน	วิศวกรระบบสุขาภิบาล	เฉลิมพล อุตุย์บุตร รยก 21035	วิศวกรระบบสื่อสารสัญญาณ	ปานทิพย์ พูนผล	วิศวกรระบบปรับอากาศ	สุมิตร ศรีวัฒน ภท.10666	อนุมัติ	ชูชาติ ช้วย	ผจ.ทพ. 27.ธ.บ.57		28/49
	รายการประกอบแบบหน้าต่าง		เขียน	สนั่น นาคนิค									


32/358

ขอบบันไดคสล หนา 0.10 ม. ฉาบปูนเรียบทาสี
พื้นบันได คสล ผิวปูนขัดมัน รั้วรูปพร้อมขัดเคลือบผิว
จุกบันไดอลูมิเนียมสอดแน่นยางกันลื่น ผิวสี 3 เส้น กว้าง 2"

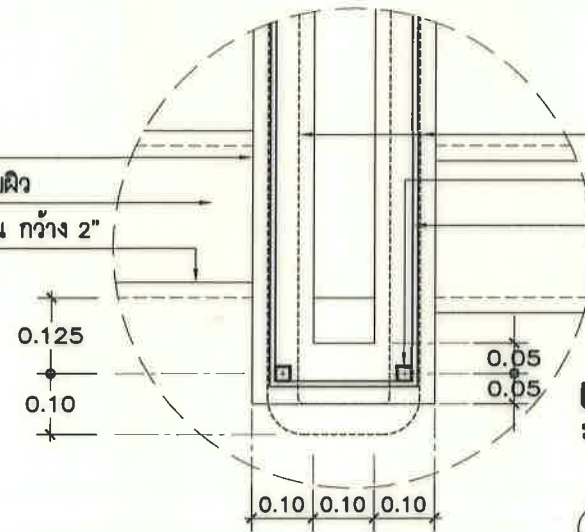


เส้นประราวบันไดสแตนเลส ๑ 2" หนา มม. ผิวขัดด้าน
ลูกกรงราวกันตกท่อสแตนเลส 304 ผิว HL ๕3/8"x3/8"
ลูกกรงราวกันตกท่อสแตนเลส 304 ผิว HL ๕3/8"x3/8"
หนา 1 มม. ๑ 0.0725 ม. 4 เส้น


แบบขยาย ①
มาตราส่วน 1 : 12.5

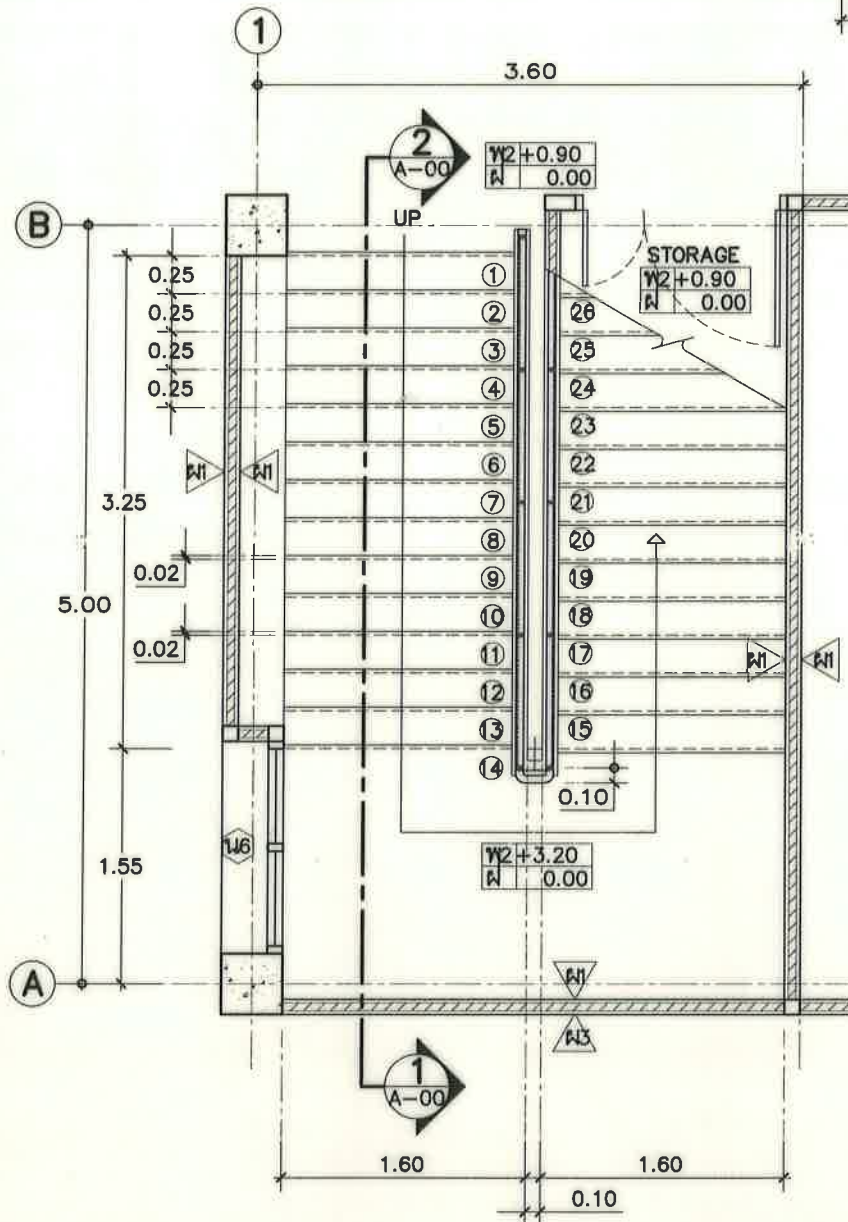

แปลนขยายบันไดชั้น 1 ST-2
มาตราส่วน 1 : 50

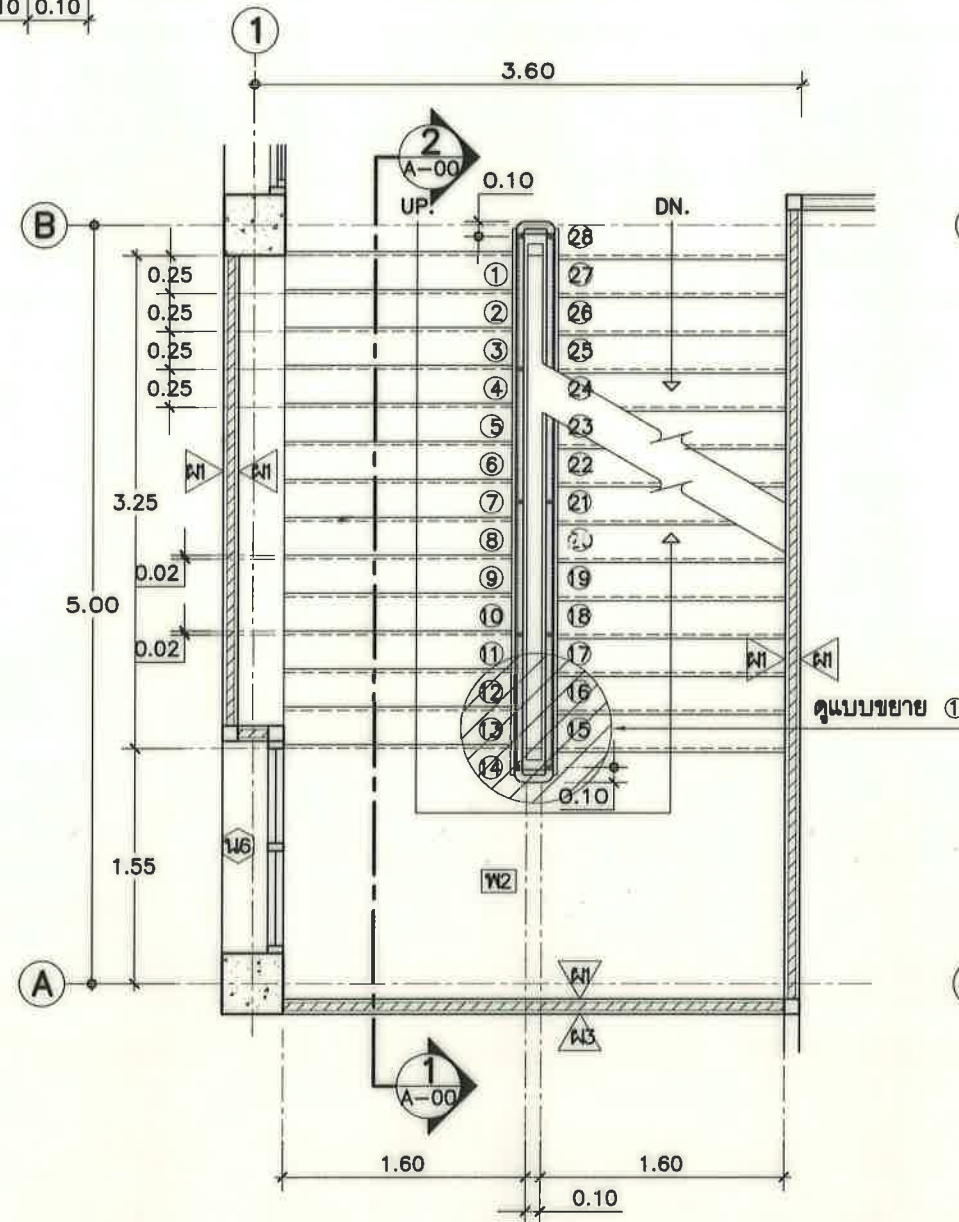


แปลนขยายบันไดชั้น 2-4 ST-2
มาตราส่วน 1 : 50

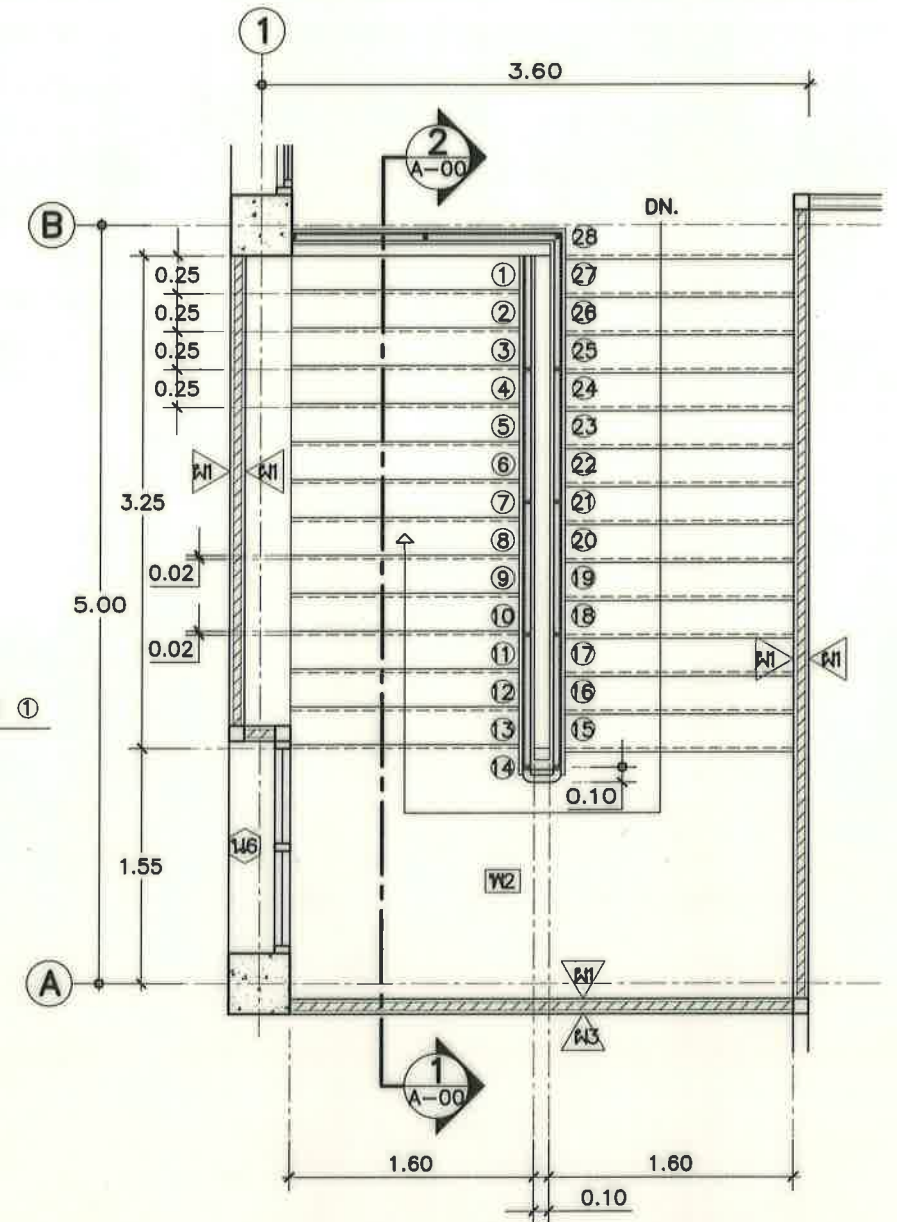





แปลนขยายบันไดชั้นดาดฟ้า ST-2
มาตราส่วน 1 : 50

TOT Property Management Department ฝ่ายบริหารทรัพย์สิน ส่วนอาคารและวิศวกรรมอาคาร	เจ้าของโครงการ	ฝ่ายพัฒนาผลิตภัณฑ์ระหว่างประเทศ	สถาปนิก	สนั่น นาคนิกร ๙-๘๘๖๑๙	วิศวกรระบบไฟฟ้ากำลัง	เฉลิมชัย พงศากร ๙๙๙ ๖๖๒๕	วิศวกรระบบป้องกันอัคคีภัย	ประทีป อินทรศักดิ์ ๙๙๙ ๖๗๐๗	ตรวจ	วิรัชชัย ๙๙๙ ๙๙๙	เลขที่แบบ	A-32
	แบบ	งานจ้างเหมาก่อสร้างอาคารสถานประกอบการเคเบิลทีวี ปากบารา	วิศวกรโครงสร้าง	เอกสิทธิ์ จิระเกียรติ ๙๙๙ ๕๗๗๘	วิศวกรระบบควบคุมอัตโนมัติ	พงษ์ศักดิ์ บุญทวี ๙๙๙ ๕๘๗๔	วิศวกรระบบดับเพลิงอัตโนมัติ	ปรีชา เหมมัน ๙๙๙ ๓๐๑๔	เห็นชอบ	วิระ มาประเสริฐ ๙๙๙ ๙๙๙	แผนที/รวม	A-32/49
	แสดง	แปลนขยายบันได ST-2	มาตราส่วน	1:50	วิศวกรระบบสุขาภิบาล	เฉลิมพล อุดมบุตร ๙๙๙ ๒๑๐๓๕	วิศวกรระบบปรับอากาศ	สุมิตร ศรีวิวัฒน์ ๙๙๙ ๑๐๖๖๖	อนุมัติ	สุชาติ ชัยสุข ๙๙๙ ๙๙๙		
			เขียน	สิงห์ อาษา								

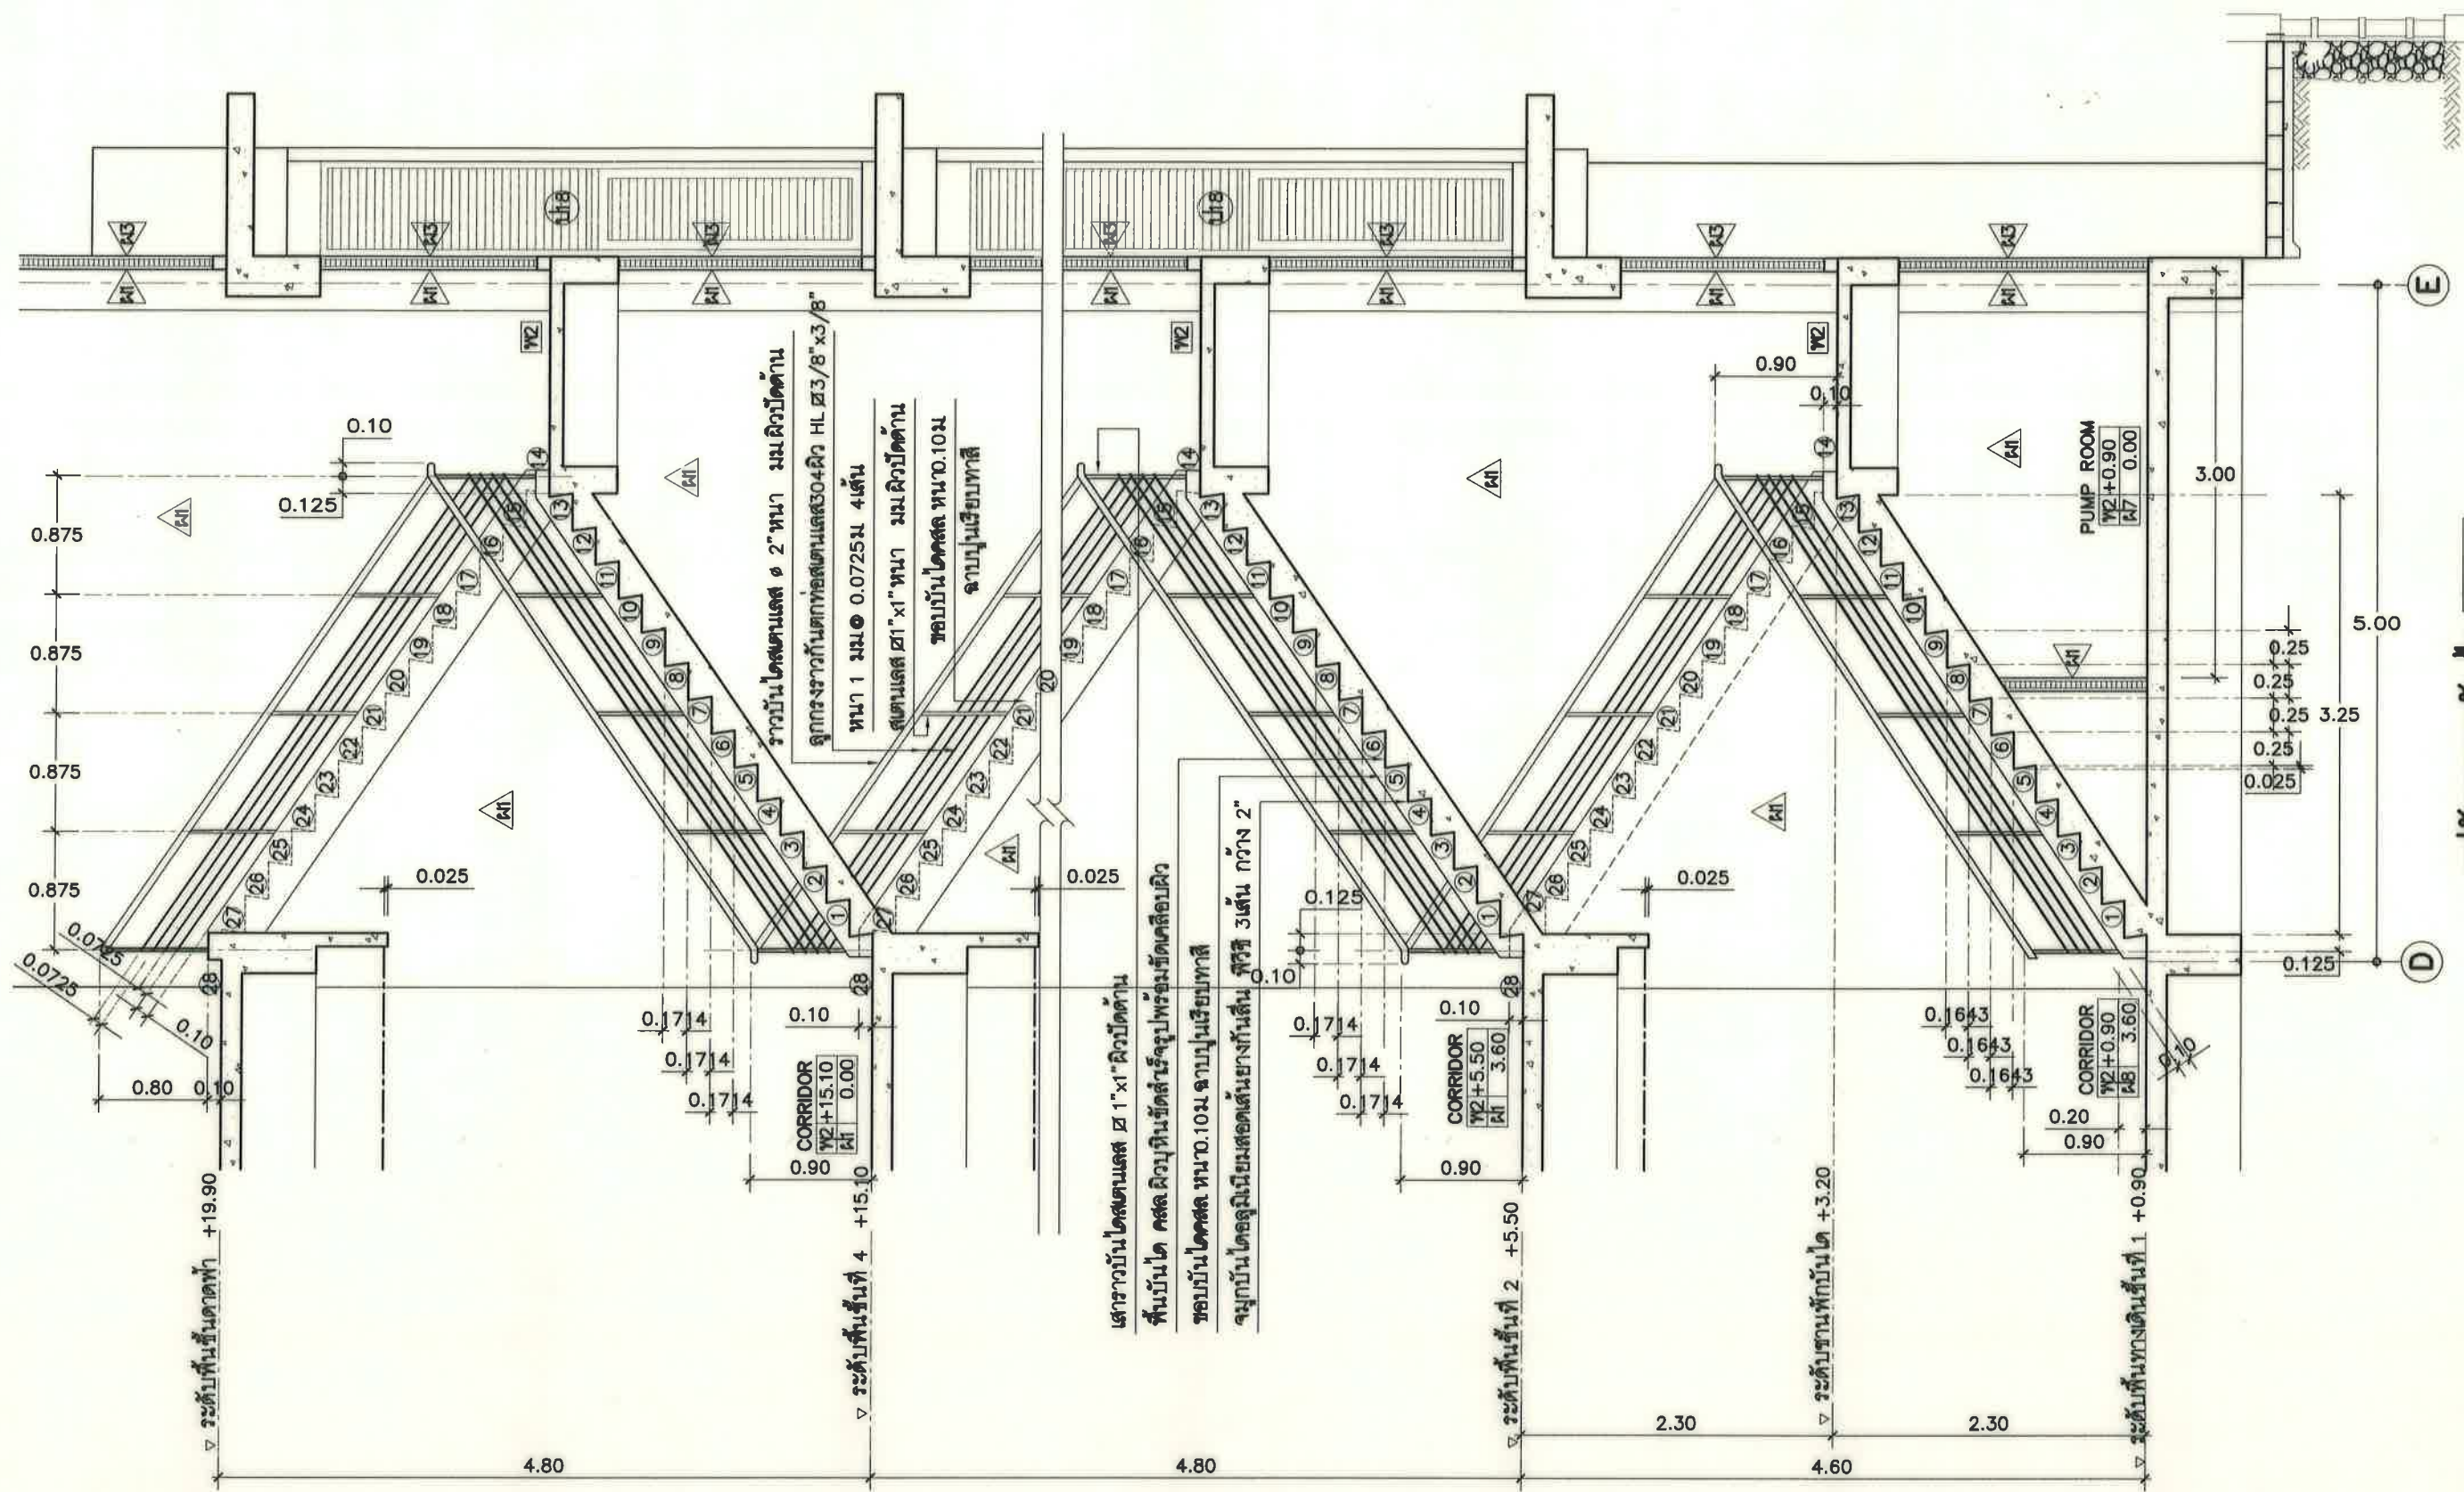


รูปตัดขยายบันได ST-2
มาตราส่วน 1 : 50

 TOT Property Management Department ฝ่ายบริหารทรัพย์สิน ส่วนอาคารและวิศวกรรมอาคาร	เจ้าของโครงการ	ฝ่ายพัฒนาผลิตภัณฑ์ระหว่างประเทศ	สถาปนิก	สนั่น นาคนิกร ๓-๘๘๙๖๑	วิศวกรระบบไฟฟ้ากำลัง	เฉลิมชัย พงษ์พานิช ๓๖๒๕	วิศวกรระบบป้องกันอัคคีภัย	ประทีป อินทพงศ์ ๓๖๒๗	ตรวจ	วิมล ๓๖๒๗	เลขที่แบบ	A-33
	แบบ	งานจ้างเหมาก่อสร้างอาคารสถานประกอบการและที่พักอาศัย	วิศวกรโครงสร้าง	เอกสิทธิ์ จันทระเกียรติ ๓๖๕๗๗	วิศวกรระบบควบคุมอัตโนมัติ	พงษ์ศักดิ์ บุญทวี ๓๖๕๗๗	วิศวกรระบบดับเพลิงอัตโนมัติ	ปรีชา เหมมัน ๓๖๓๐๑๔	เห็นชอบ	ศิริ มาประเสริฐ ๓๖๓๐๑๔	แผ่นที่/รวม	33/49
	แสดง	แปลนขยายบันได ST-2	วิศวกรระบบสุขาภิบาล	เฉลิมพล อุดมย์บุตร ๓๖๒๓๕	วิศวกรระบบสื่อสาร	ปานทิพย์ พูนผล	วิศวกรระบบปรับอากาศ	สุเมธ ศรีวิวัฒน์ ๓๖๑๐๖๖	อนุมัติ	สุชาติ ๓๖๑๐๖๖		
			เขียน	สิงห์ อาษา								

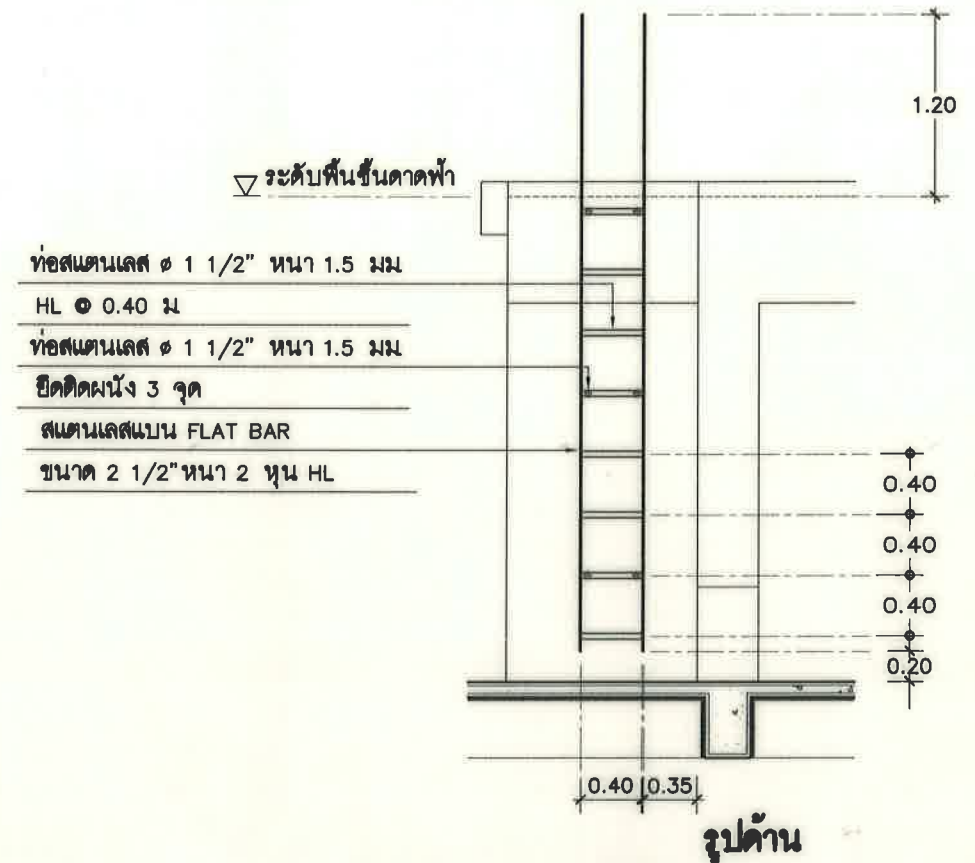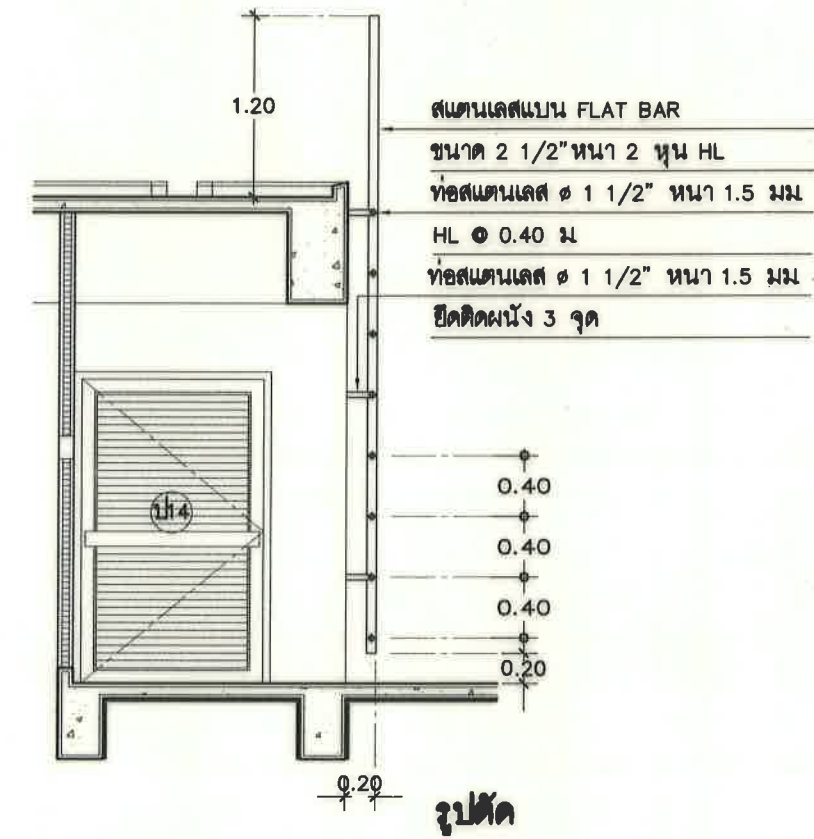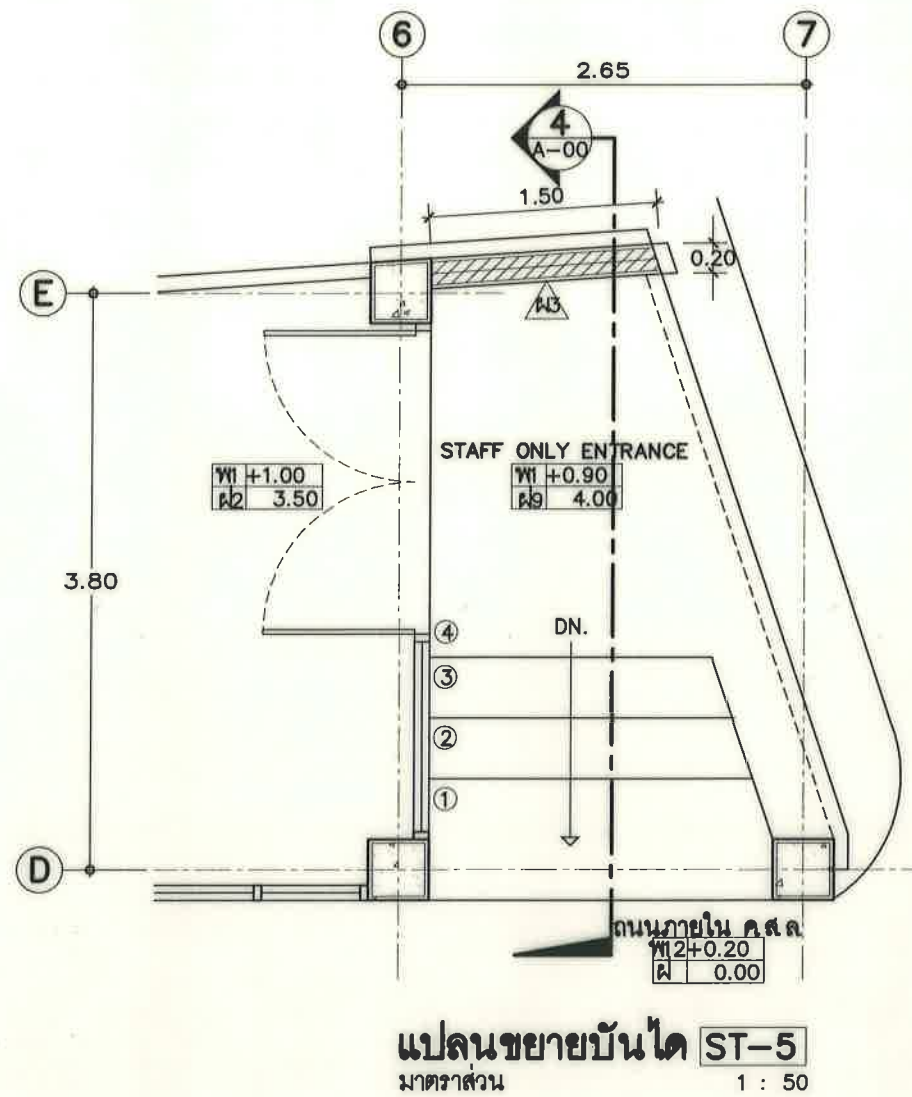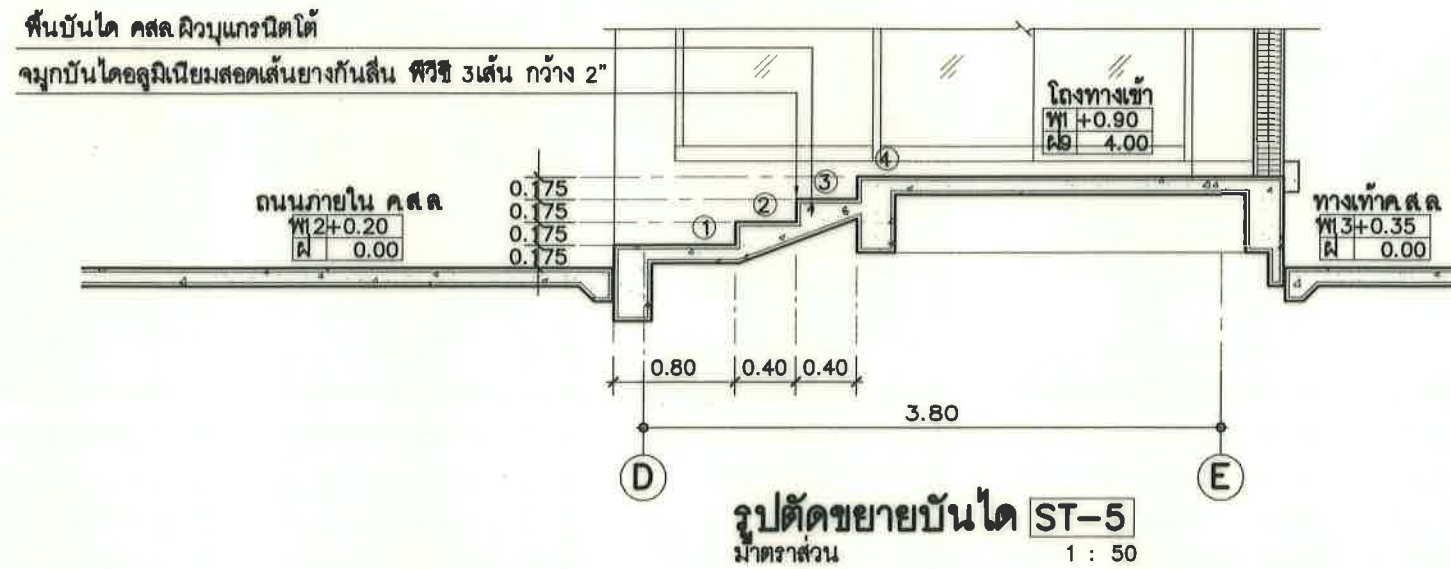


รูปตัดขยายบันไดหนีไฟ ST-6
มาตราส่วน 1 : 50

Property Management Department ฝ่ายบริหารทรัพย์สิน ส่วนออกใบวิศวกรรมการอาคาร	เจ้าของโครงการ	ฝ่ายพัฒนาผลิตภัณฑ์ระหว่างประเทศ	สถาปนิก	สนั่น นาคนิกร ๓-๓๑๙๖๑๙	วิศวกรระบบไฟฟ้ากำลัง	เฉลิมชัย พงษ์ชากร ภพท 6625	วิศวกรระบบป้องกันอัคคีภัย	ประทีป อินทรศักดิ์ ภพท 6707	ตรวจ	วิรัช ภิทยามา ๓๖ ๐๐/๕๖	ผจ.สอ.ทพ.	เลขที่แบบ
	แบบ	งานจ้างเหมาก่อสร้างอาคารสถานที่มีโครงการเขตนีโอมา ปากบารา อ.ละงู จ.สตูล พร้อมงานติดตั้งระบบปรับอากาศ และงานรื้อถอน	วิศวกรโครงสร้าง	เอกสิทธิ์ จิงขจรเกียรติ สย.๕๗๗๘	วิศวกรระบบควบคุมอัตโนมัติ	พงษ์ศักดิ์ บุญทวี ภพท.๕๘๗๔	วิศวกรระบบดับเพลิงอัตโนมัติ	ปรีชา เหมมัน สก.๓๐๑๔	เห็นชอบ	ศิริ มาประเสริฐ ๓๔ ๐๐/๕๖	ผจ.สอ.ทพ.	A-35
	แสดง	แบบขยายบันได ST-5 , ST-6	มาตราส่วน	เขียน	วิศวกรระบบสุขาภิบาล	เฉลิมพล อดุลย์นร ๓๒ ๒๑๐๓๕	วิศวกรระบบสื่อสารสัญญาณ	สุมิตร ศรีวัฒนะ ภท.๑๐๖๖๕	อนุมัติ	สุชาติ ทรัพย์ ๒๗ ๐๐/๕๖	ผจ.ทพ.	แผ่นที่/รวม
				สิงห์ อาษา								35/49

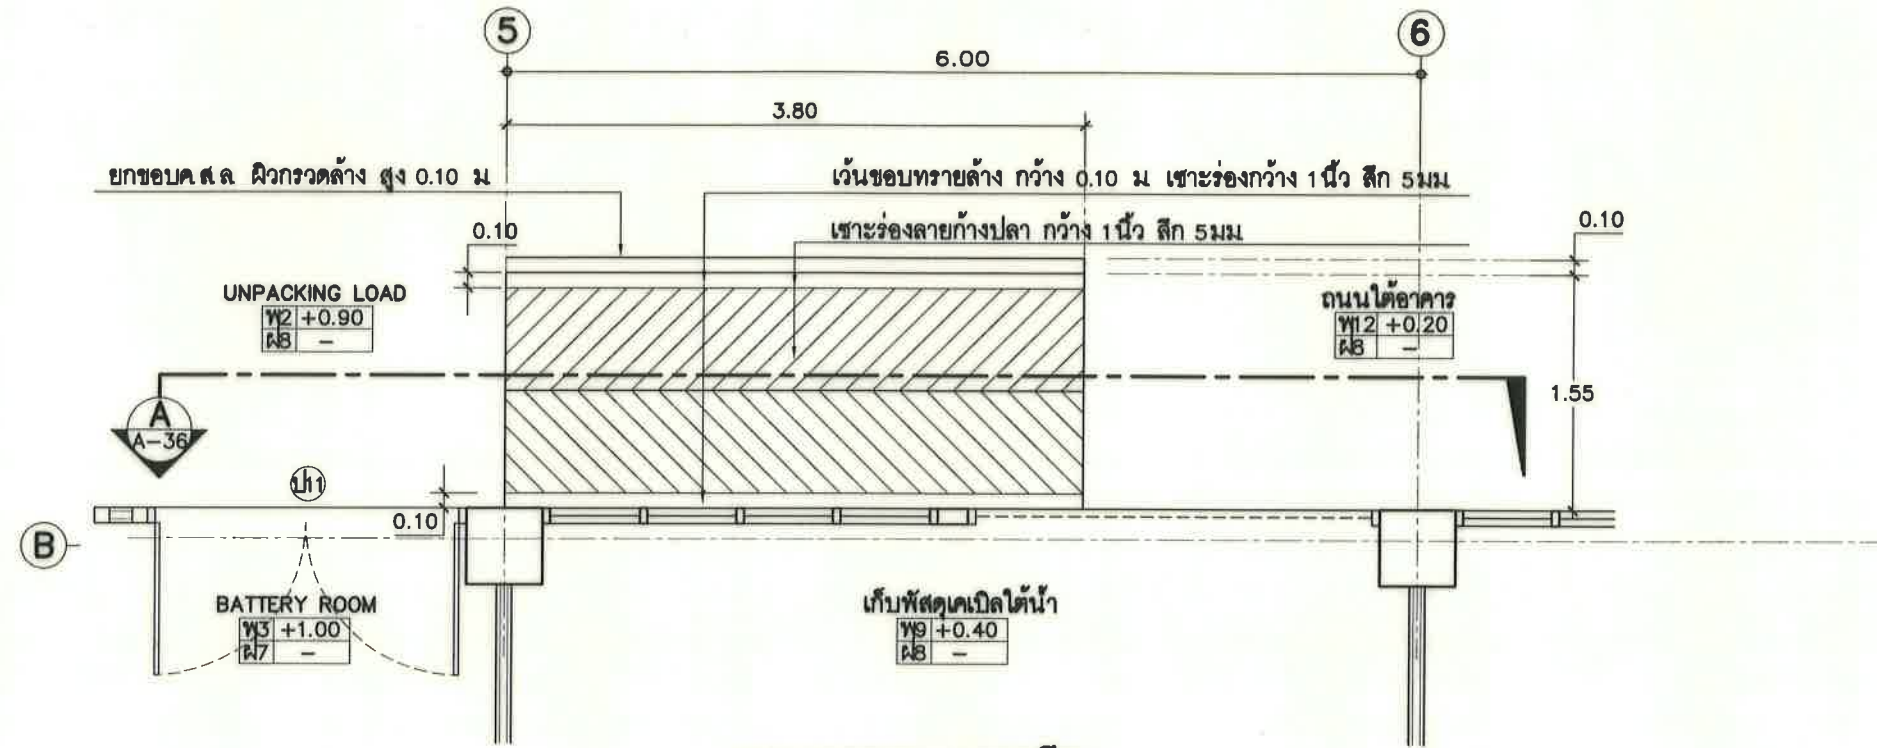

แบบขยายทางลาดเอียง


มาตราส่วน 1 : 50

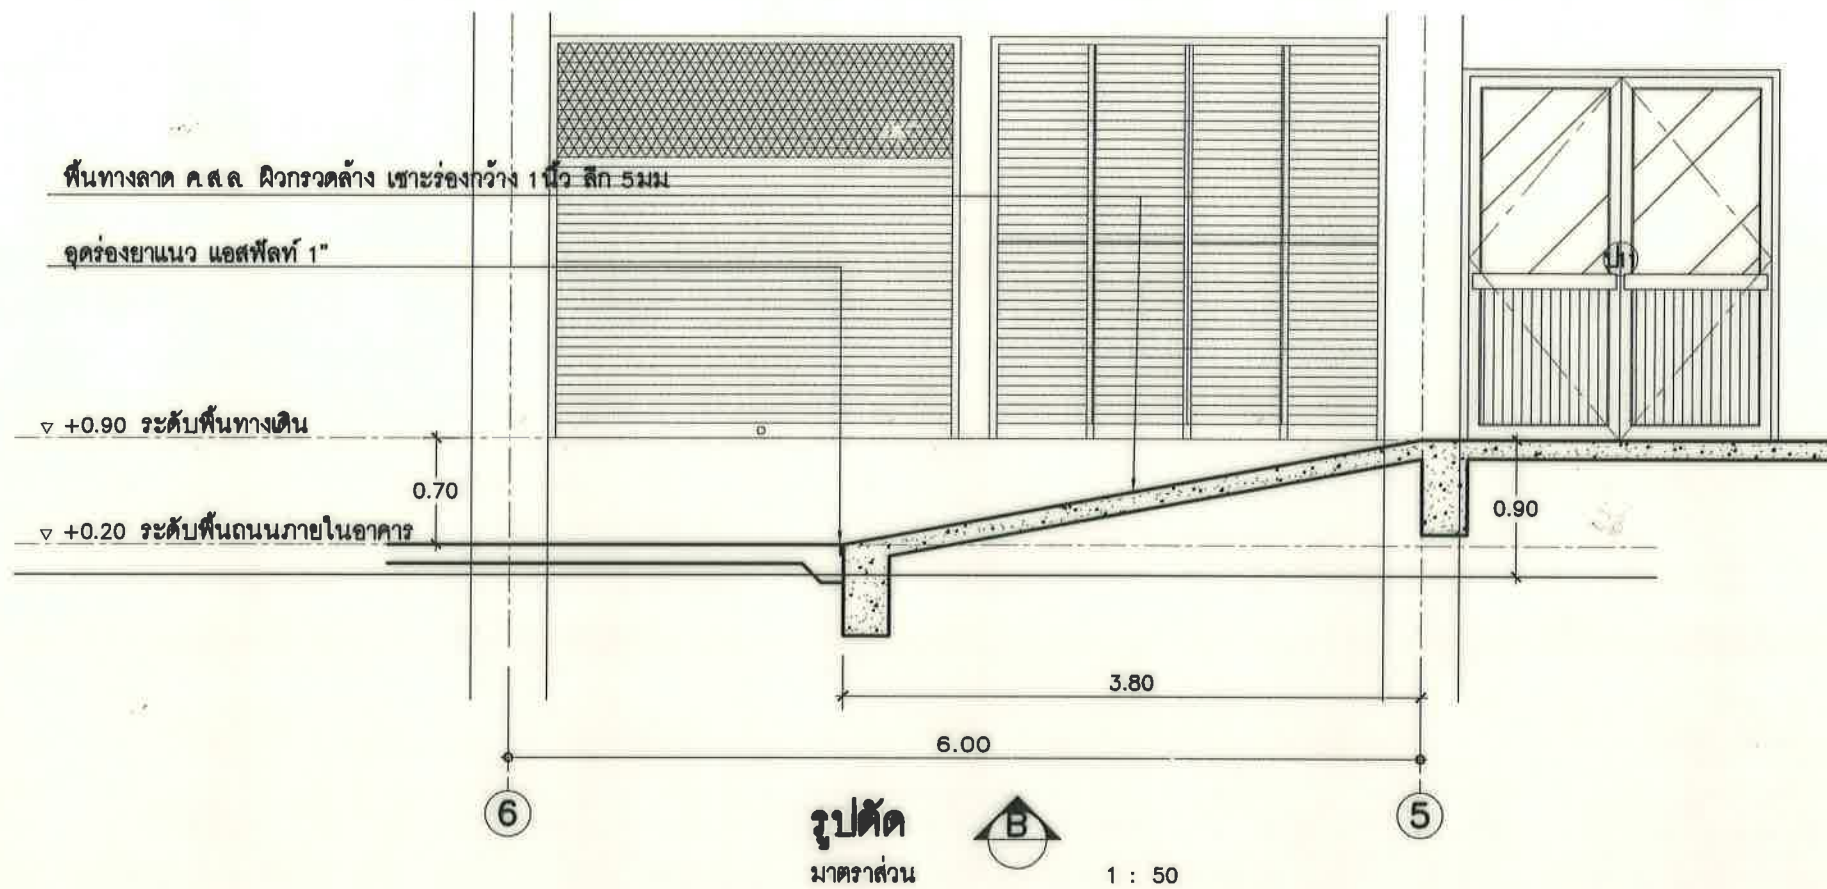


รูปตัด

มาตราส่วน 1 : 50


TOT Property Management Department ฝ่ายบริหารทรัพย์สิน ส่วนออกใบวิศวกรรมการ	เจ้าของโครงการ	ฝ่ายพัฒนาผลิตภัณฑ์ระหว่างประเทศ	สถาปนิก	สนั่น นาคนิกร ๙-๘๘๙๖๑๙	วิศวกรระบบไฟฟ้ากำลัง	เฉลิมชัย พงษ์จักร ๙๗๖ ๖๖๒๕	วิศวกรระบบป้องกันอัคคีภัย	ประทีป ชินทรศักดิ์ ๙๗๖ ๖๗๐๗	ตรวจ	วิมล ๙๗๖ ๖๗๐๗	เลขที่แบบ	A-36
	แบบ	งานจ้างเหมาก่อสร้างอาคารสถานีโครงการเขื่อนลำนาน้ำปากบารา	วิศวกรโครงสร้าง	เอกสิทธิ์ จันทะเกียรติ ๙๗๖ ๕๗๗๘	วิศวกรระบบควบคุมอัตโนมัติ	พงษ์ศักดิ์ บุญทวี ๙๗๖ ๕๘๗๔	วิศวกรระบบดับเพลิงอัตโนมัติ	ปรีชา เหมนัน ๙๗๖ ๓๐๑๔	เห็นชอบ	วิมล ๙๗๖ ๕๗๗๘	แผ่นที่/รวม	36/49
	แสดง	มาตราส่วน 1 : 50	วิศวกรระบบสุขาภิบาล	เฉลิมพล อุดมบุตร ๙๗๖ ๒๑๐๓๕	วิศวกรระบบสื่อสารสัญญาณ	ปานทิพย์ พูนผล	วิศวกรระบบปรับอากาศ	สุมิตร ศรีวิวัฒน์ ๙๗๖ ๑๐๖๘๘	อนุมัติ	วิมล ๙๗๖ ๕๗๗๘		
	แบบขยายทางลาดเอียง	เขียน	สนั่น นาคนิกร									

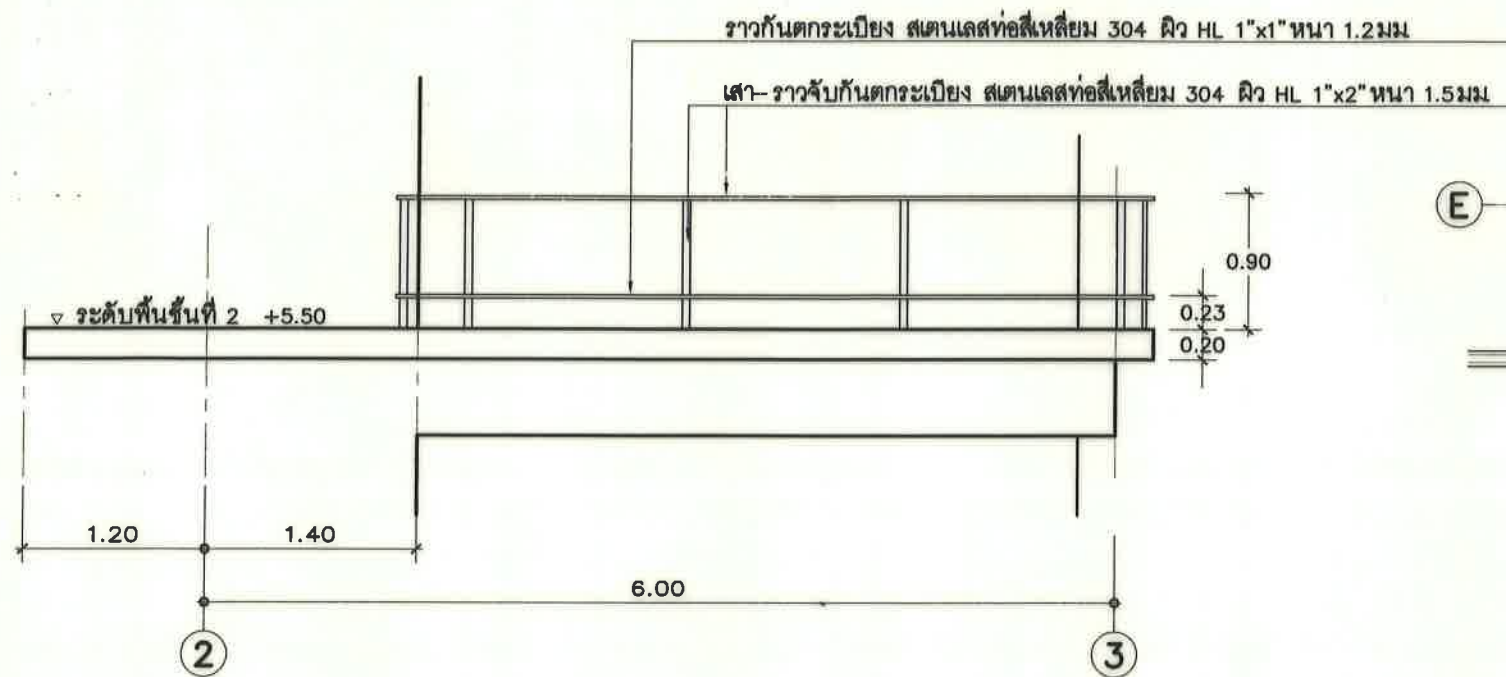


รูปด้านขยายระเบียง
มาตราส่วน 1 : 50

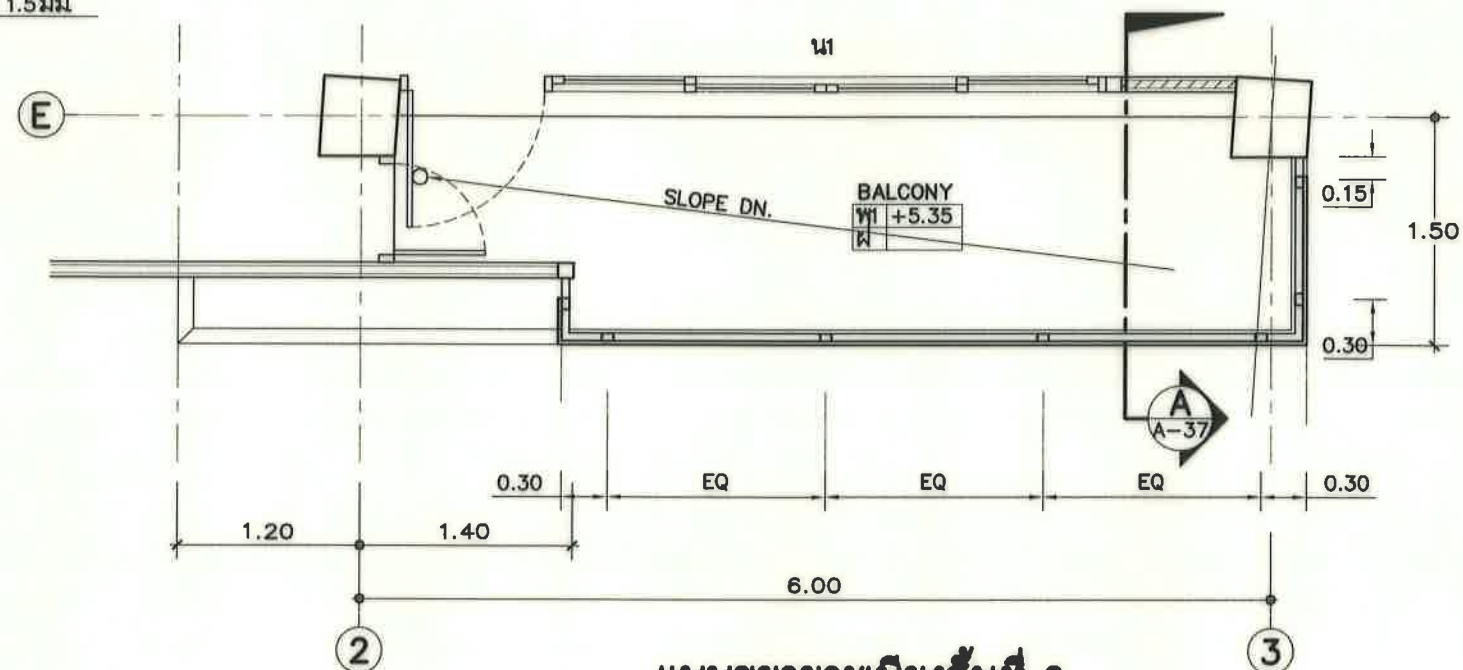

แบบขยายระเบียงชั้นที่ 2
มาตราส่วน 1 : 50

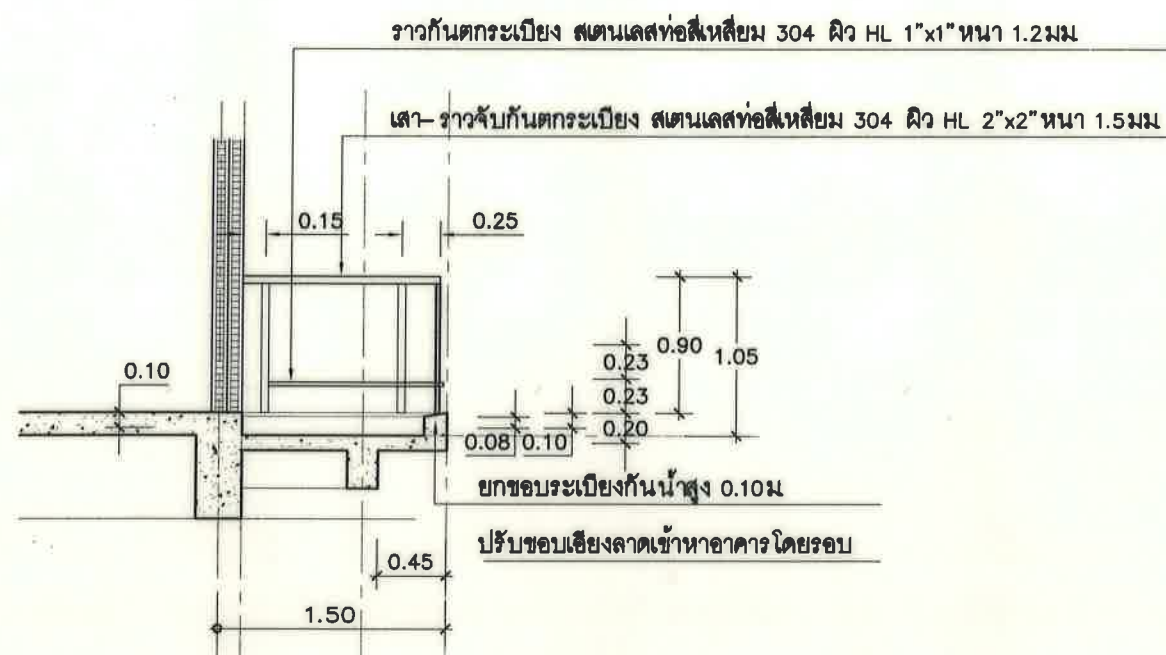


รูปตัดขยายระเบียง
มาตราส่วน 1 : 50

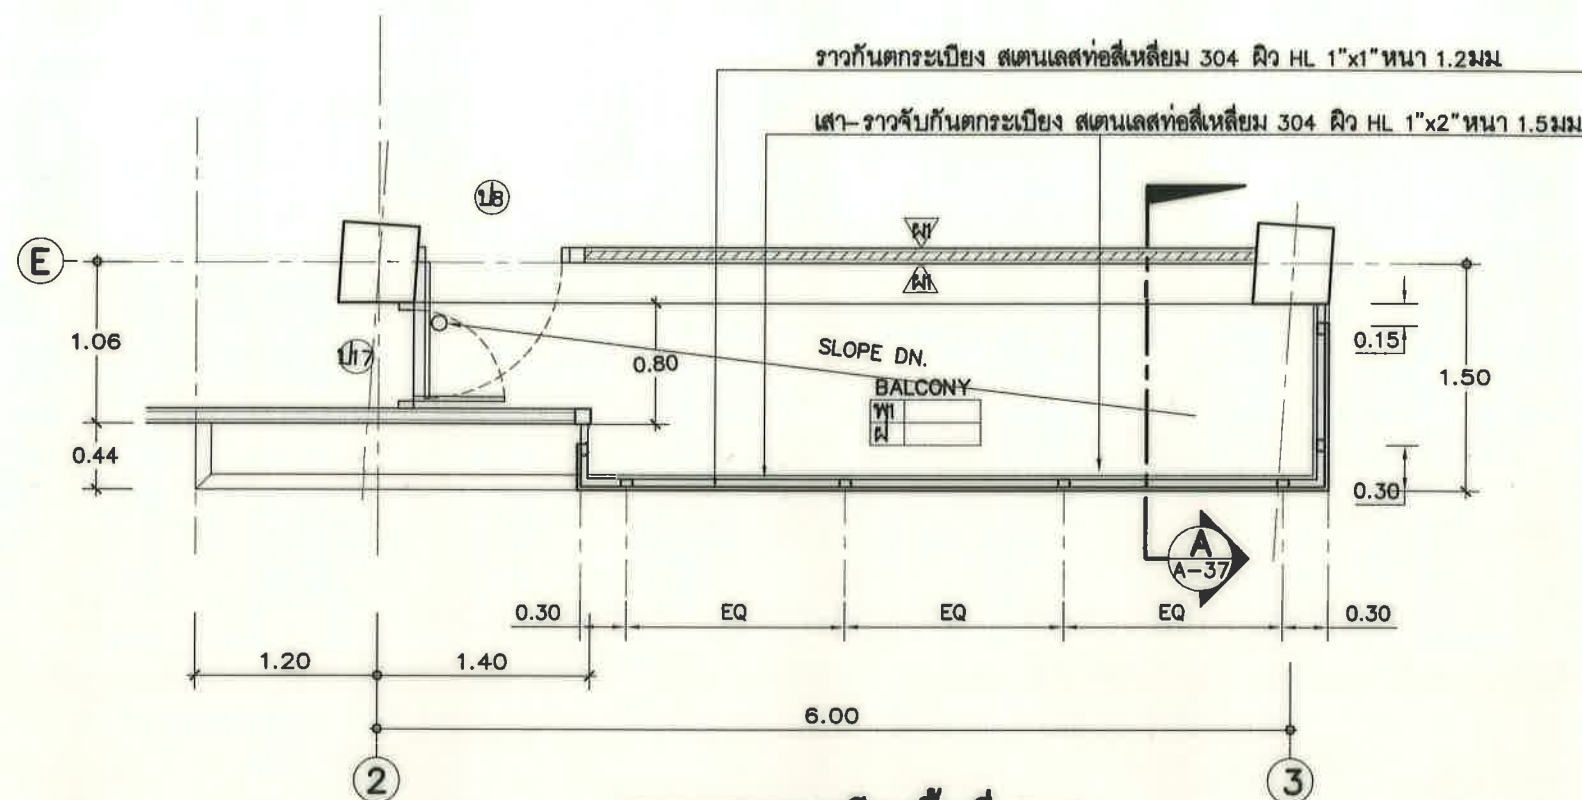

แบบขยายระเบียงชั้นที่ 3-4
มาตราส่วน 1 : 50


	เจ้าของโครงการ	ฝ่ายพัฒนาผลิตภัณฑ์ระหว่างประเทศ	สถาปนิก	สนั่น นาคนิกร ๙-๘๘๙๖๑๙	วิศวกรระบบไฟฟ้ากำลัง	เฉลิมชัย พงษ์ชากร ๙๙๙ ๖๖๒๕	วิศวกรระบบป้องกันอัคคีภัย	ประทีป อินทพงศ์ ๙๙๙ ๖๗๐๗	ตรวจ	วิรัชพงศ์/พิทยามา	๙๘/๙๙/๕๖	เลขที่แบบ	A-37
	แบบ	งานจ้างเหมาก่อสร้างอาคารสถานีโครงการเขื่อนลัดน้ำ ปากบารา	วิศวกรโครงสร้าง	เอกสิทธิ์ จิระขจรเกียรติ ๙๙๙ ๕๗๗๘	วิศวกรระบบควบคุมอัตโนมัติ	พงษ์ศักดิ์ บุญทวี ๙๙๙ ๕๘๗๔	วิศวกรระบบดับเพลิงอัตโนมัติ	ปรีชา เหมรัตน์ ๙๙๙ ๓๐๑๔	เห็นชอบ	ศิริ มาประเสริฐ	๙๘/๙๙/๕๖	แผ่นที่/รวม	37/49
	แสดง	อลงู จ.สตูล พร้อมงานติดตั้งระบบปรับอากาศ และงานรื้อถอน	วิศวกรระบบสุขาภิบาล	เฉลิมพล อุดมบุตร ๙๙๙ ๒๑๐๓๕	วิศวกรระบบสื่อสารสัญญาณ	ปานทิพย์ พูนผล	วิศวกรระบบปรับอากาศ	สุมิตร ศรีวิวัฒน์ ๙๙๙ ๑๐๘๖๖	อนุมัติ	สุชาติ ราชย์	๙๘/๙๙/๕๖		
	มาตราส่วน	1 : 50	เขียน	สนั่น นาคนิกร									

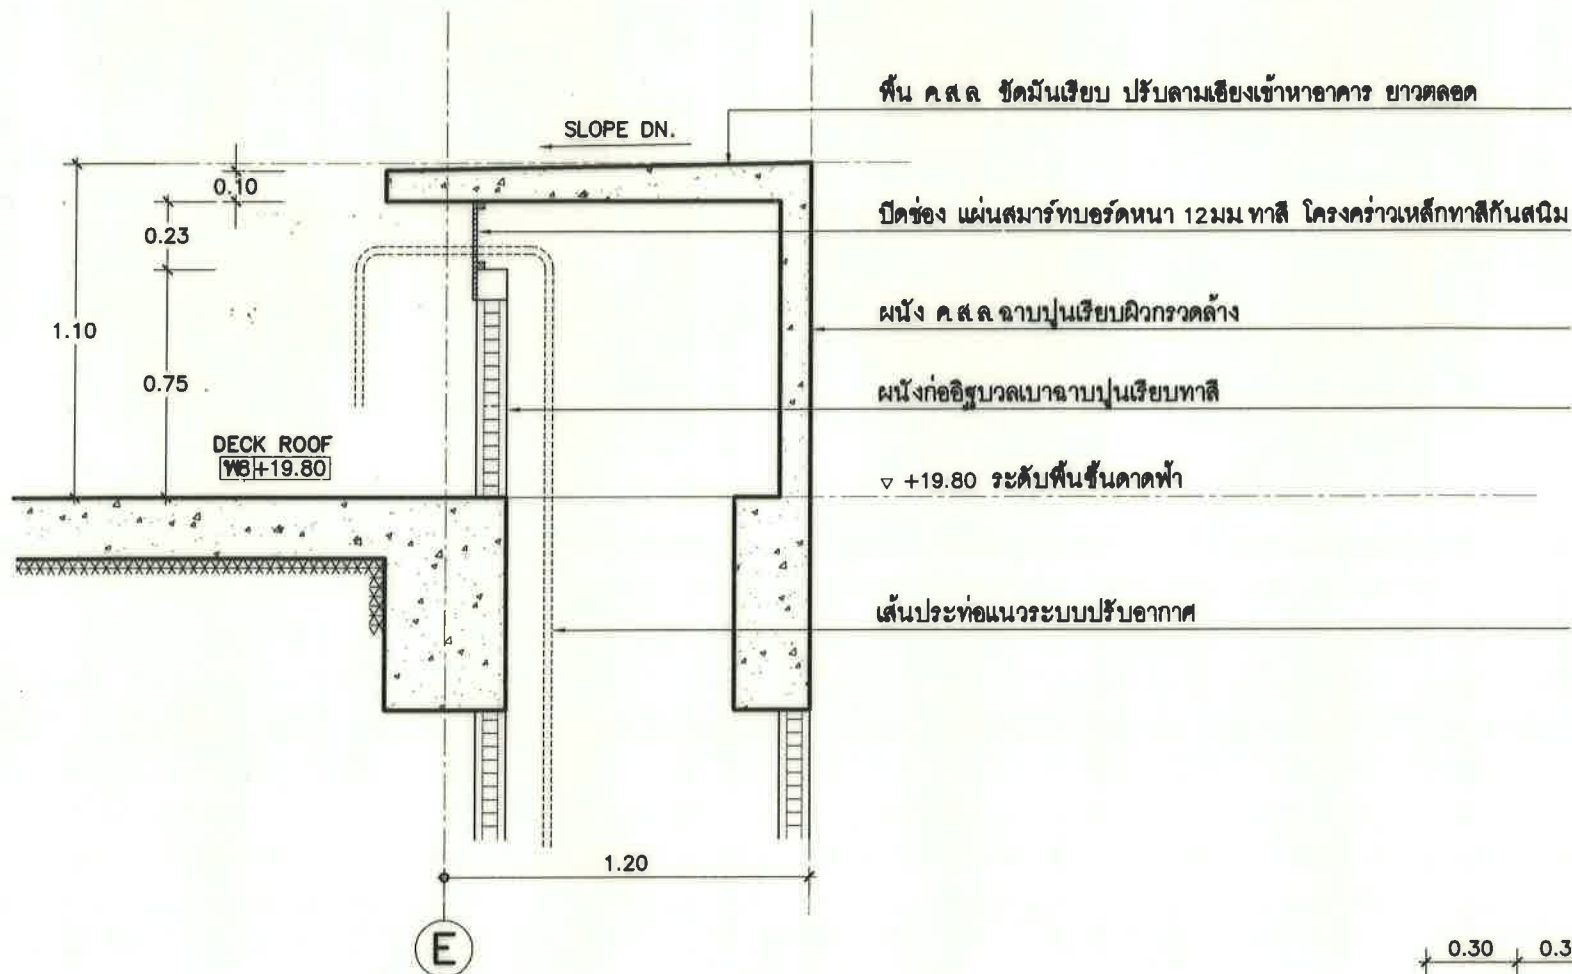

แบบขยายช่อง DUCT แอร์ ชั้นดาดฟ้า

มาตราส่วน


1 : 25

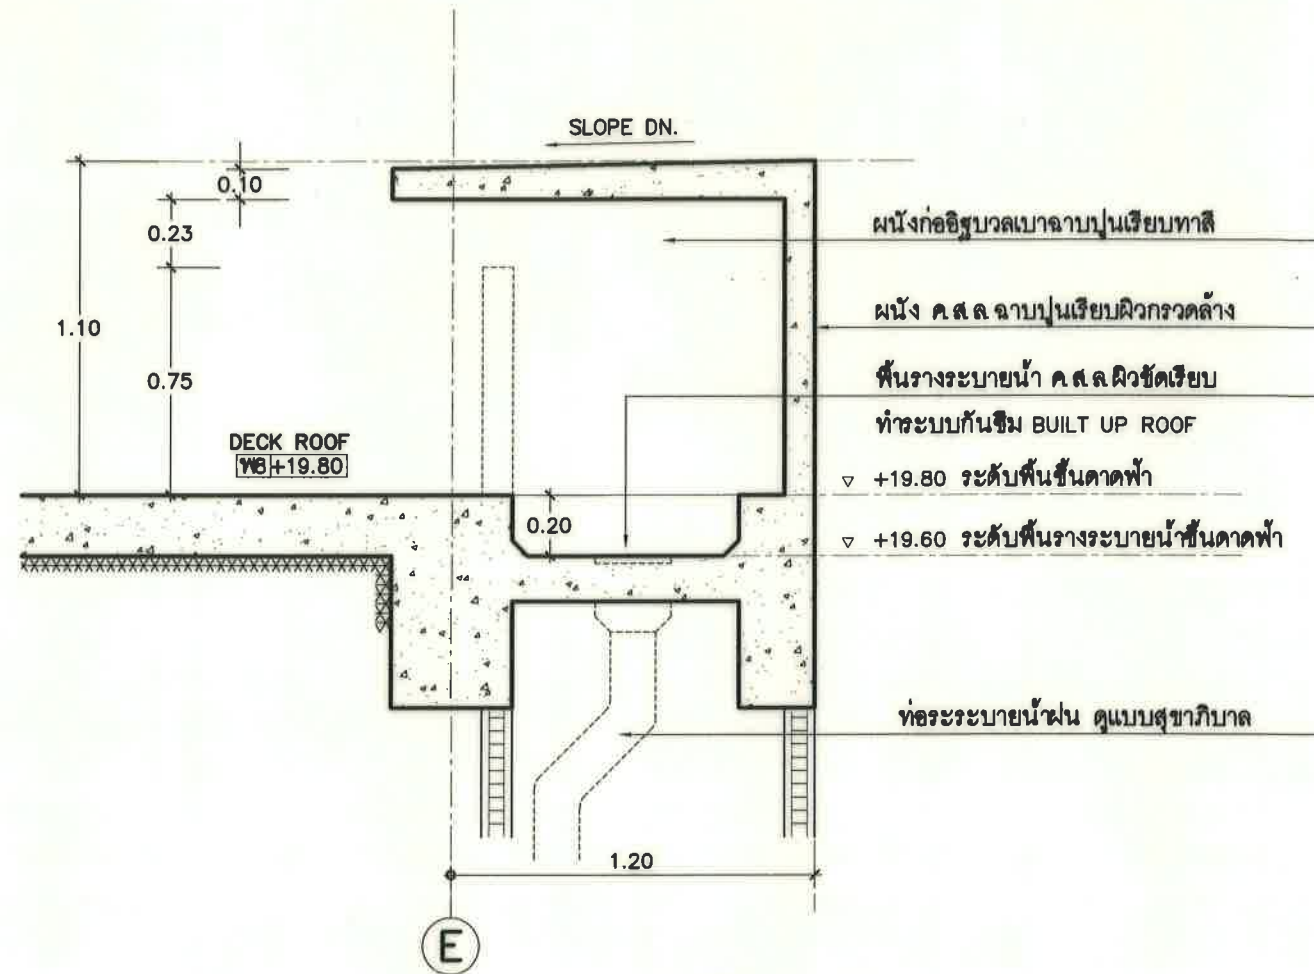

แบบขยายวางระบายน้ำชั้นดาดฟ้า

มาตราส่วน


1 : 25

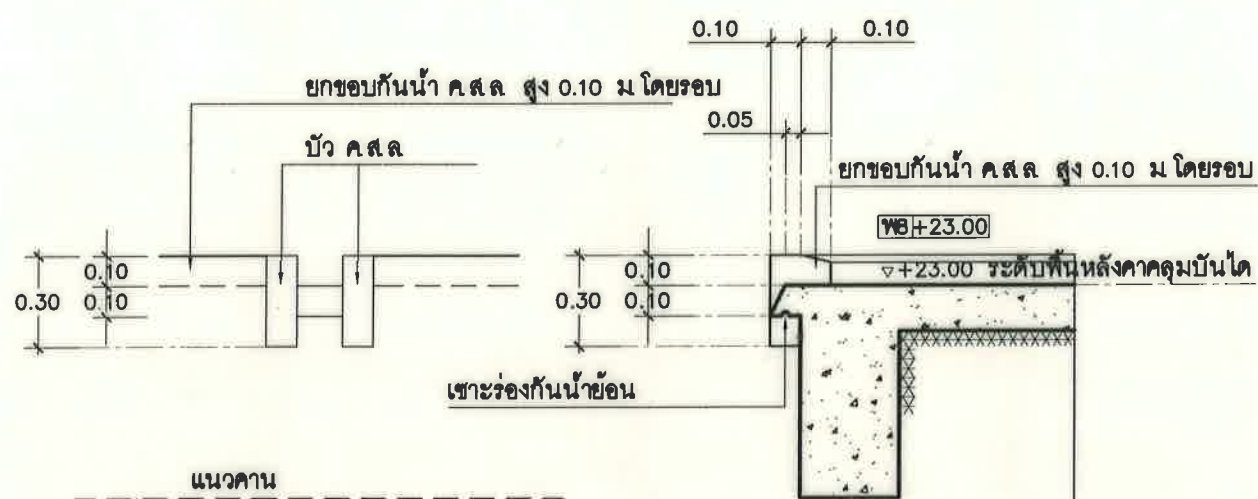

แบบขยายขอบวางน้ำ ค.ส.ล

มาตราส่วน


1 : 25

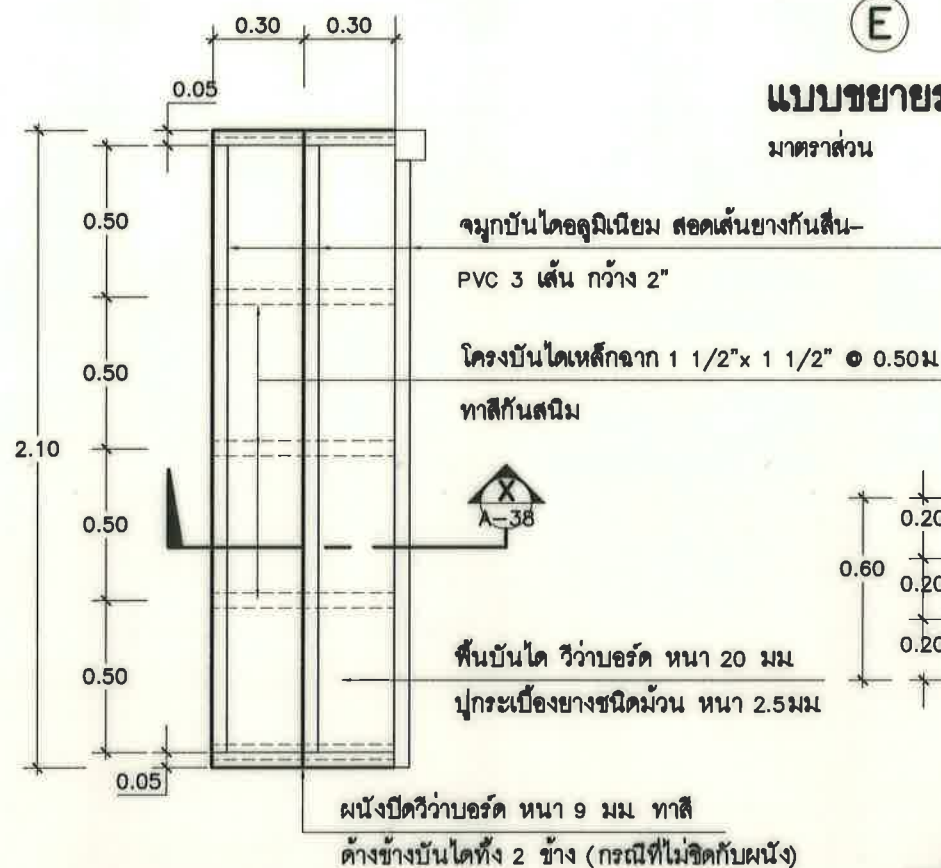

แปลนขยายบันไดต่างระดับภายใน

มาตราส่วน

1:25

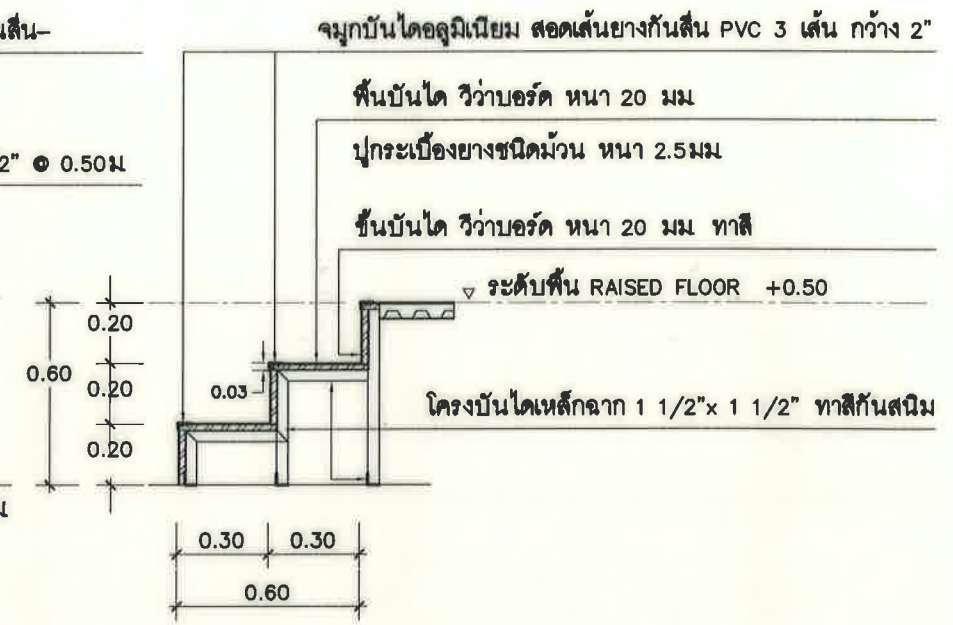


รูปตัดขยายบันได


มาตราส่วน

1:25

Property Management Department ฝ่ายบริหารทรัพย์สิน ส่วนอาคารและวิศวกรรมอาคาร	เจ้าของโครงการ	ฝ่ายพัฒนาผลิตภัณฑ์ระหว่างประเทศ	สถาปนิก	สนั่น นาคนิกร ๓-๓๘๖๑๙	วิศวกรระบบไฟฟ้ากำลัง	เฉลิมชัย พุกผาธร ๓๖๒๕	วิศวกรระบบป้องกันอัคคีภัย	ประทีป อินทรศักดิ์ ๓๖๒๗	ตรวจ	วิมล ๓๖/๓๖๖๖	เลขที่แบบ	A-38
	แบบ	งานช่างเทคนิคอาคารสถานที่โครงการขยายเคหะชุมชน ปากบารา อ.ละมั่ง จ.สกลนคร พร้อมงานติดตั้งระบบปรับอากาศ และงานรื้อถอน	วิศวกรโครงสร้าง	เอกสิทธิ์ จิงขจรเกียรติ ๓๖๕๗๗๘	วิศวกรระบบควบคุมอัตโนมัติ	พงษ์ศักดิ์ บุญทวี ๓๖๕๗๗๔	วิศวกรระบบดับเพลิงอัตโนมัติ	ปรีชา เหมมัน ๓๖๓๐๑๔	เห็นชอบ	๓๖/๓๖๖๖	แผ่นที่/รวม	38/49
	แสดง	แบบขยายช่อง DUCT แอร์ ชั้นดาดฟ้า	มาตราส่วน	1 : 25	วิศวกรระบบสุขาภิบาล	เฉลิมพล อดุลย์บุตร ๓๖๒๑๓๕	วิศวกรระบบสื่อสารสัญญาณ	ปานทิพย์ หุ่นผล	อนุมัติ	๓๖/๓๖๖๖		
	แบบขยาย	บันไดต่างระดับภายในอาคาร	เขียน	สนั่น นาคนิกร								

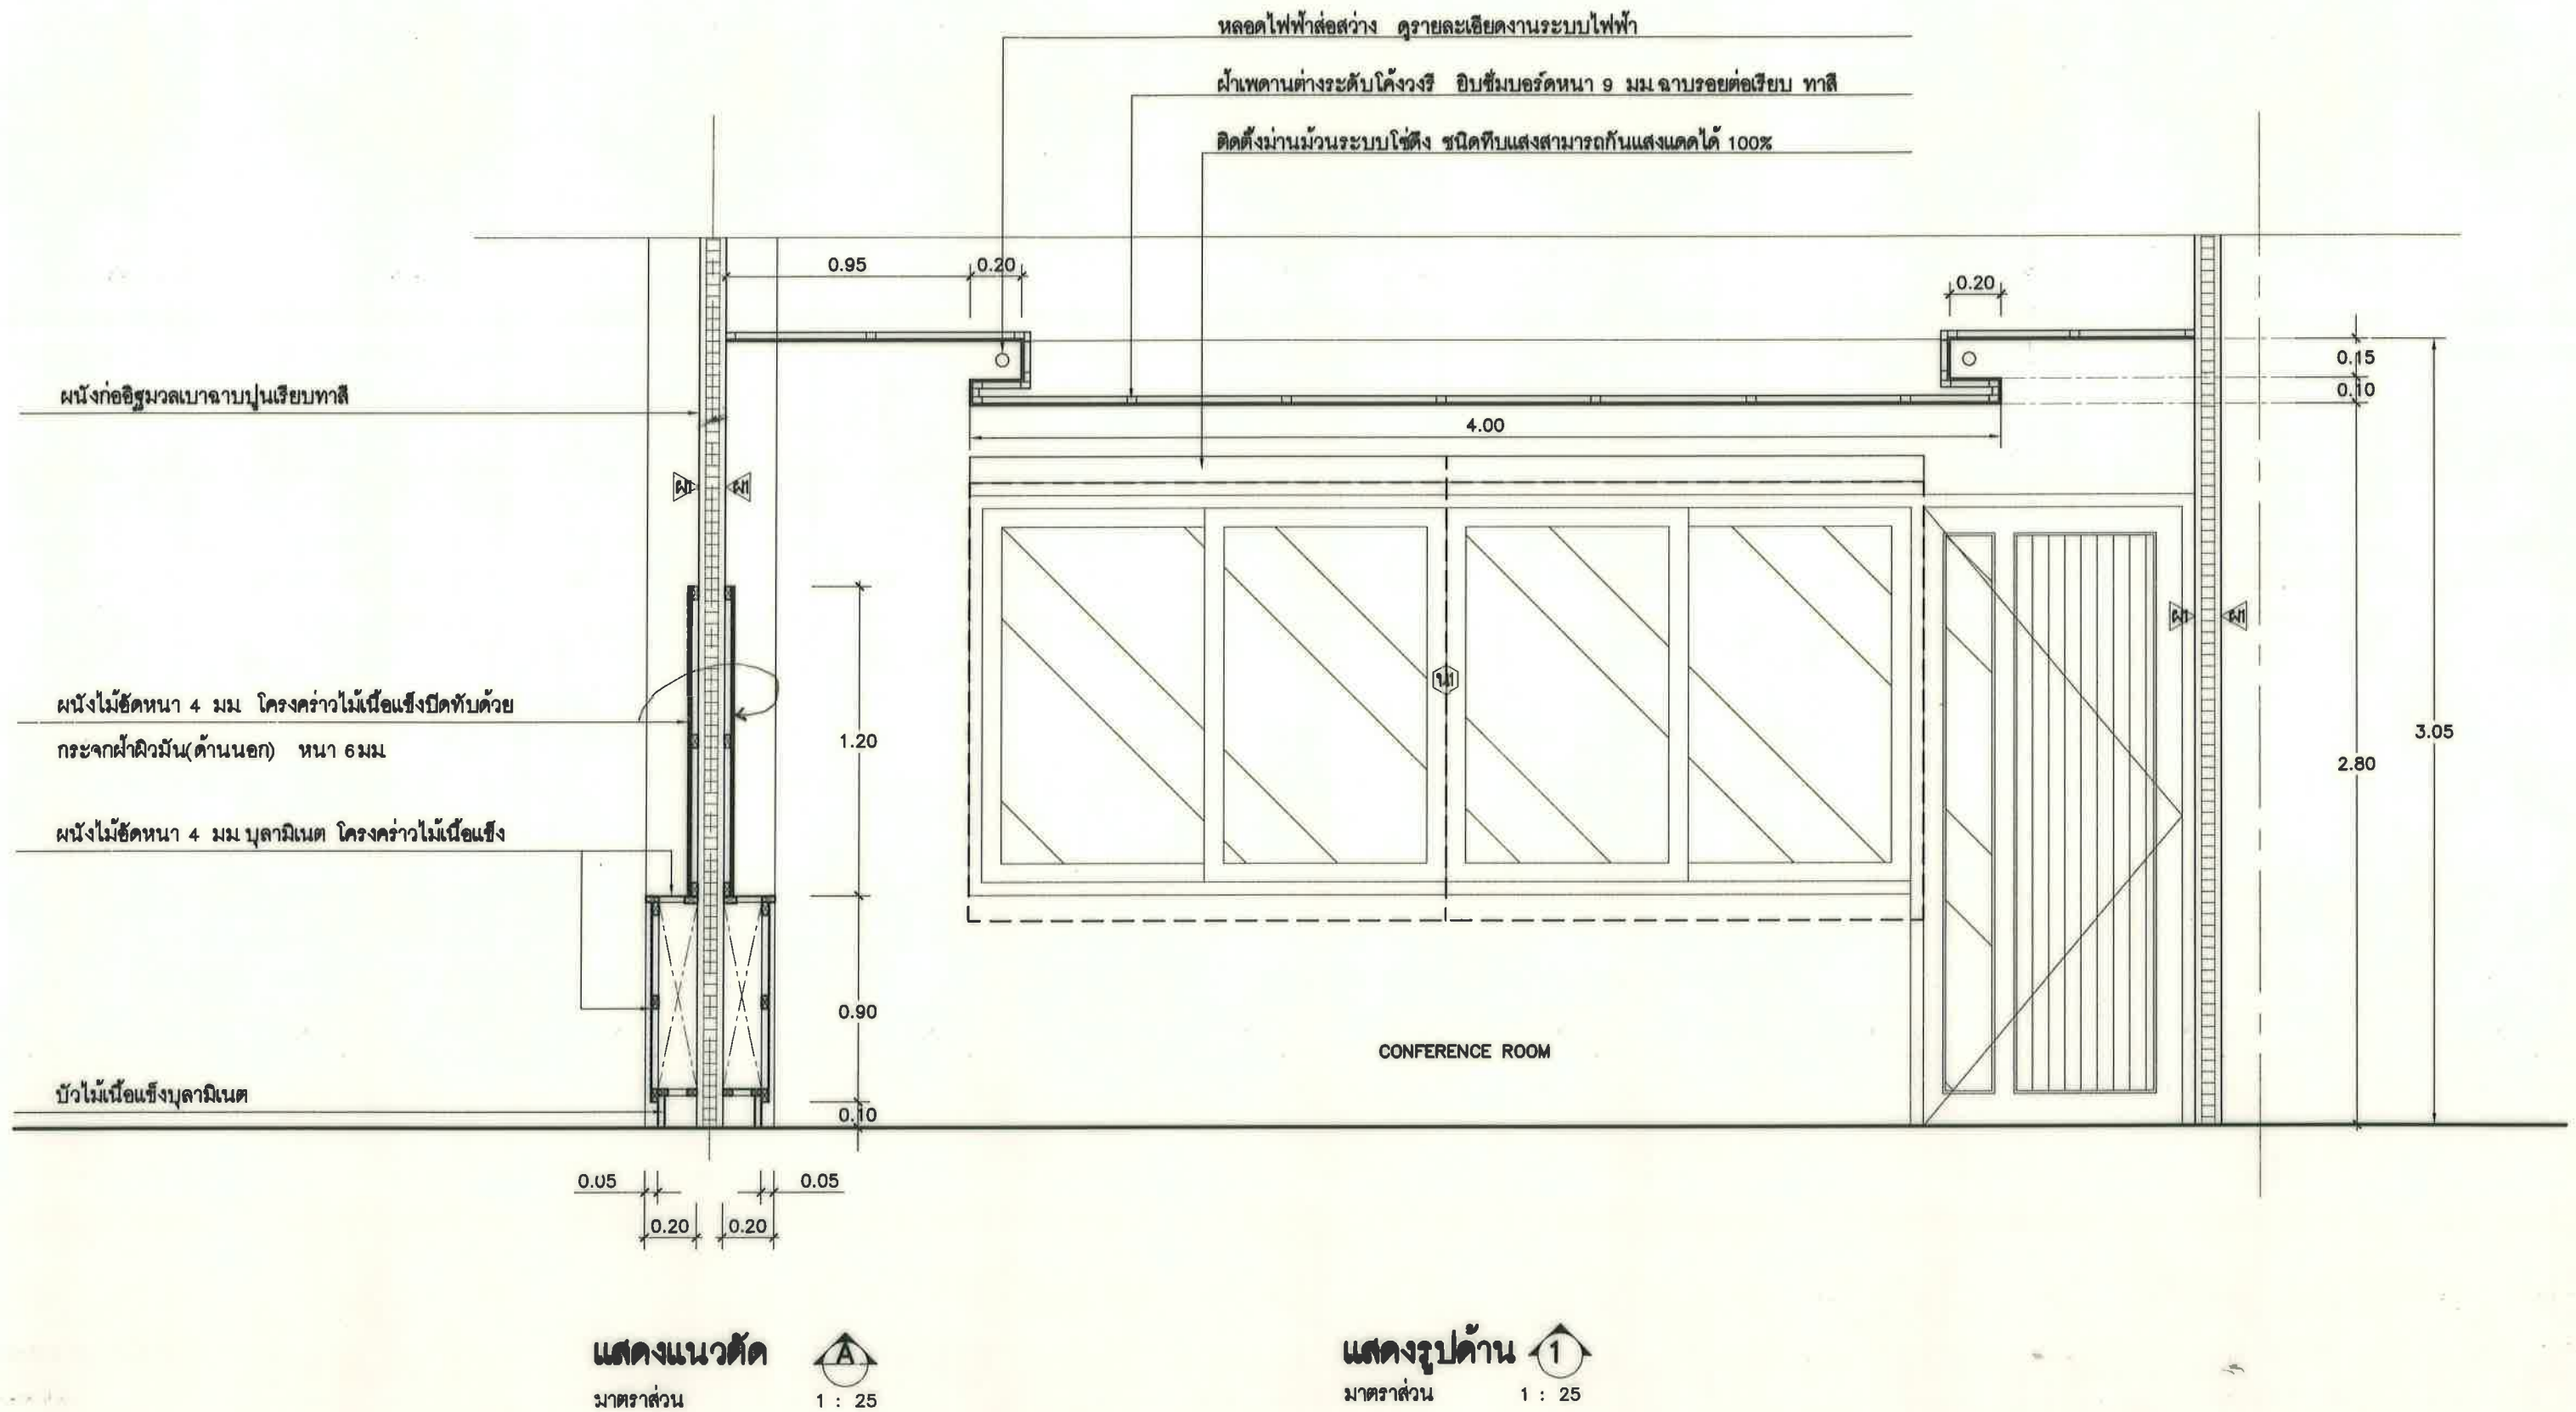

TOT Property Management Department ฝ่ายบริหารทรัพย์สิน ส่วนออกแบบวิศวกรรมอาคาร	เจ้าของโครงการ	ฝ่ายพัฒนาผลิตภัณฑ์ระหว่างประเทศ	สถาปนิก	สนั่น นาคนิกร ภา-สธ9619	วิศวกรระบบไฟฟ้ากำลัง	เฉลิมชัย พุกษากกร ภาฟก 6625	วิศวกรระบบป้องกันอัคคีภัย	ประทีป อินทรศักดิ์ ภาฟล 6707	ตรวจ	วิรัชพงศ์ ภัทยามาศ 78/ค.4.5	เลขที่แบบ	A-40
	แบบ	งานจ้างเพื่อก่อสร้างอาคารสถานี่โครงการเคเบิลไต่หน้า ปากบารา	วิศวกรโครงสร้าง	เอกสิทธิ์ จิงขจรเกียรติ สย5778	วิศวกรระบบควบคุมอัตโนมัติ	จิระชาย เจริญสุขวิชญ์ ภาฟก 19309	วิศวกรระบบดับเพลิงอัตโนมัติ	ปรีชา เหมมัน สก3014	เห็นชอบ	วิระ มาประเสริฐ 26.ค.4.5	แผ่นที่/รวม	40/49
	แสดง	แบบขยายฝ้าเพดานและผนังห้องประชุม	วิศวกรระบบสุขาภิบาล	เฉลิมพล อุดยัษฐ ภาข 21035	วิศวกรระบบสื่อสารสัญญาณ	พงษ์ศักดิ์ บุญทวี ภาฟก5874	วิศวกรระบบปรับอากาศ	สุมิตร ศรีวิวัฒน์ ภาท10886	อนุมัติ	สุชาติ ชัยชู 27.ค.4.5		
	แสดงแนวตัด	แสดงรูปด้าน 1	เขียน	สนั่น นาคนิกร		ปานทิพย์ ทุนผล						

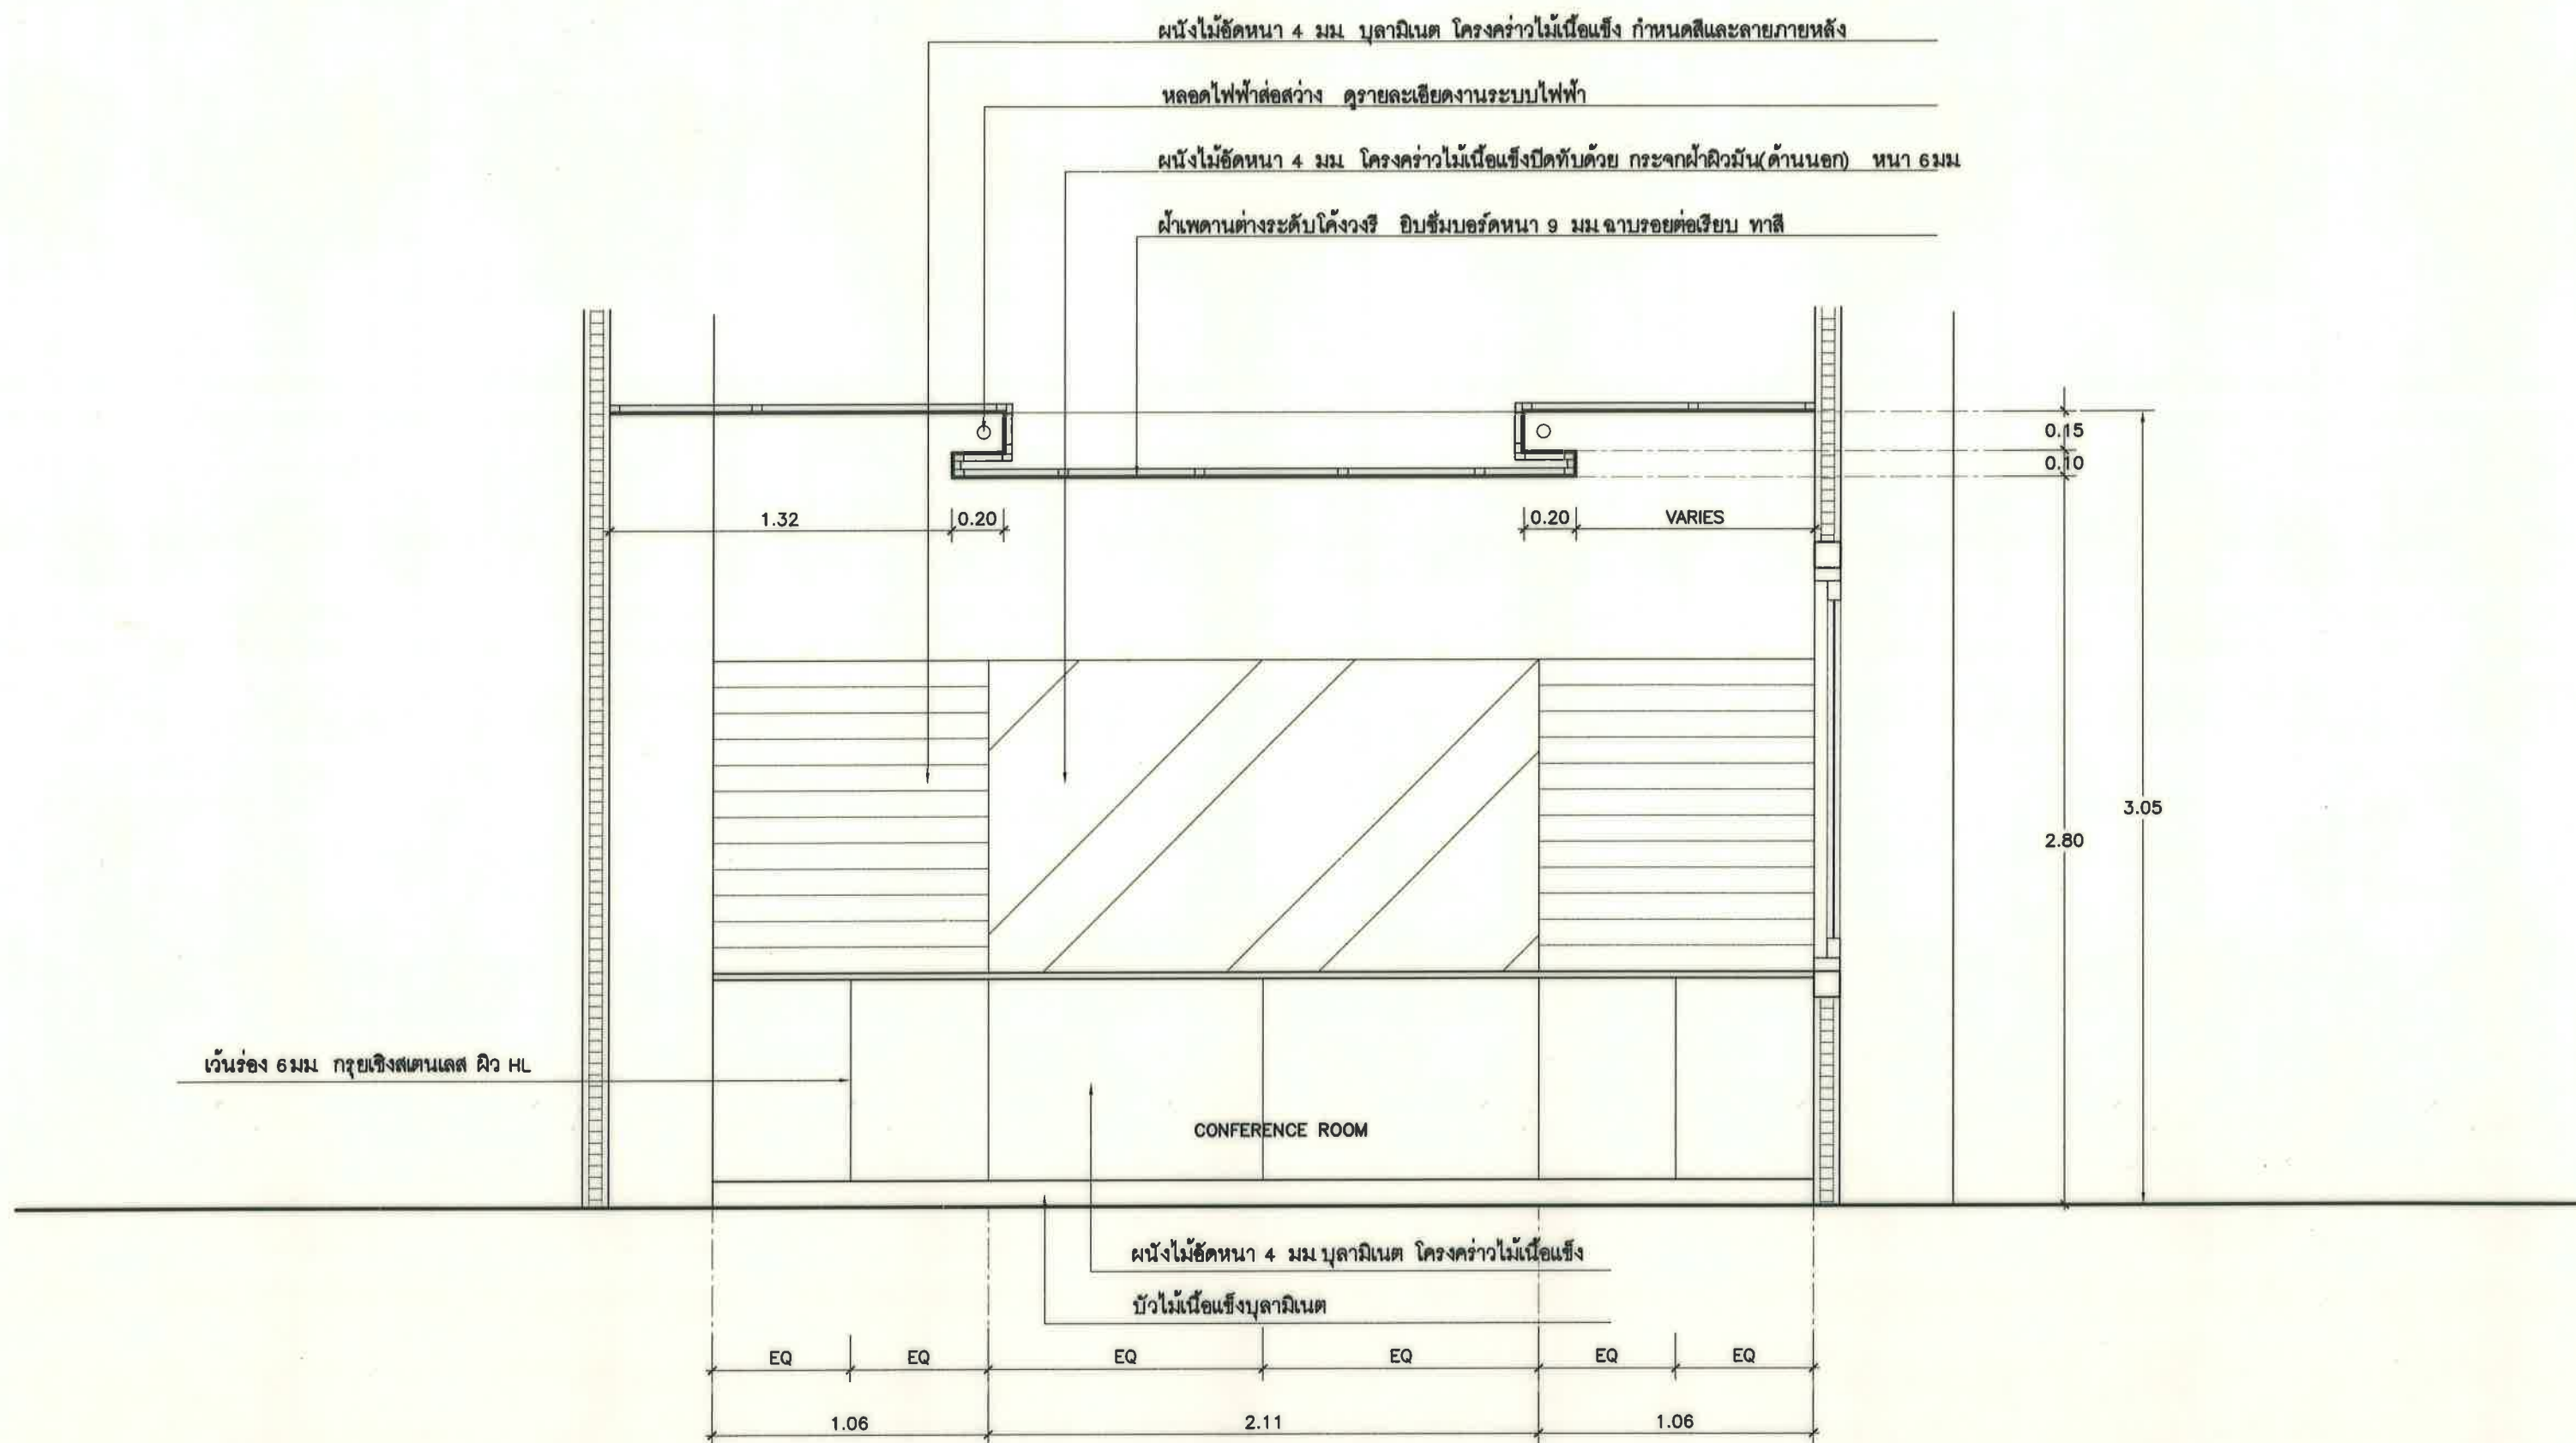


แสดงรูปด้าน ②


มาตราส่วน 1 : 25

Property Management Department ฝ่ายบริหารทรัพย์สิน	เจ้าของโครงการ ฝ่ายพัฒนาผลิตภัณฑ์ระหว่างประเทศ	สถาปนิก	สนั่น นาคนิกร ๓-๘๘๙๖๑๙	วิศวกรระบบไฟฟ้ากำลัง	เฉลิมชัย พงษ์พานิช ๓๖๒๕	วิศวกรระบบป้องกันอัคคีภัย	ประทีป อินทรพัฒน์ ๓๖๒๗	ตรวจ	วิรัช วัฒนวิทย์ ๓๖๒๗	เลขที่แบบ	A-41
	แบบ งานจ้างเหมาก่อสร้างอาคารสถานที่โครงการเคเบิลทีวี ปากบารา อ.ละงู จ.สตูล พร้อมงานติดตั้งระบบปรับอากาศ และงานรื้อถอน	วิศวกรโครงสร้าง	เอกสิทธิ์ จันทะนิตย์ ๓๖๕๗๗๘	วิศวกรระบบควบคุมอัตโนมัติ	พงษ์ศักดิ์ บุญทวี ๓๖๕๗๗๘	วิศวกรระบบดับเพลิงอัตโนมัติ	ปรีชา เหมมัน ๓๖๓๐๑๔	เห็นชอบ	วิรัช วัฒนวิทย์ ๓๖๒๗	แผ่นที่/รวม	41/49
	แสดง แบบขยายฝ้าเพดานและผนังห้องประชุม	วิศวกรระบบสุขาภิบาล	เฉลิมพล อดุลย์บุตร ๓๖๒๕	วิศวกรระบบสื่อสารสัญญาณ	ปานทิพย์ พูนผล	วิศวกรระบบปรับอากาศ	ศุภมิตร ศรีวิวัฒน์ ๓๖๑๐๖๖	อนุมัติ	วิรัช วัฒนวิทย์ ๓๖๒๗		
	แสดงรูปด้าน ②	เขียน	สนั่น นาคนิกร								

45/358

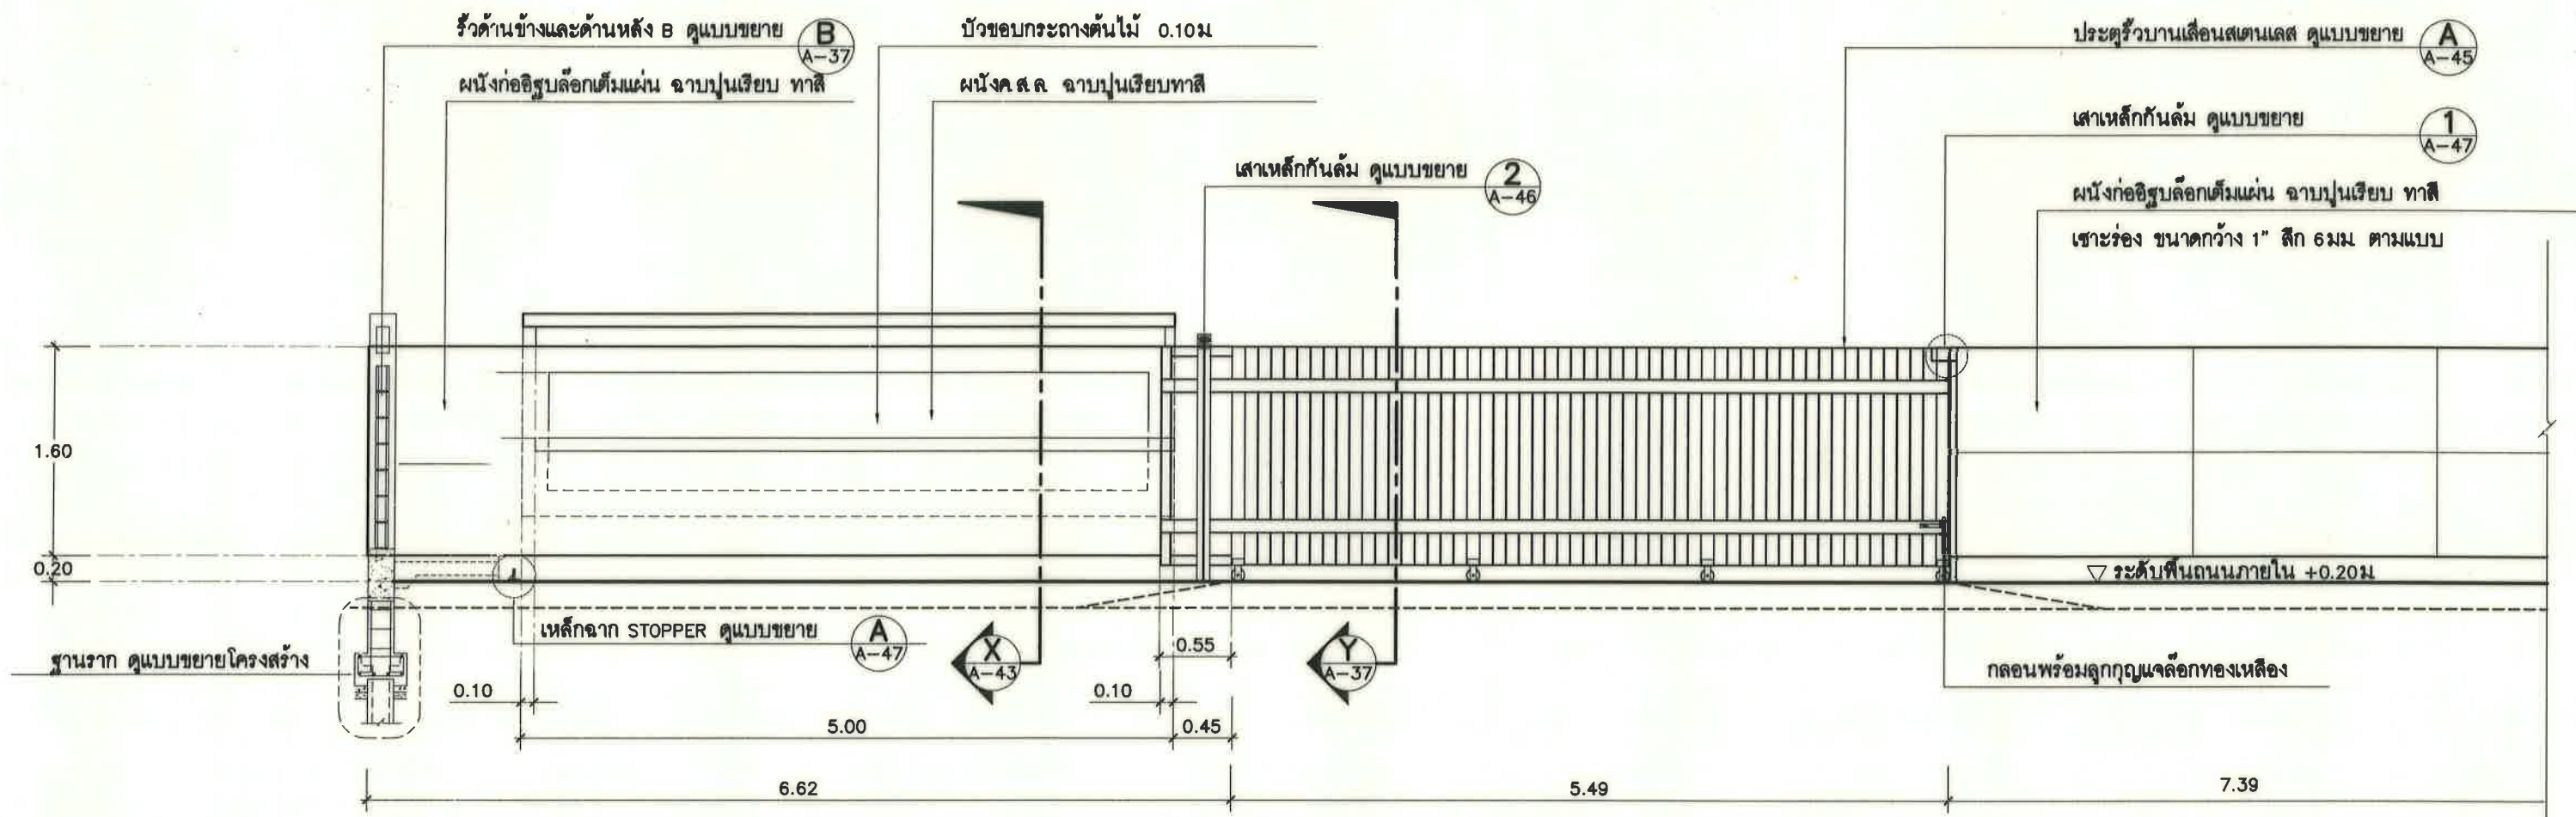

แสดงรูปด้าน 2
มาตราส่วน 1 : 50

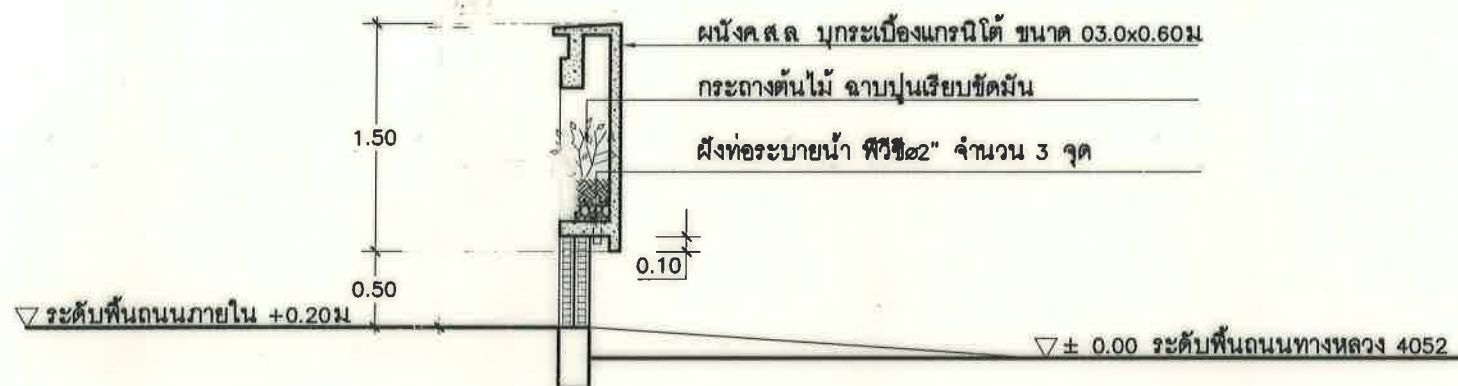


แสดงแนวตัด X
มาตราส่วน 1 : 50

รายการประกอบแบบ ประตูรั้วบานเลื่อน

1. ประตูรั้วบานเลื่อน ขนาด ยาว 5.50ม สูง 1.80ม เส้นเปิดทางเดียว
2. ลูกกลิ้งเหล็ก 110ม HEAVY DUTY อย่างดี ขนาดใหญ่สุด 4 ชุด
3. รางล้อเหล็ก สเตนเลสกลม เชื่อมปิดกับเหล็กฉาก 2"x2" ฝังกับถนนค.ส.ล
4. ติดตั้งกลอนฝังพื้นครบชุด พร้อมปลดกรับกลอนฝังพื้น
5. ขอบด้านข้างติดตั้งยางกันกระแทกขนาด 2 1/2" ข้างละ 3 จุด
6. ทุญแจต้องสายชูทองเหลือง (ทุญแจวงแหวน) 50 มิลลิเมตร หูยาว ยี่ห้อ YALE หรือคุณภาพเทียบเท่า
ตัวถังสีเหลี่ยม/หกเหลี่ยม - แม่ทุญแจ 1 ตัว + ลูกทุญแจ 1 พวง (3 ดอก)
ตัวถังทุญแจทำจากทองเหลืองเกรด A 100% ไม่เป็นสนิม - ตัวถังรูปหกเหลี่ยม

 Property Management Department ฝ่ายบริหารทรัพย์สิน ส่วนอำนวยการวิศวกรรมอาคาร	เจ้าของโครงการ ฝ่ายพัฒนาที่ดินระหว่างประเทศ	สถาปนิก สนั่น นาคนิกร ๖-๓๐๙๖๑๙	วิศวกรระบบไฟฟ้ากำลัง เจริญชัย พงษ์ชากร ๖๖๒๕	วิศวกรระบบป้องกันอัคคีภัย ประทีป อินทรศักดิ์ ๖๗๓๖	ตรวจ 18 มิ.ย. 57	เลขที่แบบ A-43
	แบบ งานจ้างเหมาก่อสร้างอาคารสถานที่โครงการขายเคปิตัล ปากบารา อ.ละงู จ.สตูล พร้อมงานติดตั้งระบบปรับอากาศ และงานรื้อถอน	วิศวกรโครงสร้าง เอกสิทธิ์ จังขระเกียรติ ๕๕๕๗๗๘	จรรยาวัชร ๖๖๓๓๓๓ ๖๖๓๓๓๓	วิศวกรระบบควบคุมอัตโนมัติ พงษ์ศักดิ์ บุญทวี ๖๖๓๓๓๓	เห็นชอบ ๒๖ มิ.ย. ๕๗	แผ่นที่/รวม 43/49
	แสดง แบบขยายรั้ว A	มาตราส่วน 1 : 50	วิศวกรระบบสุขาภิบาล เจริญพล อดุลย์นคร ๖๖๓๓๓๓	วิศวกรระบบปรับอากาศ สุมิตร ศรีวิวัฒน์ ๖๖๓๓๓๓	อนุมัติ ๒๗ มิ.ย. ๕๗	
	แสดงรั้วด้านหน้า 2	เขียน สนั่น นาคนิกร				

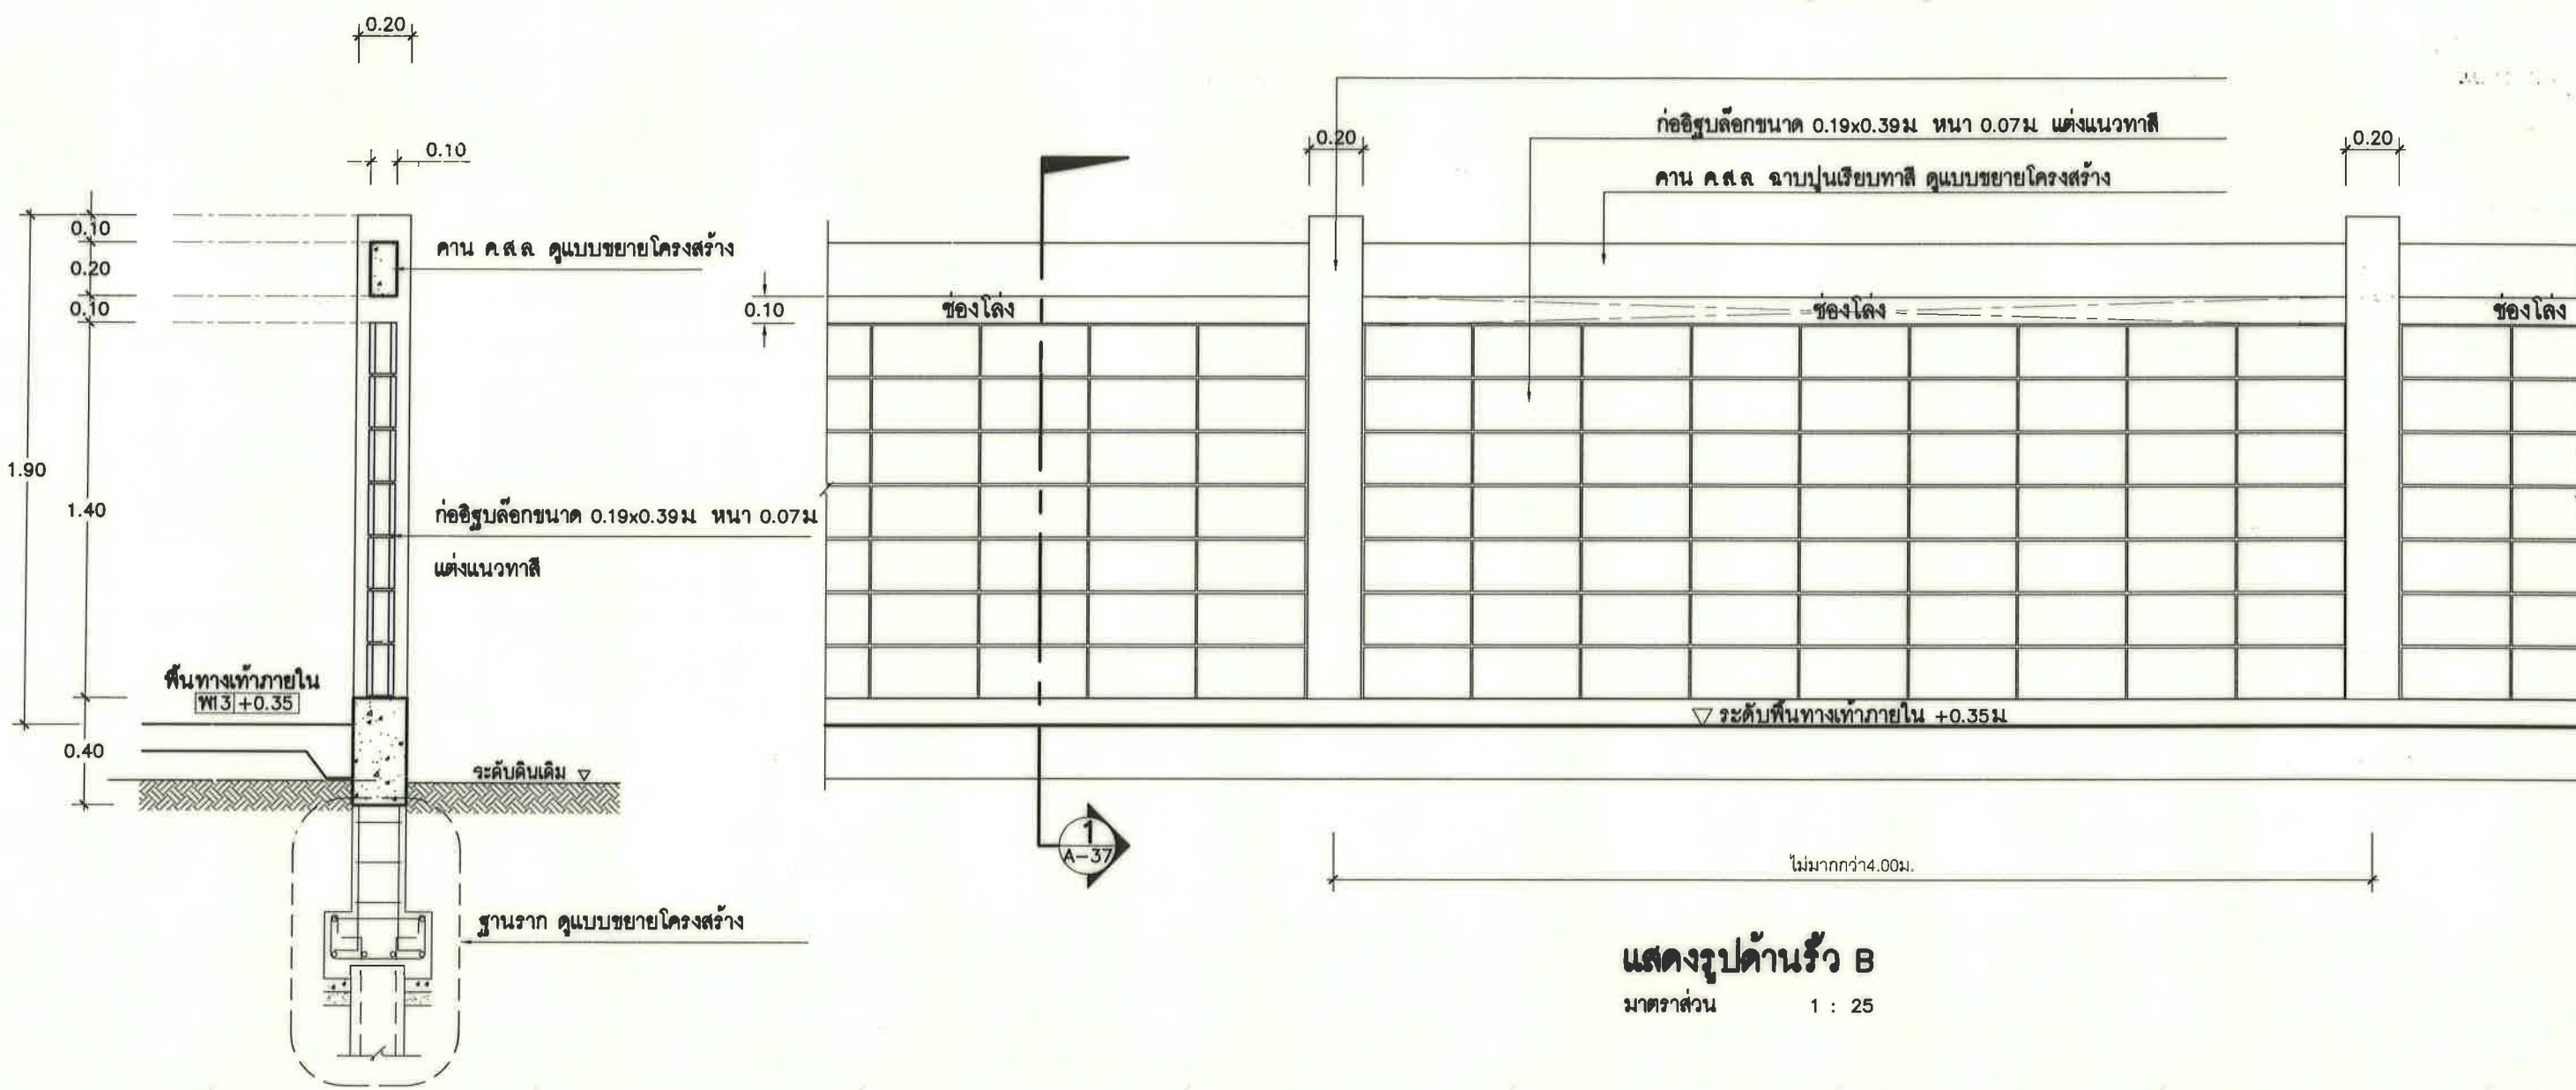


แสดงรูปด้านรั้ว B

มาตราส่วน 1 : 25



รูปด้าน 1
มาตราส่วน 1 : 50

 Property Management Department ฝ่ายบริหารทรัพย์สิน ส่วนออกใบอนุญาตอาคาร	เจ้าของโครงการ ฝ่ายพัฒนาผลิตภัณฑ์ระหว่างประเทศ	สถาปนิก	สนั่น นาคนิกร ๓-๓๓๙๖๑๙	วิศวกรระบบไฟฟ้ากำลัง	เฉลิมชัย พงษ์ชากร ๓๓๓ ๖๖๒๕	วิศวกรระบบป้องกันอัคคีภัย	ประทีป อินทรศักดิ์ ๓๓๓ ๖๗๐๗	ตรวจ	ผจ.สอ.ทพ. ๑๘/๐๓/๕๖	เลขที่แบบ A-44 แผ่นที่/รวม 44/49
	แบบ งานจ้างเหมาก่อสร้างอาคารสถานที่โครงการเคเบิ้ลไทร์ ปากบารา อ.ละงู จ.สตูล พร้อมงานติดตั้งระบบปรับอากาศ และงานรื้อถอน	วิศวกรโครงสร้าง	เอกสิทธิ์ จิงจางเกียรติ ๓๓๓ ๕๗๗๘	วิศวกรระบบควบคุมอัตโนมัติ	พงษ์ศักดิ์ บุญทวี ๓๓๓ ๕๘๗๔	วิศวกรระบบดับเพลิงอัตโนมัติ	ปรีชา เหมมัน ๓๓๓ ๓๐๑๔	เห็นชอบ	ผจ.สอ.ทพ. ๑๘/๐๓/๕๖	
	แสดง	มาตราส่วน	เขียน	วิศวกรระบบสุขาภิบาล	เฉลิมพล อุดมบุตร ๓๓๓ ๒๑๐๓๕	วิศวกรระบบปรับอากาศ	สุมิตร ศรีวิพัฒน์ ๓๓๓ ๑๐๖๖๖	อนุมัติ	ผจ.ทพ. ๒๗/๐๓/๕๖	
	แบบขยายรั้ว B	เขียน	สนั่น นาคนิกร					รูชาติ ชัยสุข		

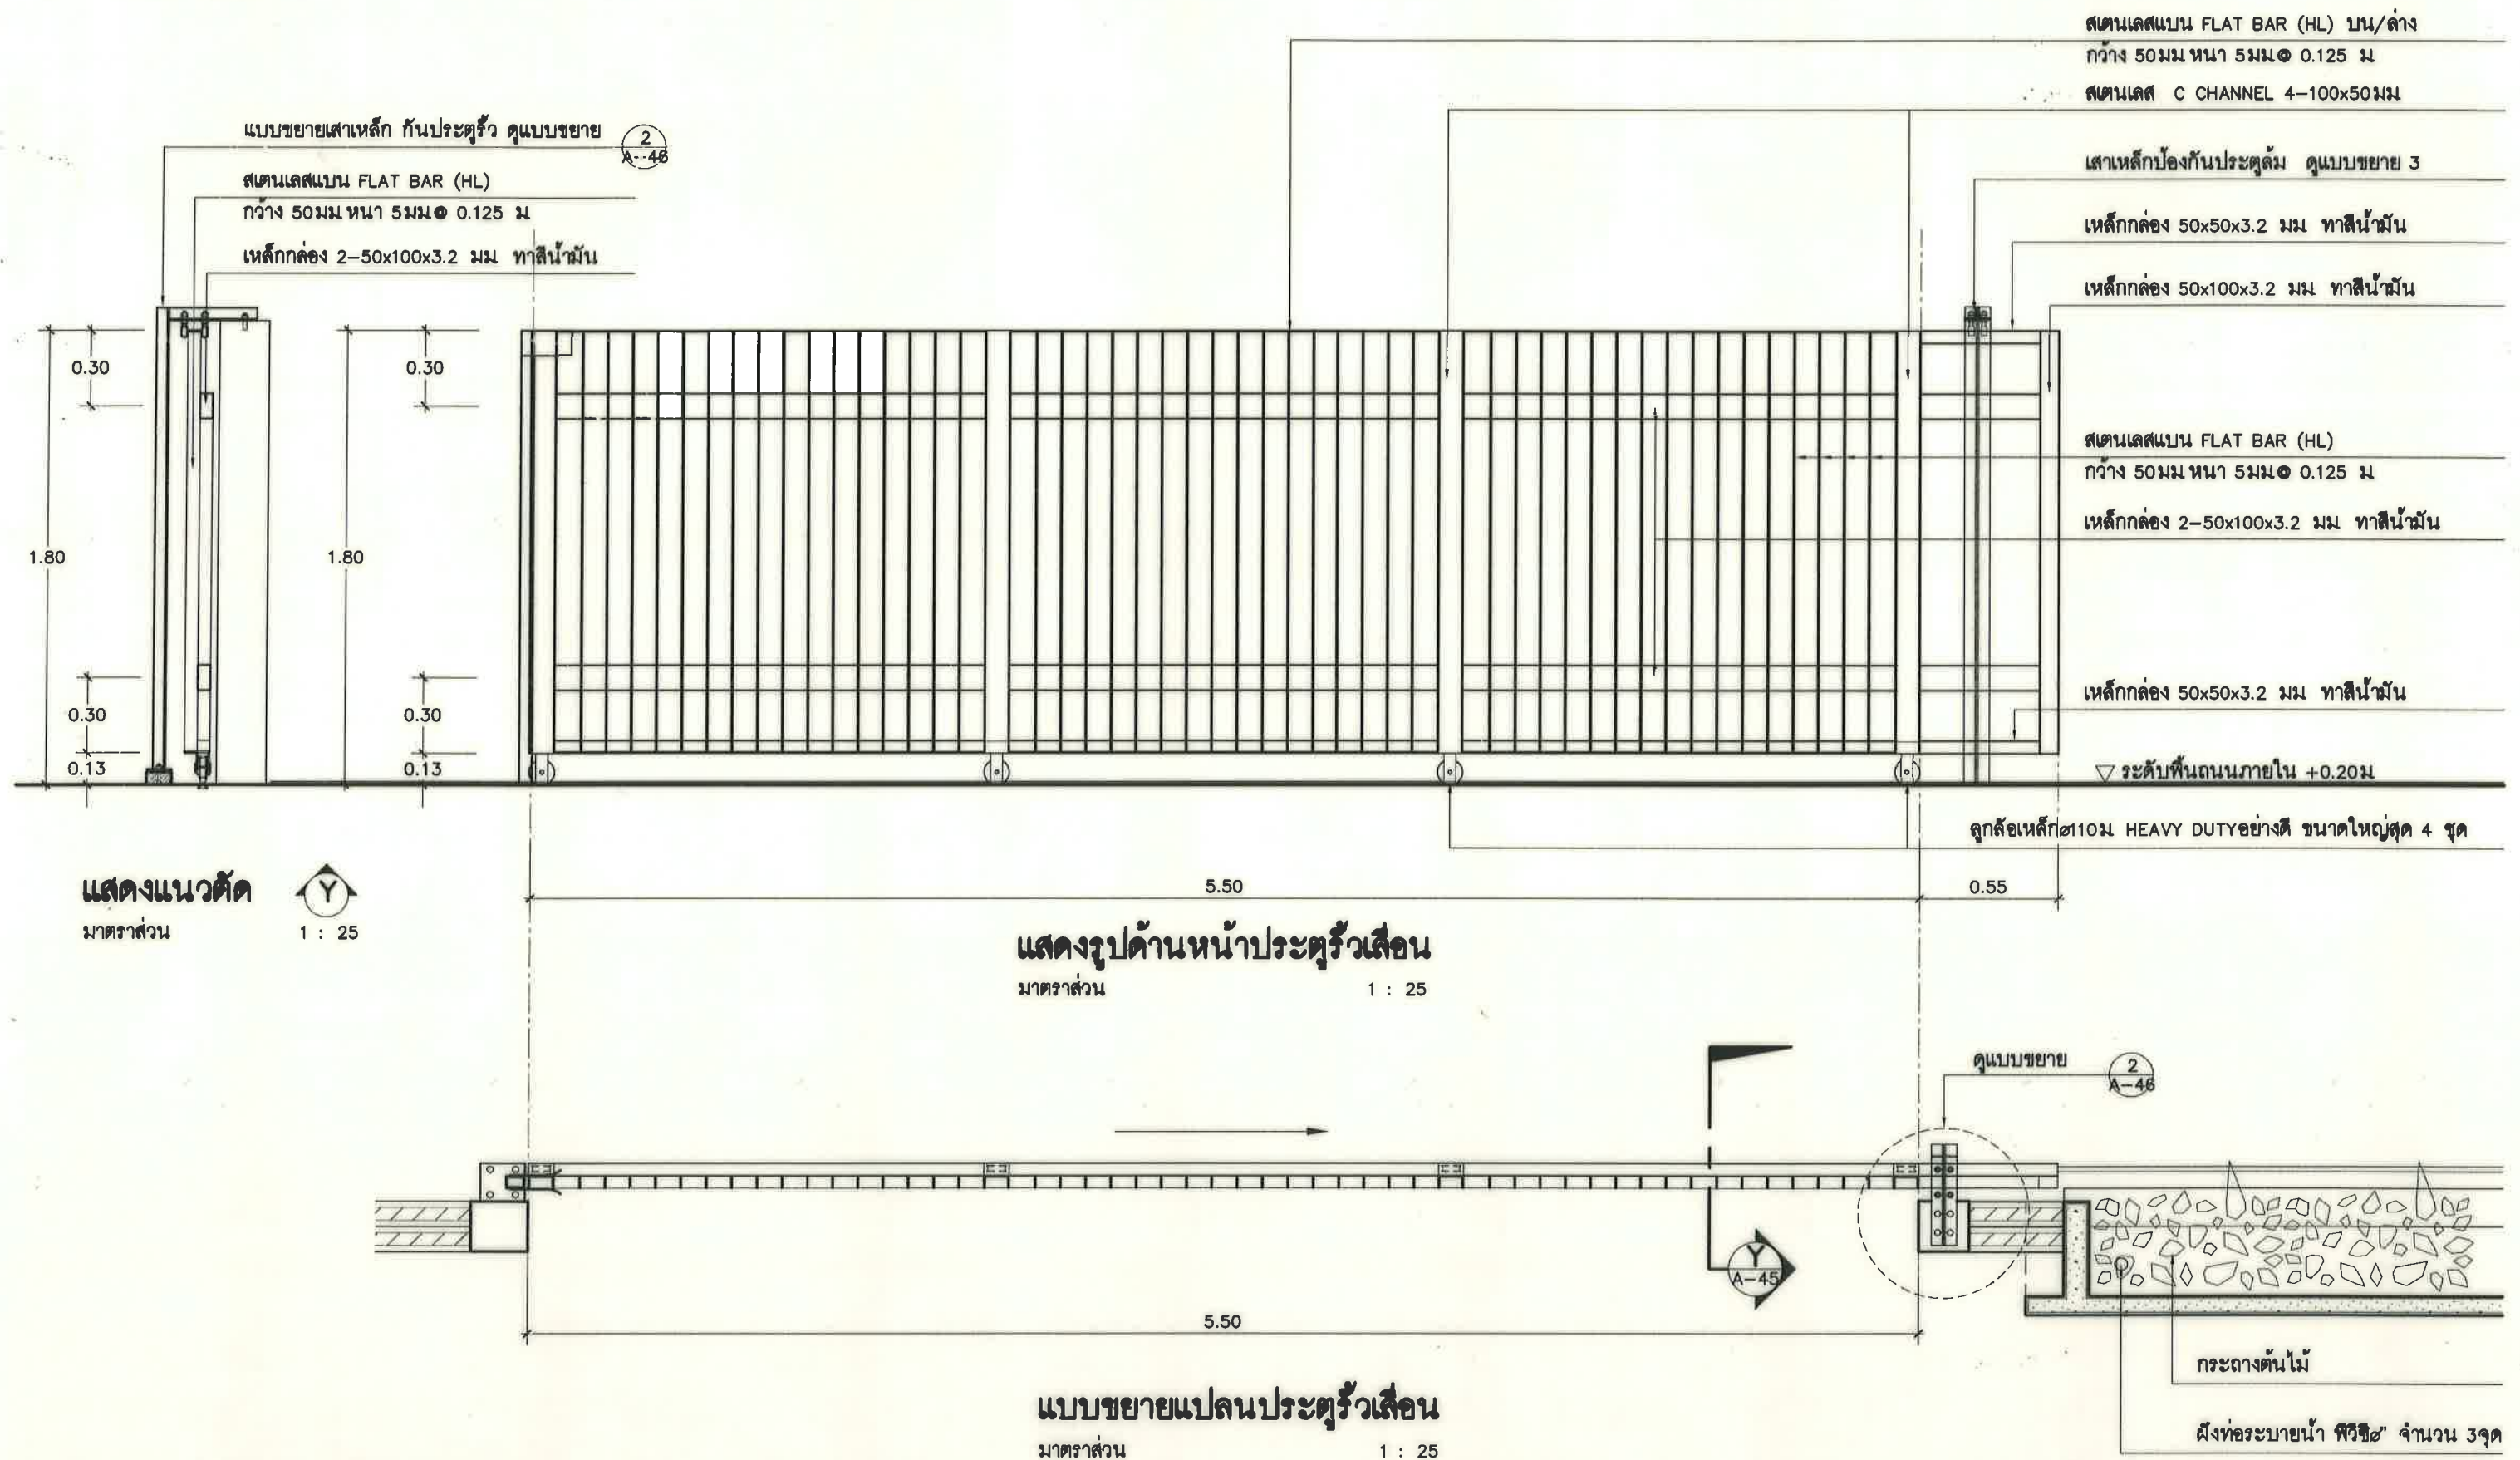

 TOT Property Management Department ฝ่ายบริหารทรัพย์สิน ส่วนออกแบบวิศวกรรมอาคาร	เจ้าของโครงการ	ฝ่ายพัฒนาผลิตภัณฑ์ระหว่างประเทศ	สถาปนิก	สนั่น นาคนิก ภา-๑๑๙๖๑๙	วิศวกรระบบไฟฟ้ากำลัง	เฉลิมชัย พงกษากร ภาท 6625	วิศวกรระบบป้องกันอัคคีภัย	ประทีป อินทรศักดิ์ ภาท 6707	ตรวจ	วิรัชพงศ์ จิตยาภัก	ผจ.สอทพ.	เลขที่แบบ
	แบบ	งานจ้างเหมาก่อสร้างอาคารสถานีโครงการเคเบิลไฟฟ้า ปากบารา	วิศวกรโครงสร้าง	เอกสิทธิ์ จิงขจรเกียรติ สย 5778	วิศวกรระบบควบคุมอัตโนมัติ	พงษ์ศักดิ์ บุญทวี ภาท 5874	วิศวกรระบบดับเพลิงอัตโนมัติ	ปรีชา เหมมัน สก 3014	เห็นชอบ	กฤษ มาประเสริฐ	ผจ.สอทพ.	A-45
	แสดง	มาตรฐาน 1 : 25	วิศวกรระบบสุขาภิบาล	เฉลิมพล อุดกยบุตร ภา 21035	วิศวกรระบบสื่อสารสัญญาณ	ปานทิพย์ พูนผล	วิศวกรระบบปรับอากาศ	สุมิตร ศรีวิวัฒน์ ภาท 10666	อนุมัติ	รุชติ ชัยสุข	ผจ.ทพ.	แผนที่/รวม
	แบบขยายแปลนประตูรั้วเลื่อน	เขียน	สนั่น นาคนิก								ผจ.ทพ.	45/49





49/358

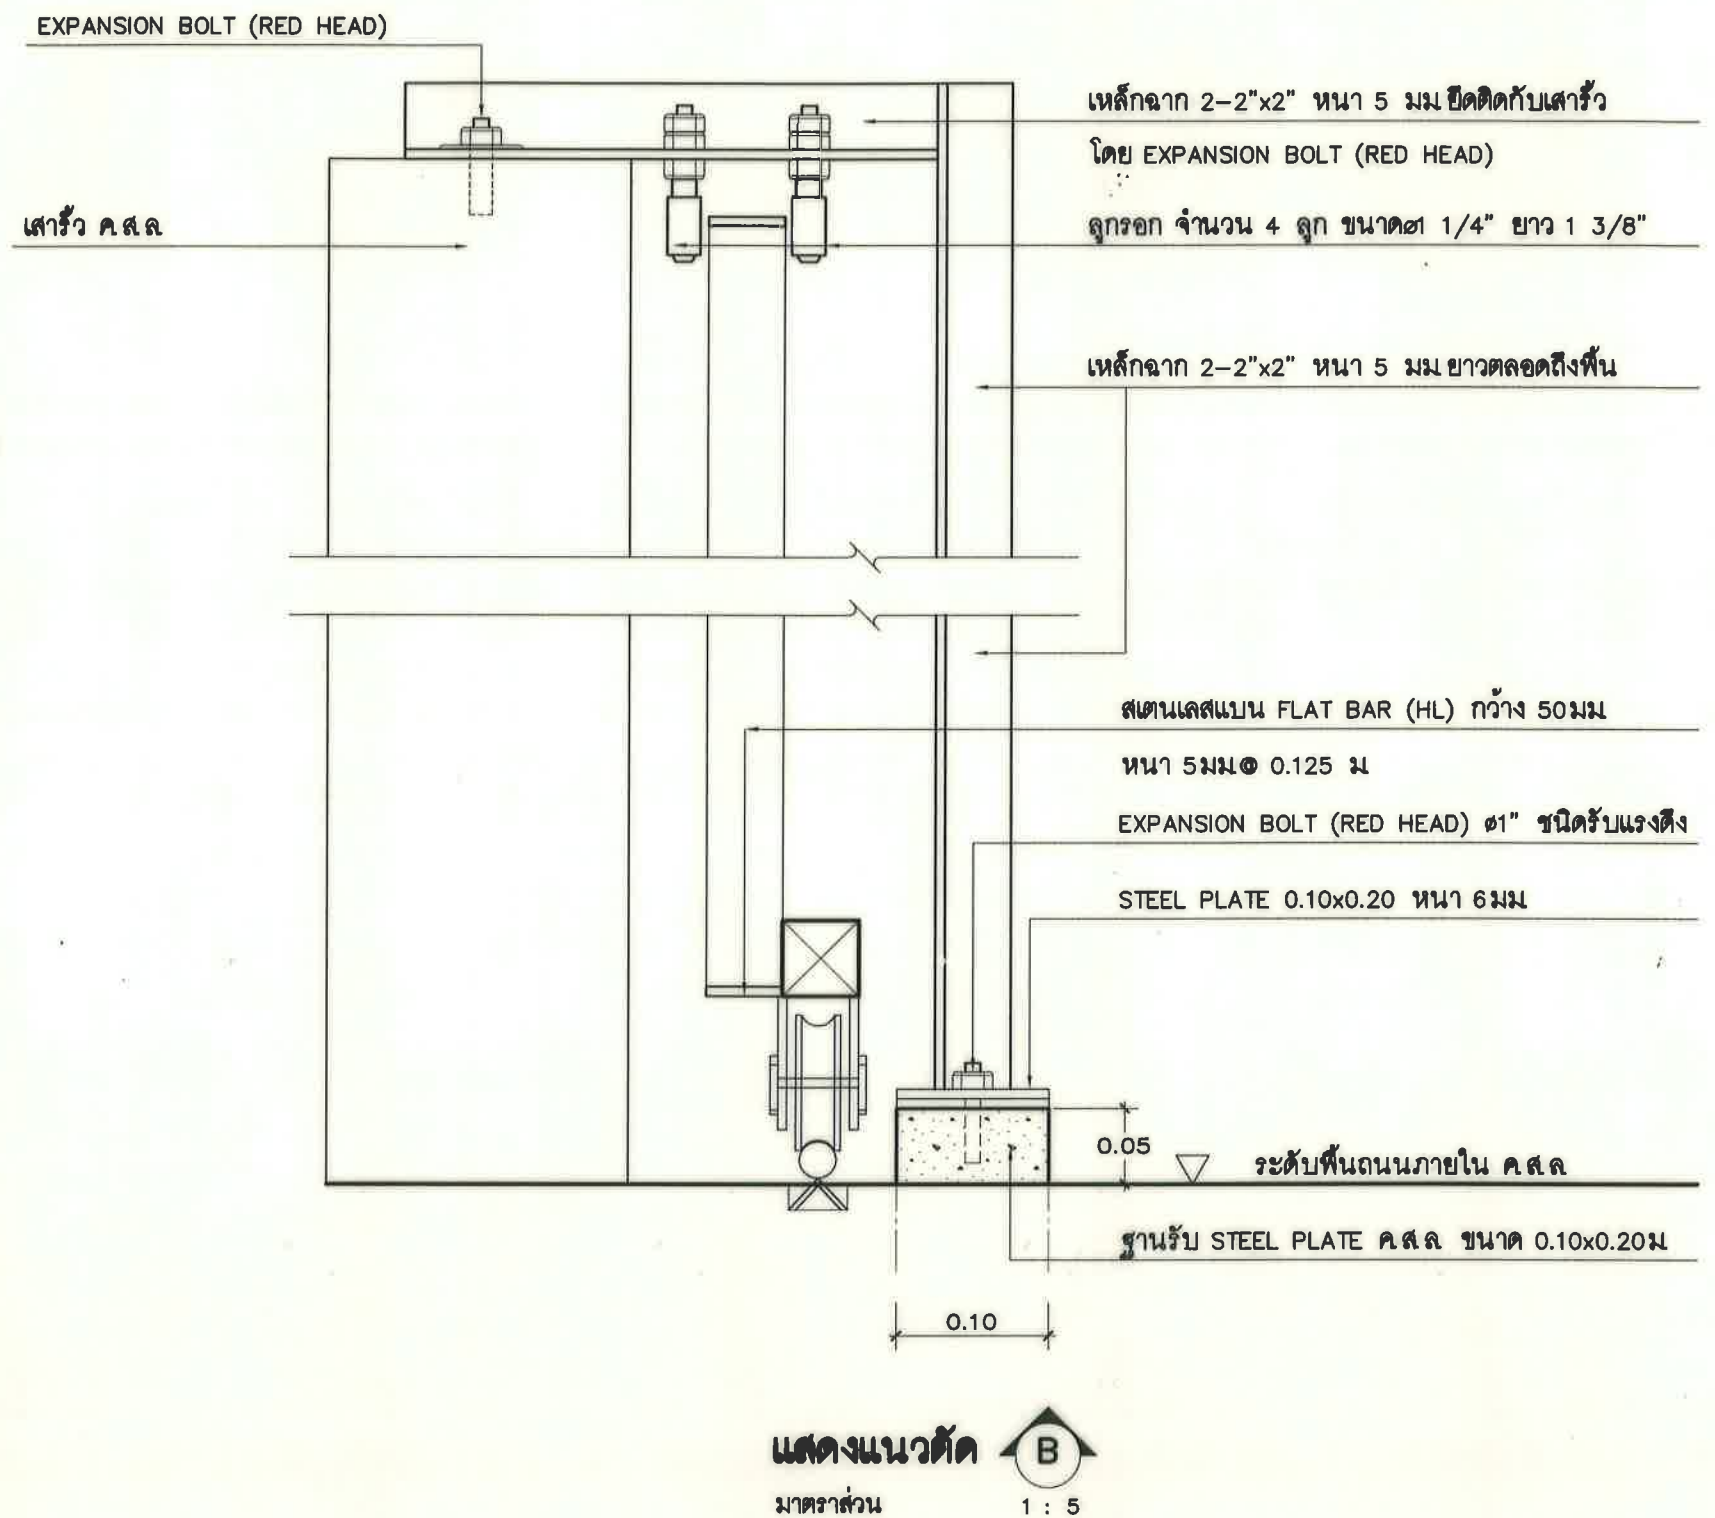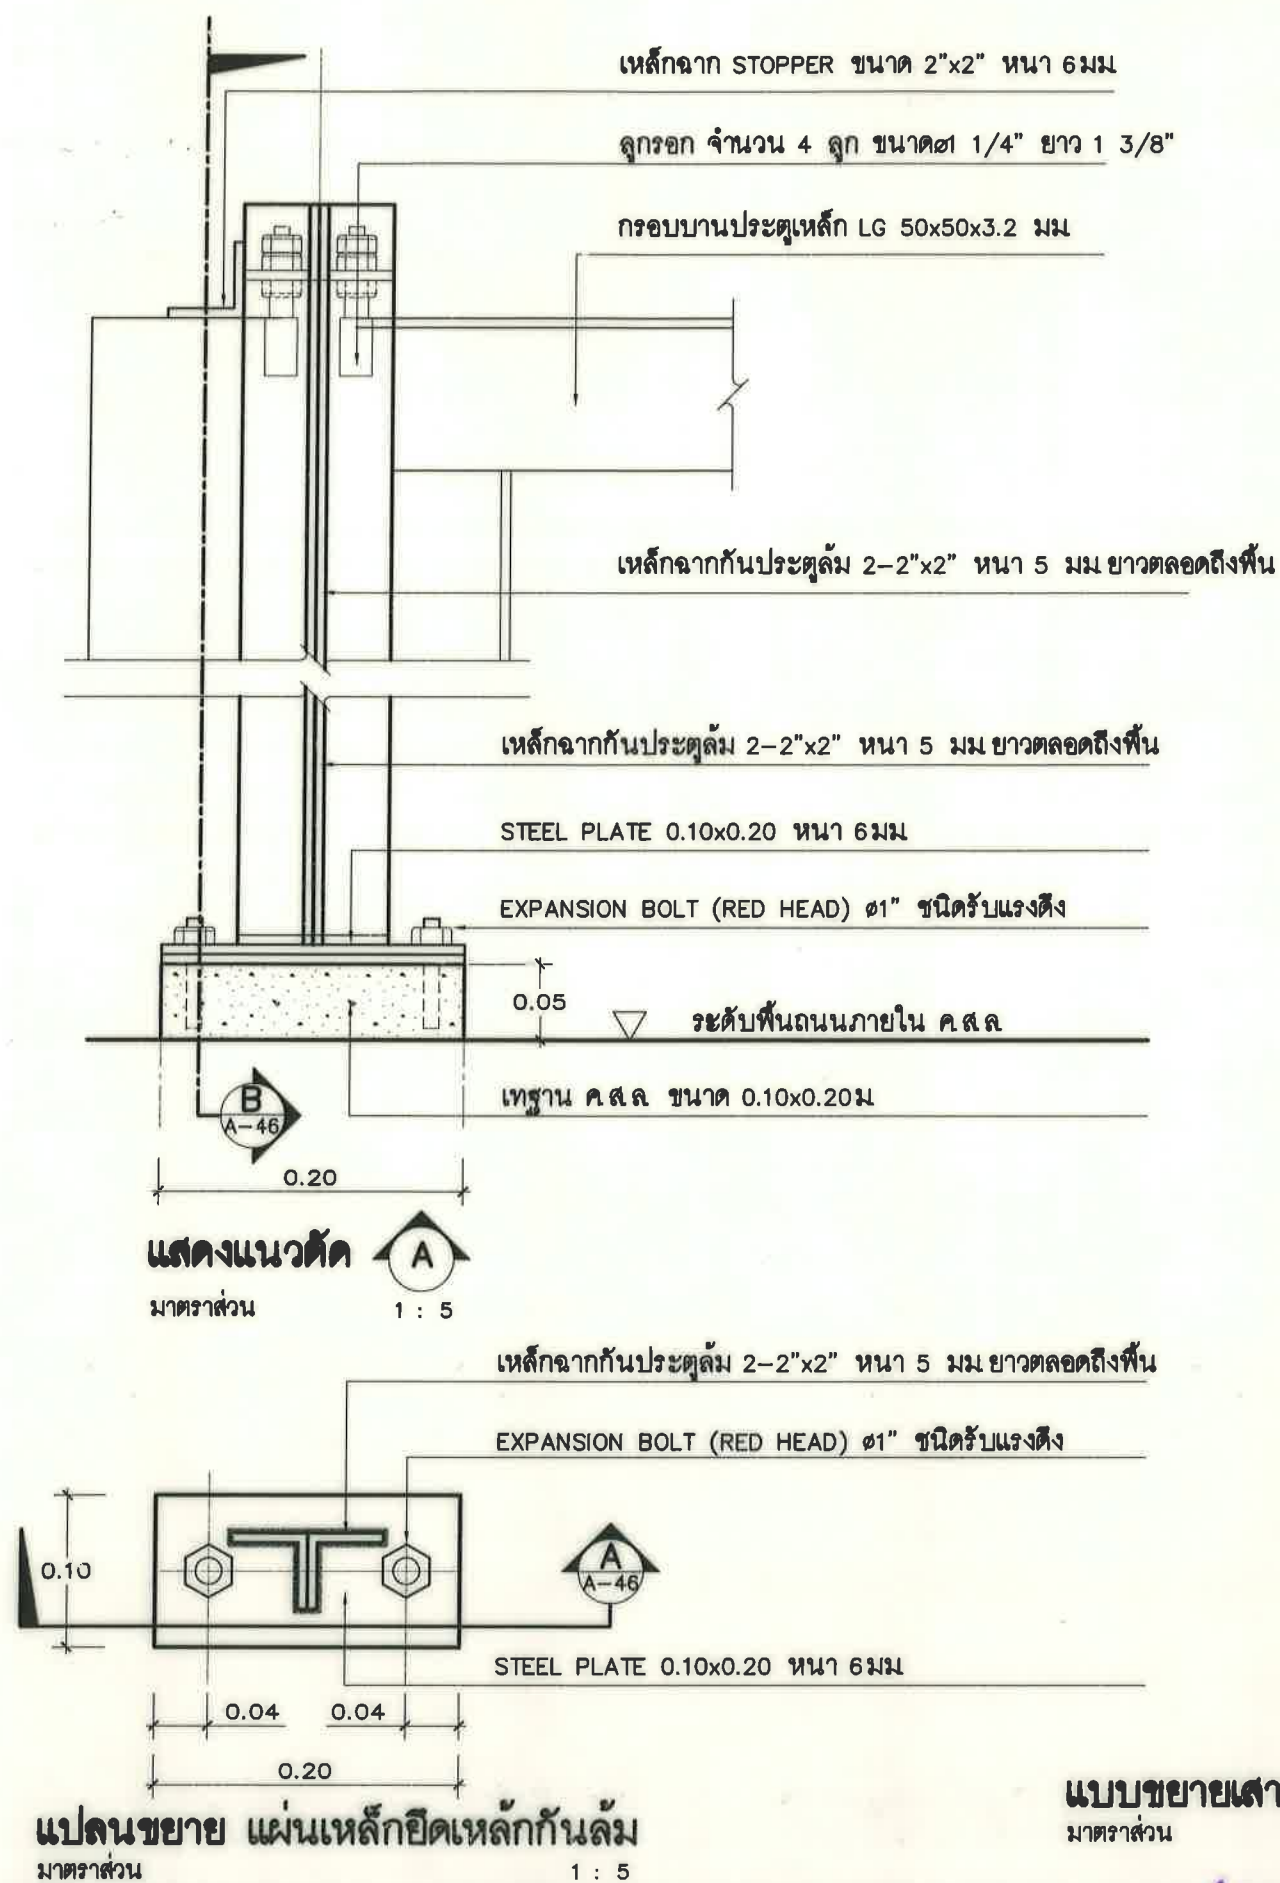

แบบขยายเสาเหล็ก กันประตูรั่ว


มาตราส่วน 1 : 5

TOT Property Management Department ฝ่ายบริหารทรัพย์สิน ส่วนออกแบบวิศวกรรมอาคาร	เจ้าของโครงการ	ฝ่ายพัฒนาผลิตภัณฑ์ระหว่างประเทศ	สถาปนิก	สนั่น นาคนิกร ๙-๙๘๙๖๑๙	วิศวกรระบบไฟฟ้ากำลัง	เฉลิมชัย พงษ์ชากร ๙๙๙๘๕	วิศวกรระบบป้องกันอัคคีภัย	ประทีป อินทรศักดิ์ ๙๙๙๘๗	ตรวจ	ผจ.สอ.พ.	เลขที่แบบ
	แบบ	งานจ้างเหมาก่อสร้างอาคารสถานประกอบการเคเบิลทีวี ปากบารา	วิศวกรโครงสร้าง	เอกสิทธิ์ จิระกรเกียรติ ๙๙๙๗๗๘	จระเขย เวชวิทย์คุณ ๙๙๙๙๐๙	วิศวกรระบบควบคุมอัตโนมัติ	พริษา เหมมัน ๙๙๙๙๑๔	เห็นชอบ	ผจ.สอ.พ.	๙๘/๙๙๙๙๙๙	A-46
	แสดง	อลง จ.สตุล พร้อมงานติดตั้งระบบปรับอากาศ และงานรื้อถอน	วิศวกรระบบสุขาภิบาล	เฉลิมพล อุดมย์นร ๙๙๙๙๑๕	ปานทิพย์ พูนผล	วิศวกรระบบสื่อสารสัญญาณ	สุมิตร ศรีวิวัฒน์ ๙๙๙๙๑๖	อนุมัติ	ผจ.สอ.พ.	๙๘/๙๙๙๙๙๙	๙๘/๙๙๙๙๙๙
	แบบขยายเสาเหล็ก กันประตูรั่ว	มาตราส่วน 1 : 5	เขียน	สนั่น นาคนิกร				ชราณี ชัย			๙๘/๙๙๙๙๙๙

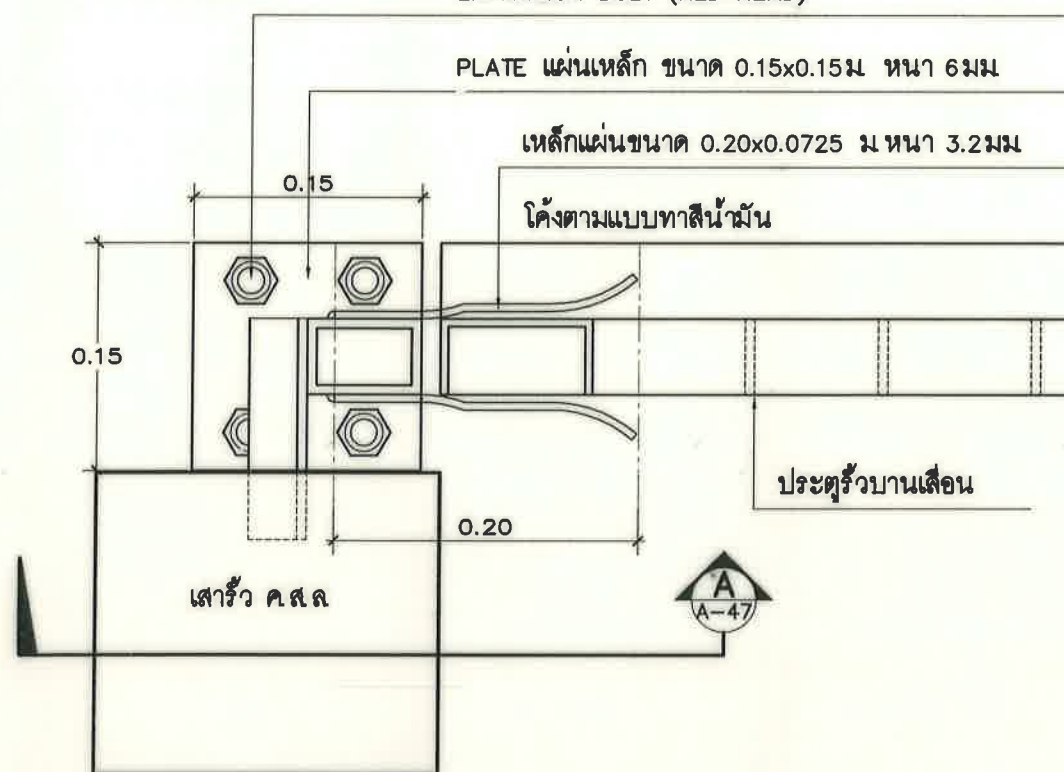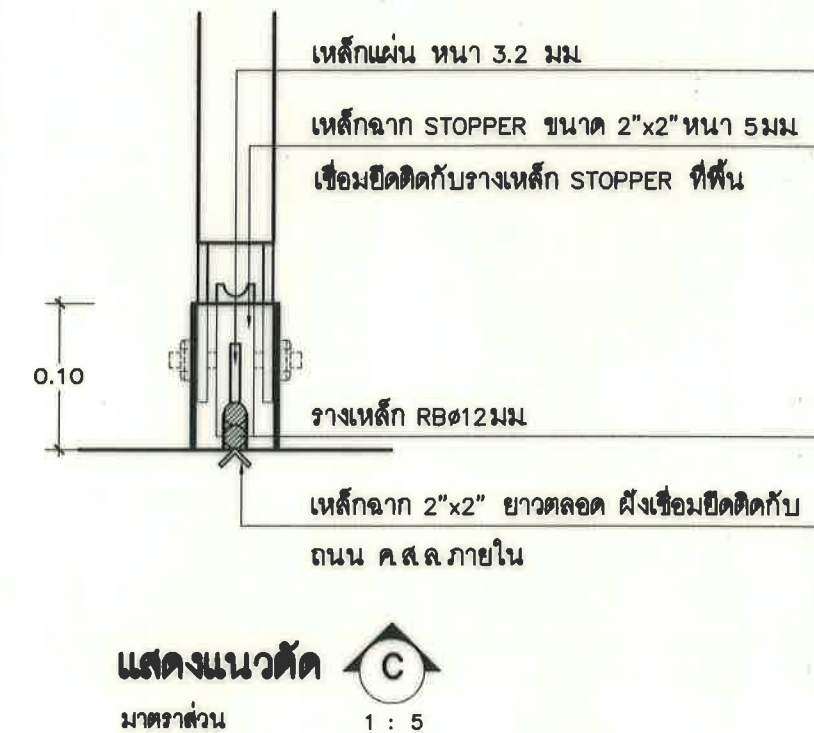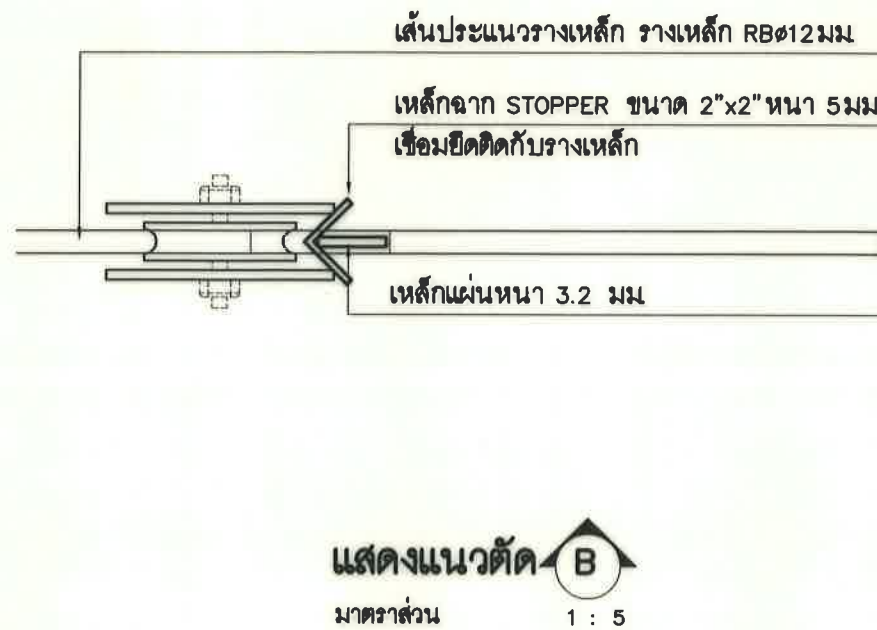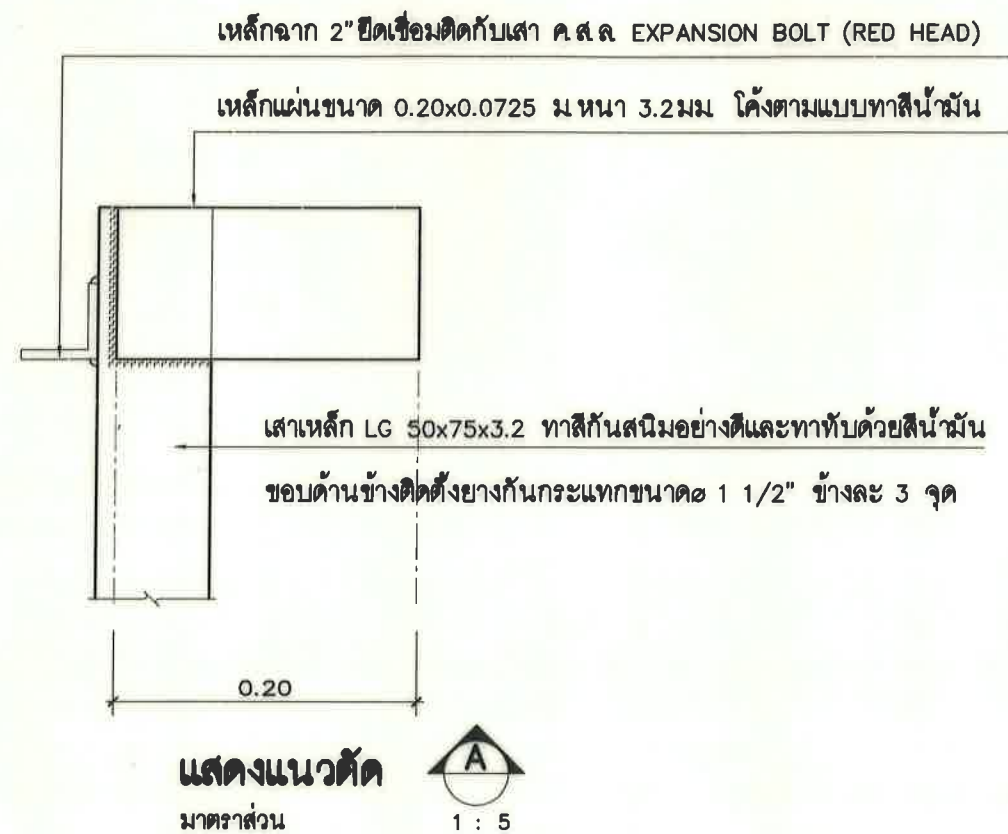

แปลนแบบขยายเสาเหล็ก กันชนประตูลูกบิดเลื่อน

มาตราส่วน 1 : 5

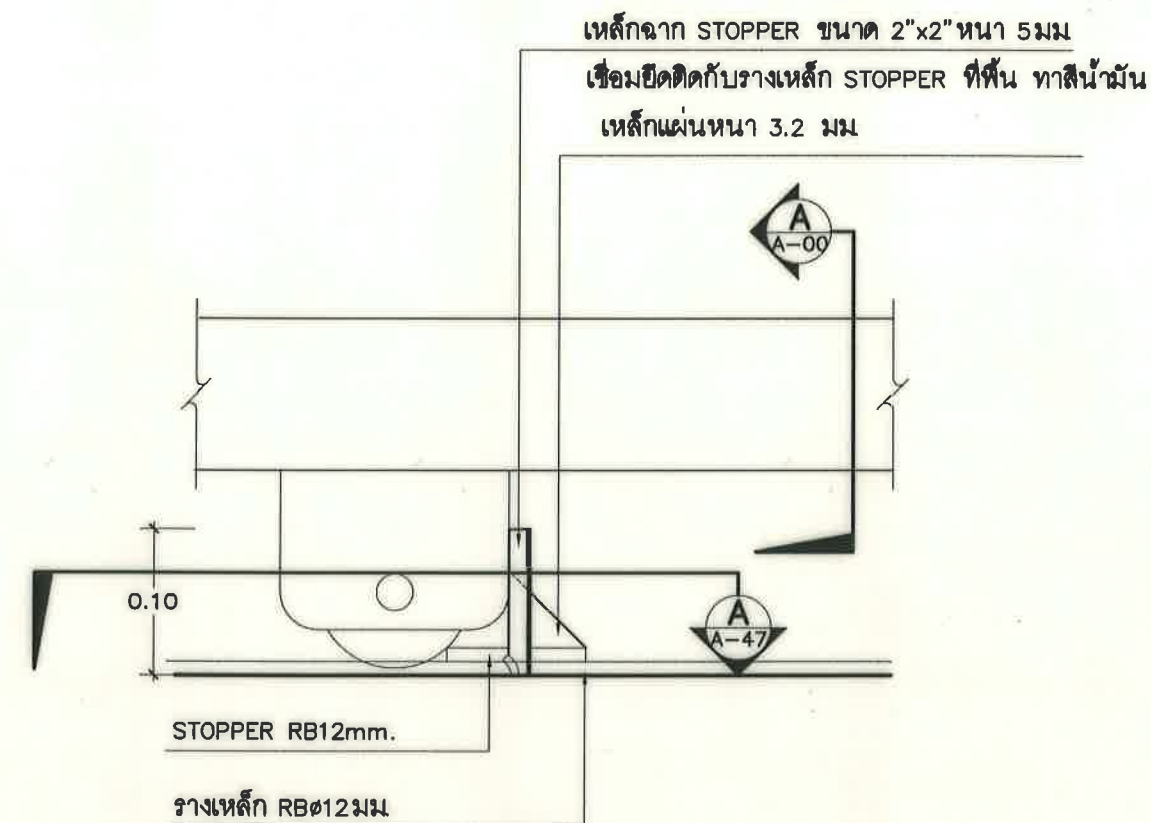


แปลนแบบขยายSTOPPER ประตูลูกบิดเลื่อน

มาตราส่วน 1 : 5

 Property Management Department ฝ่ายบริหารทรัพย์สิน ส่วนออกแบบวิศวกรรมอาคาร	เจ้าของโครงการ	ฝ่ายพัฒนาผลิตภัณฑ์ระหว่างประเทศ	สถาปนิก	สนั่น นาคนิกร ภา-สอ.9619	วิศวกรระบบไฟฟ้ากำลัง	เฉลิมชัย พงกษาร ภาฟก.6625	วิศวกรระบบป้องกันอัคคีภัย	ประทีป อินทรศักดิ์ ภาฟค.6707	ตรวจ	วิรัชพงศ์ ภิทยามาศ 18.04/57	เลขที่แบบ	A-47
	แบบ	งานจ้างเหมาก่อสร้างอาคารสถานีโครงการเคเบิลไต่หน้าปากบารา อ.ละงู จ.สตูล พร้อมงานติดตั้งระบบปรับอากาศ และงานรื้อถอน	วิศวกรโครงสร้าง	เอกสิทธิ์ จิงขจรเกียรติ สย.5778	วิศวกรระบบควบคุมอัตโนมัติ	พงษ์ศักดิ์ บุญทวี ภาฟค.5874	วิศวกรระบบดับเพลิงอัตโนมัติ	ปรีชา เหมมื่น สก.3014	เห็นชอบ	ศิระ มาประเสริฐ 06.04/57	แผนที่/รวม	47/49
	แสดง	แบบขยายเสาเหล็ก ประตูหัว	มาตราส่วน	1 : 5	วิศวกรระบบสุขาภิบาล	เฉลิมพล อดุลย์บุตร ภาข.21035	วิศวกรระบบปรับอากาศ	สุมิตร ศรีวิวัฒน์ ภาค.10686	อนุมัติ	ชัชชาติ ชัยสุข 07.07/57		
		แบบขยายSTOPPER	เขียน	สนั่น นาคนิกร								

โต๊ะประชุม : MT-01 ขนาด 1800 x 1280 x 19 mm. จำนวน 1 โต๊ะ
ขาโต๊ะสำหรับท็อปสีก 128 ซม.

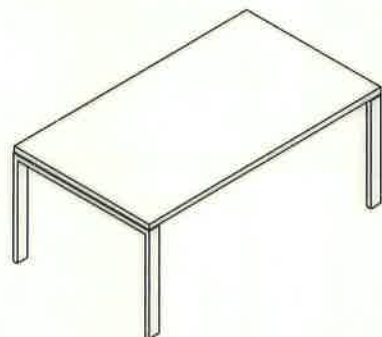

โต๊ะทำงาน : T-01 (A-FLASH) (ขาพับเก็บได้) พร้อมแผ่นบังตา จำนวน 6 โต๊ะ
ขนาด : กว้าง 150 x ลึก 60 x สูง 75 cm.



เก้าอี้สำนักงาน CH-01 : เก้าอี้สำนักงาน พนักพิงกลางมีเท้าแขน จำนวน 6 ตัว
CH-02 : เก้าอี้สำนักงาน พนักพิงเดี่ยวและไม่มีเท้าแขน จำนวน 6 ตัว



วัสดุและโครงสร้าง

แผ่นหน้าโต๊ะ : ไม้ Particle Board หน้า 19 มิลลิเมตร เคลือบผิวด้วย Melamine Resin Film ด้วยระบบ Short Cycle หรือลามิเนตปิดขอบด้วย HARD PVC. EDGE สีเดียวกับผิวที่ใช้เคลือบหน้า 2 mm. ลบมุมมนด้วยเครื่องจักร ติดฝาครอบรูร้อยสายไฟกลม
โครงขาโต๊ะ : รูปตัว "U" ทำมาจากเหล็กกล่อง ขนาด 80x30 มม หน้า 2 มม ฟันสีเทา (Light Gray) แบบ Epoxy Powder Coating อบด้วยความร้อนสูง
คันรับหน้าโต๊ะ : คัน ี่มาจากเหล็กแผ่นหนา 2 มม เคลือบผิวด้วยสีเทา (Light Gray) แบบ Epoxy Powder Coating อบด้วยความร้อนสูง

วัสดุและโครงสร้าง

แผ่นหน้าโต๊ะ : ไม้ Particle Board หน้า 25 มิลลิเมตร เคลือบผิวด้วย Melamine Resin Film ด้วยระบบ Short Cycle ปิดขอบด้วย HARD PVC.EDGE สีเดียวกับผิวที่ใช้เคลือบหน้า 1 mm. ลบมุมมนด้วยเครื่องจักร
โครงขาโต๊ะ : ฐานขาผลิตมาจากเหล็กกลมขนาด ๑ 3/8 มิลลิเมตร รูปโครเมียมเชื่อมติดกับขาตั้งผลิตจากเหล็กกลม ขนาด ๑ 3/2 มิลลิเมตร รูปโครเมียม
คันรับหน้าโต๊ะ : รับน้ำหนักผลิตจากเหล็กสี่เหลี่ยมขนาด 32x32 ฟันเคลือบ Epoxy Coating
ปุ่มรองขา : ผลิตจากเหล็กเพรสขึ้นรูปยึดติดกับน็อตตัวผู้เกลียว 10 มม สามารถปรับเอียงองศาได้ด้านล่างครอบปิดกับพลาสติกติดขึ้นรูปสีดำ

วัสดุและโครงสร้าง

ที่นั่ง : ผลิตจากไม้ขัดเพรส ขึ้นรูปตามแบบติดทับด้วย PU โฟม หุ้มภายนอกด้วยผ้าตาข่ายสีดำ
พนักพิง : ผลิตจากพลาสติกติดขึ้นรูป โดยมีช่องระบายอากาศกลางหลัง ติดทับด้วย PU โฟม หุ้ม ภายนอกด้วยผ้าตาข่ายสีโหล่อกหลายสี
เท้าแขน : สำหรับแผ่นรองแขน ผลิตจาก PU โฟมสีดำติดขึ้นรูปตามแบบ ส่วนที่เป็นก้านแขนทำจาก Polypropylene ติดขึ้นรูป ประกอบเข้ากับแผ่นรองแขน ติดตั้งเข้าได้เบาะด้วยวิธีการยิงสกรู เท้าแขนสามารถปรับสูง-ต่ำได้
ระบบโยก : เป็นระบบ synchronized คือพนักพิง และเบาะรองนั่งโยกอิสระต่อกัน พร้อมติดตั้ง ระบบ Back Lock
ขา : แบบ 5 แฉก ผลิตจากอลูมิเนียม Die-Casting
ลูกล้อ : แบบ Twin Wheel Castor ผลิตจาก Nylon-6 สีดำ ประกอบเข้ากับขาแบบเดือยเสียบ

 Property Management Department ฝ่ายบริหารทรัพย์สิน ส่วนออกใบวิศวกรอาคาร	เจ้าของโครงการ	ฝ่ายพัฒนาผลิตภัณฑ์ระหว่างประเทศ	สถาปนิก	สนั่น นาคนิก ๓-๕๕๖๑๙	วิศวกรระบบไฟฟ้ากำลัง	เฉลิมชัย พงกษากร ๓๗๕ ๕๕๖๒๕	วิศวกรระบบป้องกันอัคคีภัย	ประทีป อินทรศักดิ์ ๓๗๕ ๕๕๖๒๕	ตรวจ	วิมลพร วัฒนาศ ๓๗๕ ๕๕๖๒๕	เลขที่แบบ	A-48
	แบบ	งานจ้างเหมาก่อสร้างอาคารสถานที่โครงการเคเบิลไต่ป่า ปากบารา อ.ละงู จ.สตูล พร้อมงานติดตั้งระบบปรับอากาศ และงานรื้อถอน	วิศวกรโครงสร้าง	เอกสิทธิ์ จิงจางเกียรติ ๕๕๖๕๗๗๘	วิศวกรระบบควบคุมอัตโนมัติ	พงษ์ศักดิ์ บุญทวี ๓๗๕ ๕๕๖๒๕	วิศวกรระบบดับเพลิงอัตโนมัติ	ปรีชา เหมมัน ๓๗๕ ๕๕๖๒๕	เห็นชอบ	ปิยะ มาประเสริฐ ๓๗๕ ๕๕๖๒๕	แผ่นที่/รวม	48/49
	แสดง	แบบขยายครุภัณฑ์	มาตรการสวน		วิศวกรระบบสุขาภิบาล	เฉลิมพร อุดยัณทร ๓๗๕ ๕๕๖๒๕	วิศวกรระบบปรับอากาศ	สุมิตร ศรีวิวัฒน์ ๓๗๕ ๕๕๖๒๕	อนุมัติ	ชูชาติ ช่างชู ๓๗๕ ๕๕๖๒๕		
		ห้องประชุมและห้องทำงาน	เขียน	สนั่น นาคนิก								

ตู้เก็บเอกสาร Low Cabinet CB-01

ขนาด : 430 x 565 x 600 มม จำนวน 6 ตู้



ตู้เก็บพัสดุ CB-02 จำนวน 6 ใบ

ขนาด ตู้บานเปิด มีขนาดไม่น้อยกว่า 118 x 62 x 183 เซนติเมตร



Specification

- แผ่นข้างตู้ : ผลิตจากไม้ Particle Board ความหนา 16 มิลลิเมตร เคลือบผิวด้วย Melamine Resin Film
- แผ่นหลัง : ผลิตจากไม้ Particle Board ความหนา 16 มิลลิเมตร เคลือบผิวด้วย Melamine Resin Film
- แผ่นหลัง : ผลิตจากไม้ Particle Board ความหนา 16 มิลลิเมตร เคลือบผิวด้วย Melamine Resin Film
- หน้าบานเปิด : ผลิตจากไม้ MDF. Board ความหนา 19 มิลลิเมตร ด้วยกรรมวิธีเ็นเบรอน
- อุปกรณ์ Knock-Down KD.Fitting ขนาด 15 และ 25 มิลลิเมตร ของ Hafele
- เยอรมันหรือเทียบเท่า
- วัสดุปิดขอบ : ปิดขอบชิ้นงานในส่วนที่ต้องสัมผัสกับชิ้นงานอื่นด้วย Edge PVC.
- เพื่อป้องกันการกระแทก ซึ่งมีความหนา 1 มิลลิเมตร และปิดขอบชิ้นงานในส่วนที่ไม่ต้องสัมผัสกับชิ้นงานอื่นด้วย Edge PVC เพื่อป้องกันการความชื้น ซึ่งมีความหนา 0.5 มิลลิเมตร
- วัสดุปิดขอบ : ปิดขอบชิ้นงานในส่วนที่ต้องสัมผัสกับชิ้นงานอื่นด้วย Edge PVC.เพื่อป้องกัน
- การกระแทก ซึ่งมีความหนา 1 มิลลิเมตร และปิดขอบชิ้นงานในส่วนที่ไม่ต้องสัมผัสกับชิ้นงานอื่นด้วย Edge PVC เพื่อป้องกันการความชื้น ซึ่งมีความหนา 0.5 มิลลิเมตร
- มือจับ : อุปกรณ์มือจับผลิตจาก Aluminum Alloy Foggy Silver Oxidization-Pilished
- อุปกรณ์บานเปิด : แบบโลหะเคลือบ ของ Hafele จากเยอรมันหรือเทียบเท่า
- กุญแจ : กุญแจคือคานแบบล็อกตลอดถูกกุญแจอยู่ด้านหน้า

รายละเอียดทางเทคนิค

- 1.1 โครงตู้ทำจากเหล็กแผ่นหนาไม่น้อยกว่า 0.6 มิลลิเมตร โครงตู้เป็นแบบถอดประกอบได้ (KNOCK DOWN)
- 1.2 บานประตูทึบทำจากเหล็กแผ่นหนาไม่น้อยกว่า 0.6 มิลลิเมตรพับและอาร์คขึ้นรูป
- 1.3 บานประตูล็อกด้วยระบบกุญแจ
- 1.4 มือจับเป็นพลาสติกฉีดขึ้นรูป มีความคงทนแข็งแรง
- 1.5 ตัววางของภายในเป็นแบบถอดประกอบได้ ขึ้นวางเป็นแบบตายตัว พับขึ้นรูป
- 1.6 ชิ้นส่วนที่เป็นเหล็กทั้งหมด ก่อนพ่นสีจะต้องผ่านการล้างคราบไขมันด้วยเคมี Bio cleaner และเคลือบผิวเหล็ก ด้วยเคมี Dry Inplace Organic Coating เพื่อป้องกันสนิมและเพิ่มการยึดเกาะของสี โดยเคมีที่ใช้ไม่มีโลหะหนักและ สารก่อมะเร็ง จากนั้นนำไปอบแห้งที่อุณหภูมิ 180-200 °C นาน 10 นาที แล้วจึงพ่นสีปิดผิวเหล็กด้วยสีฝุ่นอีพ็อกซี และอบสีที่อุณหภูมิ 200-220 °C นาน 10 นาที
- 1.7 สินค้ารับประกันคุณภาพอย่างน้อย 5 ปี ในสภาพการใช้งานปกติ รายละเอียดตามใบรับประกันสินค้า

Property Management Department ฝ่ายบริหารทรัพย์สิน ส่วนอำนวยการควบคุมอาคาร	เจ้าของโครงการ	ฝ่ายพัฒนาผลิตภัณฑ์ระหว่างประเทศ	สถาปนิก	สนั่น นาคนิกร ๙-๙๘๖๑๙	วิศวกรระบบไฟฟ้ากำลัง	เฉลิมชัย พงษ์พานิช ๙๖๒๕	วิศวกรระบบป้องกันอัคคีภัย	ประทีป อินทรศักดิ์ ๙๖๓๗	ตรวจ	วิมล ๙๖๓๗	เลขที่แบบ	A-49
	แบบ	งานจ้างเหมาก่อสร้างอาคารพาณิชย์โครงการขยายเขตเปิดโล่ง ปากบารา อ.ละงู จ.สตูล พร้อมงานติดตั้งระบบปรับอากาศ และงานรื้อถอน	วิศวกรโครงสร้าง	เอกสิทธิ์ จิระชัยเกียรติ ๙๖๕๗๗	วิศวกรระบบควบคุมอัตโนมัติ	พงษ์ศักดิ์ บุญทวี ๙๖๕๗๔	วิศวกรระบบดับเพลิงอัตโนมัติ	ปรีชา เหมมัน ๙๖๓๐๑๔	เห็นชอบ	วิมล ๙๖๓๗	แผ่นที่/รวม	49/49
	แสดง	แบบขยายงานครุภัณฑ์ ตู้เก็บพัสดุ CB-02	มาตราส่วน		วิศวกรระบบสุขาภิบาล	เฉลิมพล อุดมบุตร ๙๖๒๓๕	วิศวกรระบบปรับอากาศ	สุมิตร ศรีวิวัฒน์ ๙๖๑๐๖๖๕	อนุมัติ	วิมล ๙๖๓๗		
	ตู้เก็บเอกสาร Low Cabinet CB-01	เขียน	สนั่น นาคนิกร						รูชาติ ชัยสุข	๙๖๓๗		